



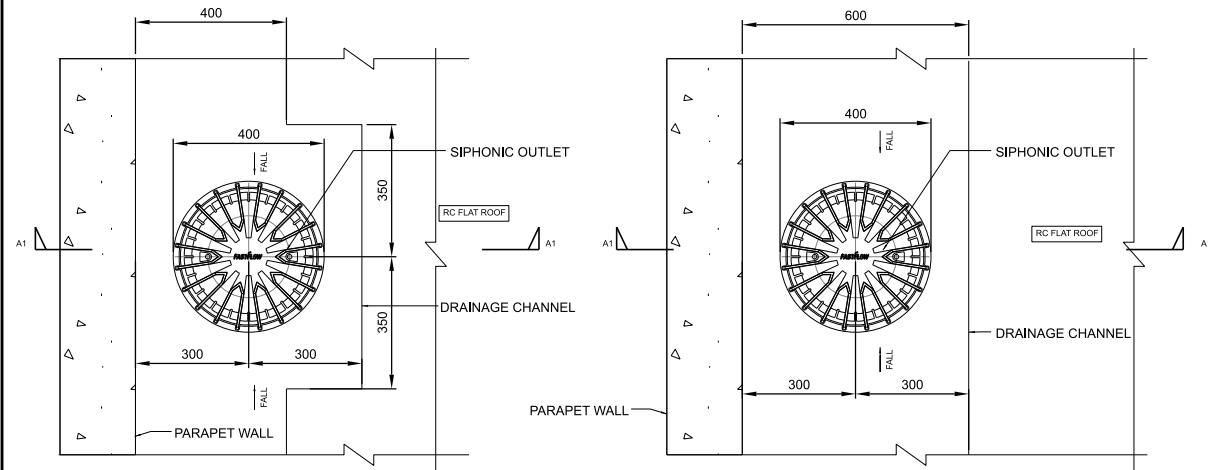


**TYPE-1
LOCALISED POCKET SCUPPER DETAIL**
1:10


**TYPE-2
WIDE SCUPPER DETAIL**
1:10

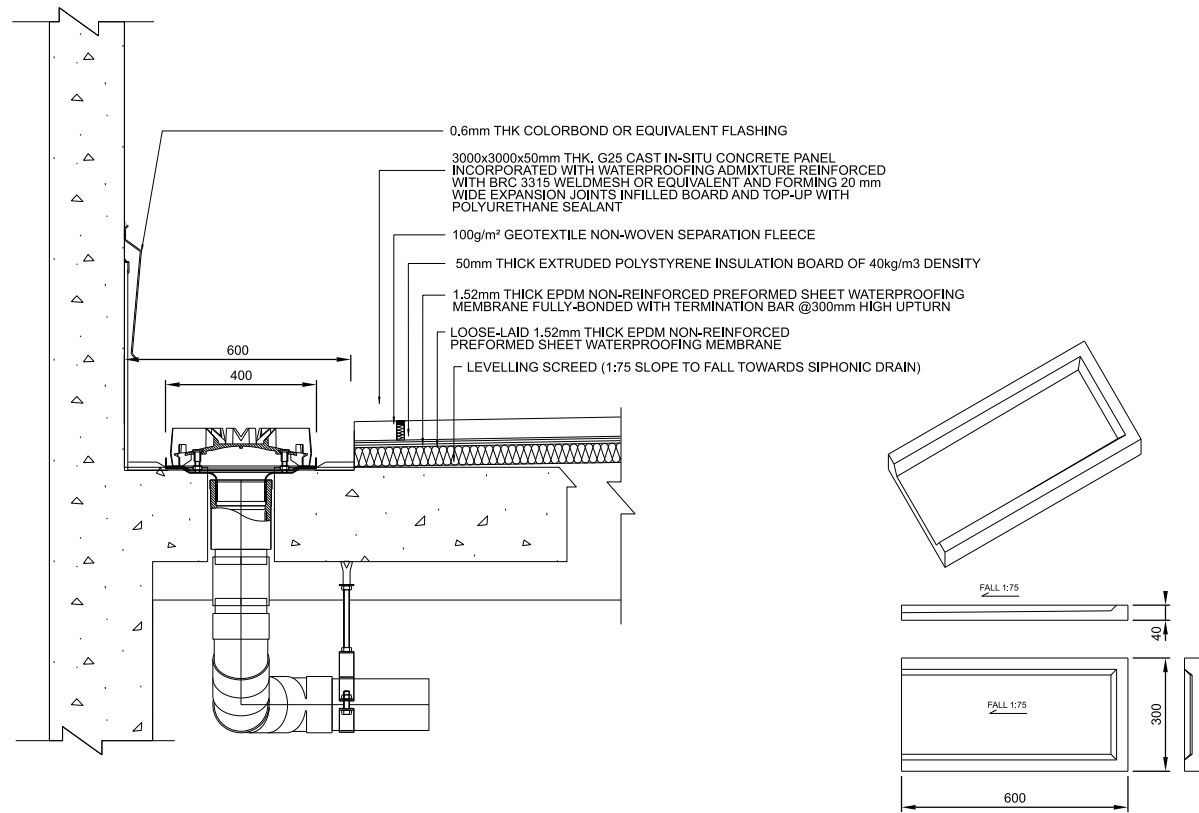

**TYP. WATERPROOFING DETAIL - SECTION A1-A1
SIPHONIC OUTLET ON RC ROOF NEAR PARAPET WALL**
1:10

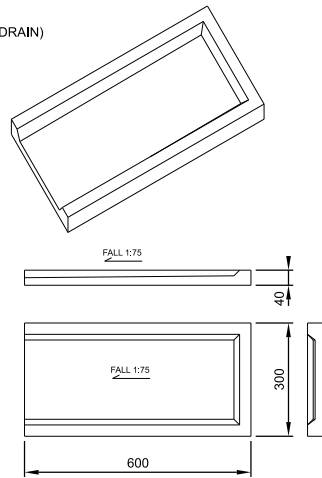


CONCRETE SPLASH BLOCK
NTS

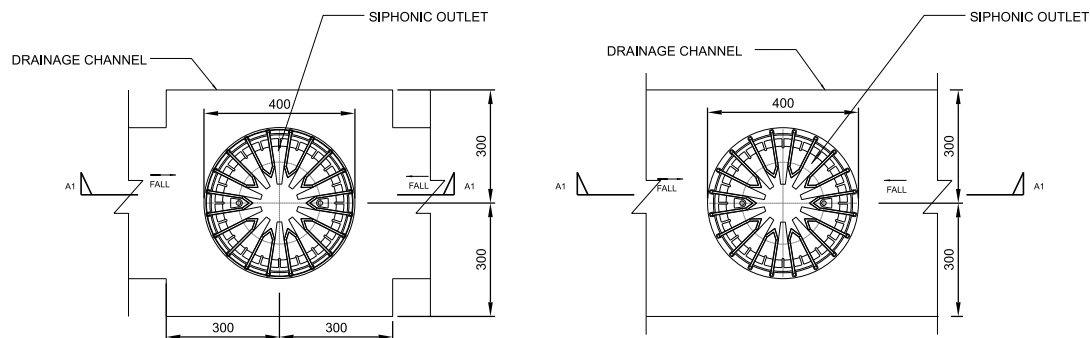


**TYPE-1
LOCALISED POCKET SCUPPER DETAIL**
1:10

**TYPE-2
LOCALISED POCKET SCUPPER DETAIL**
1:10

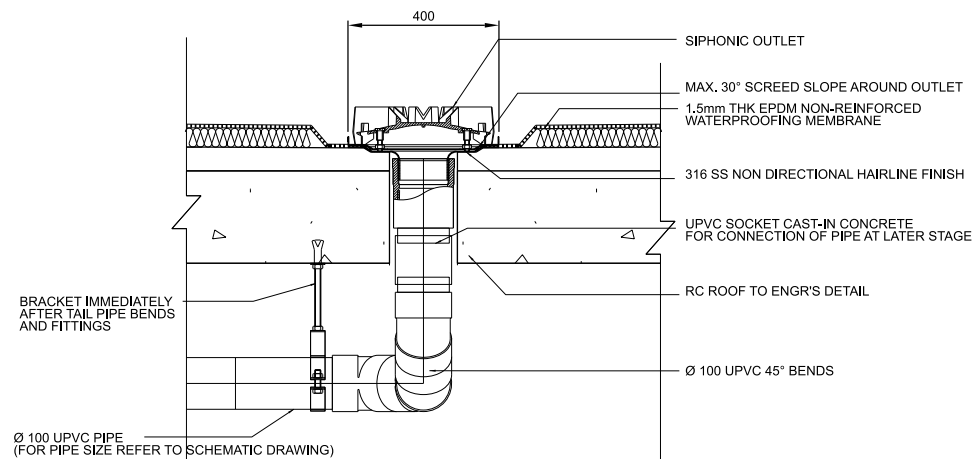

**TYP. WATERPROOFING DETAIL - SECTION A1-A1
SIPHONIC OUTLET ON RC ROOF**
1:10

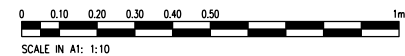

TENDER

REV	DATE	DESCRIPTION	REVIEWED	AUTHORISED
T1	20/05/22	ISSUED FOR TENDER C4B	PK	GOT

CLIENT:



PROGRAMME MANAGER:



CONSULTANT:



PROJECT TITLE:

**TUAS WATER RECLAMATION PLANT (TWRP)
DTSS PHASE 2**

DRAWING TITLE:

**ARCHITECTURAL
STANDARD DETAILS
SIPHONIC OUTLET
AND SPLASH BLOCK**

DRAFTED: SP	DESIGNED: SP	SHEET SIZE: A1
DRAFTING CHECK: DW	DESIGN CHECK: PE	SCALE: AS SHOWN
DATE: 24/07/18	REVIEWED: PK	PBS: 131101

CONTRACT: C4B	DRAWING NUMBER: PUB-DTSS2-TWRP	REVISION: T1
	SHEET NUMBER: WSW41-A-5002	

THIS DRAWING IS COPYRIGHT