


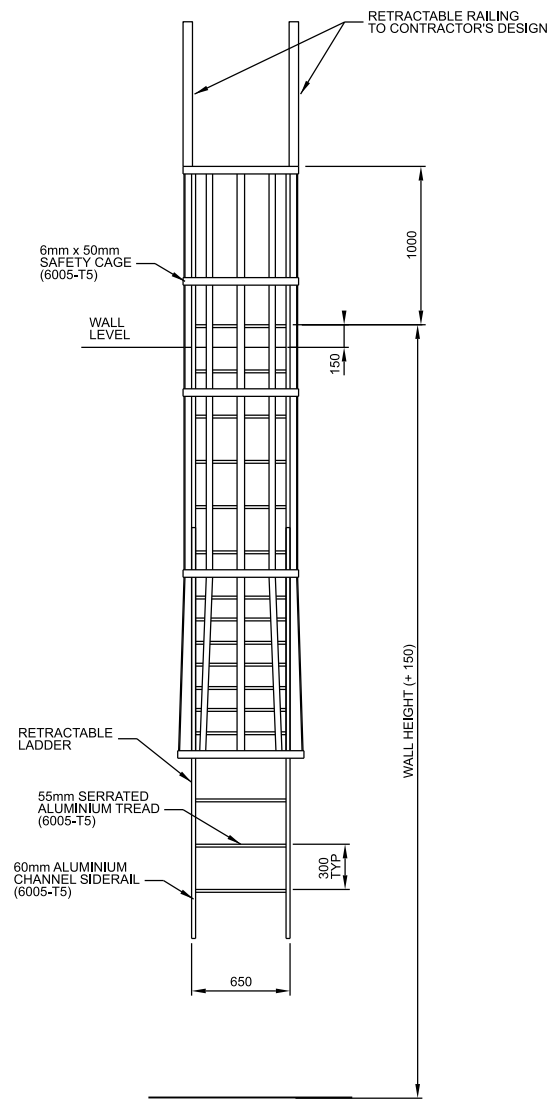


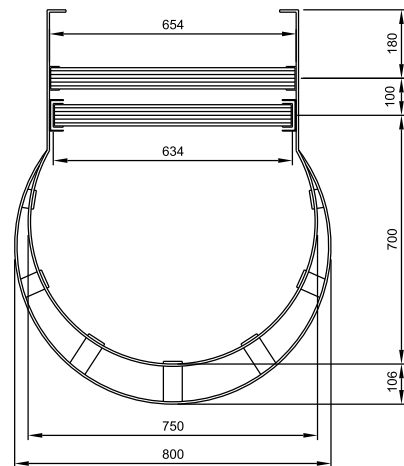

FIRE ESCAPE CAT LADDER
1:25

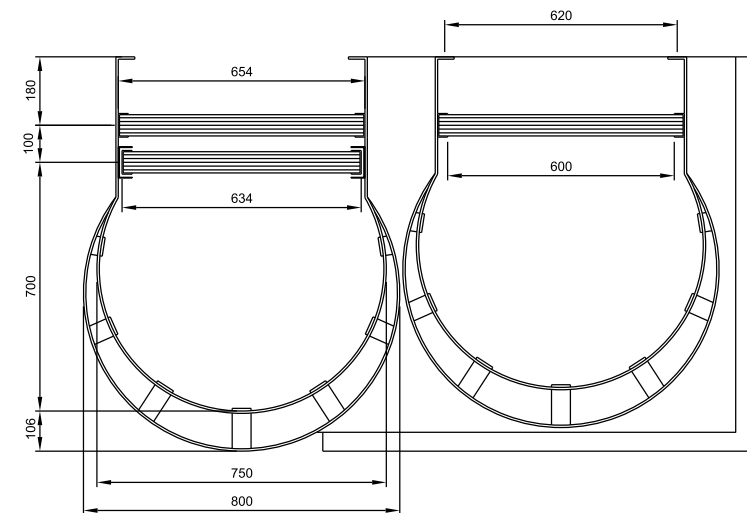

CAT LADDER PLAN
(PARAPET PLATFORM & RETURN
LADDER ARE OMITTED FOR CLARITY)

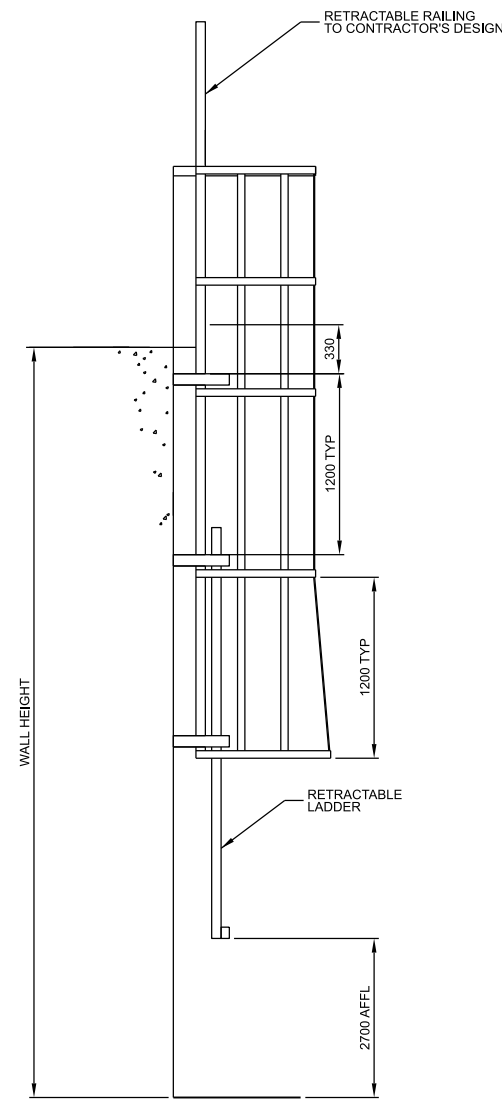


CAT LADDER PLAN WITH INTERMEDIATE LANDING
(PARAPET PLATFORM & RETURN
LADDER ARE OMITTED FOR CLARITY)

NOTES:

1. ALL DIMENSIONS ARE IN MILLIMETRES UNLESS OTHERWISE STATED.
2. ALL BOLTS/FASTENERS NECESSARY TO ANCHOR LADDER ARE BY OTHERS.

CAT LADDER DETAIL
BRACKET DETAIL TO STRUCTURE ON TOP
FACTORY FINISH ALUMINIUM-MILL FINISH

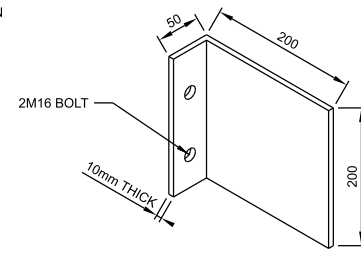

6mm x 50mm
SAFETY CAGE
(6005-T5)


RETRACTABLE
LADDER

55mm SERRATED
ALUMINIUM TREAD
(6005-T5)

60mm ALUMINIUM
CHANNEL SIDERAIL
(6005-T5)

FIRE ESCAPE CAT LADDER WITH INTERMEDIATE LANDING

1:25

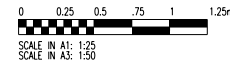

TENDER

T1	20/05/22	ISSUED FOR TENDER C4B	PK	GOT
REV	DATE	DESCRIPTION	REVIEWED	AUTHORISED

CLIENT:



PROGRAMME MANAGER:



CONSULTANT:



PROJECT TITLE:

TUAS WATER RECLAMATION PLANT (TWRP)
DTSS PHASE 2

DRAWING TITLE

ARCHITECTURAL
FIRE ESCAPE
CAT LADDER
& INTERMEDIATE

DRAFTED: SP	DESIGNED: SP	SHEET SIZE: A1
DRAFTING CHECK: DW	DESIGN CHECK: PE	SCALE: AS SHOWN
DATE: 08/04/18	REVIEWED: PK	PBS: 131101

CONTRACT: C4B	DRAWING NUMBER: PUB-DTSS2-TWRP	REVISION: T1
SHEET NUMBER: WSW41-A-5004		

THIS DRAWING IS COPYRIGHT