




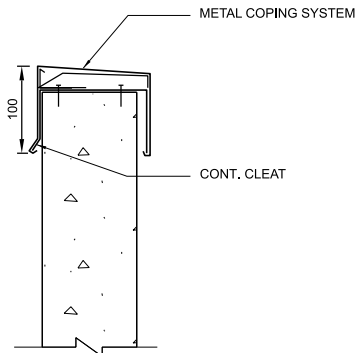


TYP. WATERPROOFING DETAIL
PARAPET WALL
1:5

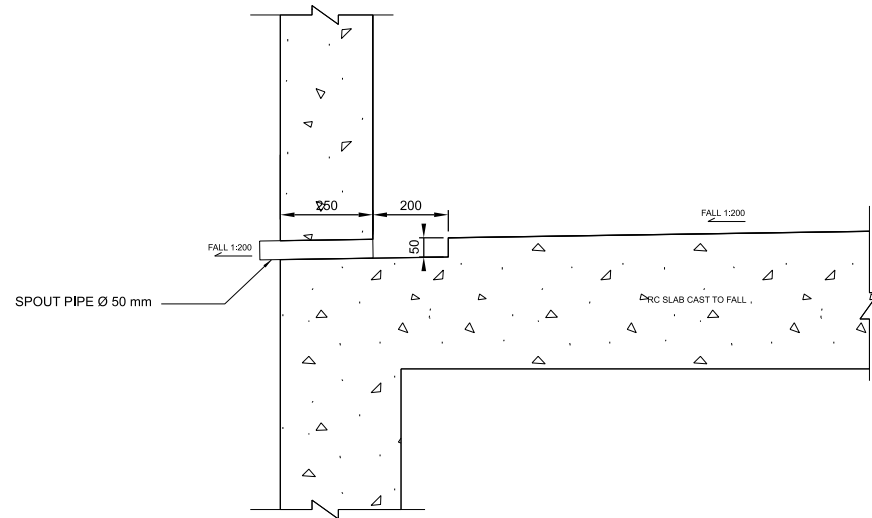



TYP. WATERPROOFING DETAIL - SECTION A1-A1
SPOUT PIPE DISCHARGE
1:10

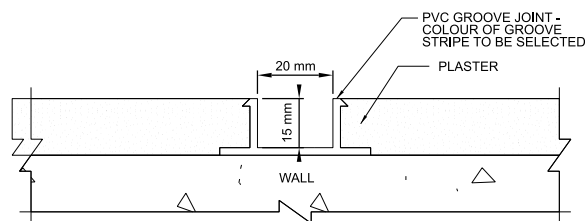


TYP. GROOVE JOINT
1:1

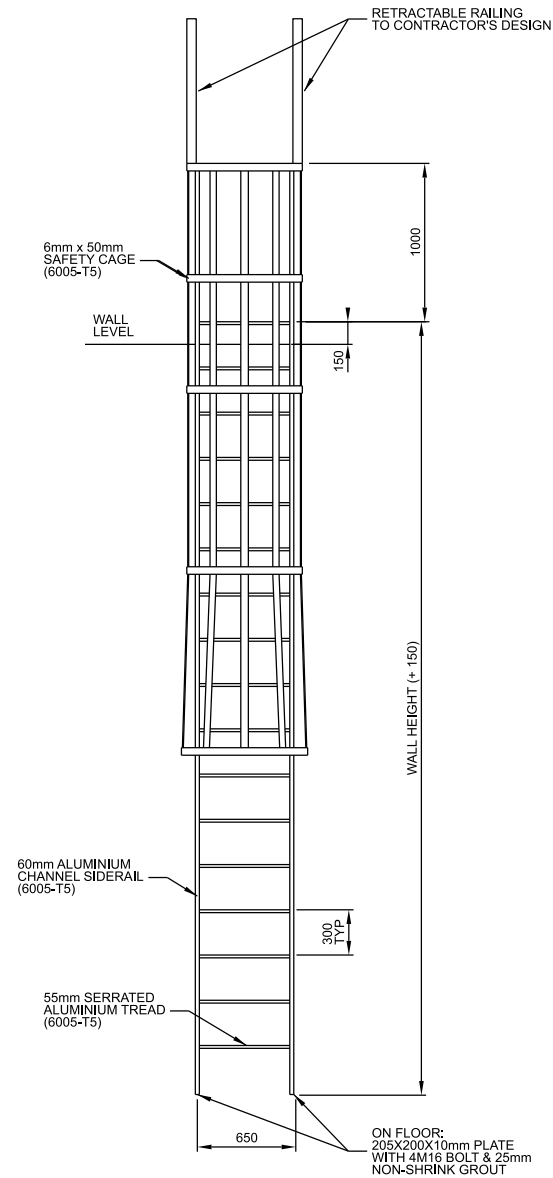

CAT LADDER WITH RETRACTABLE HANDLE
1:25

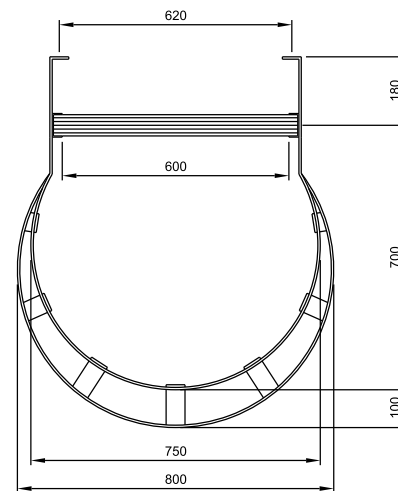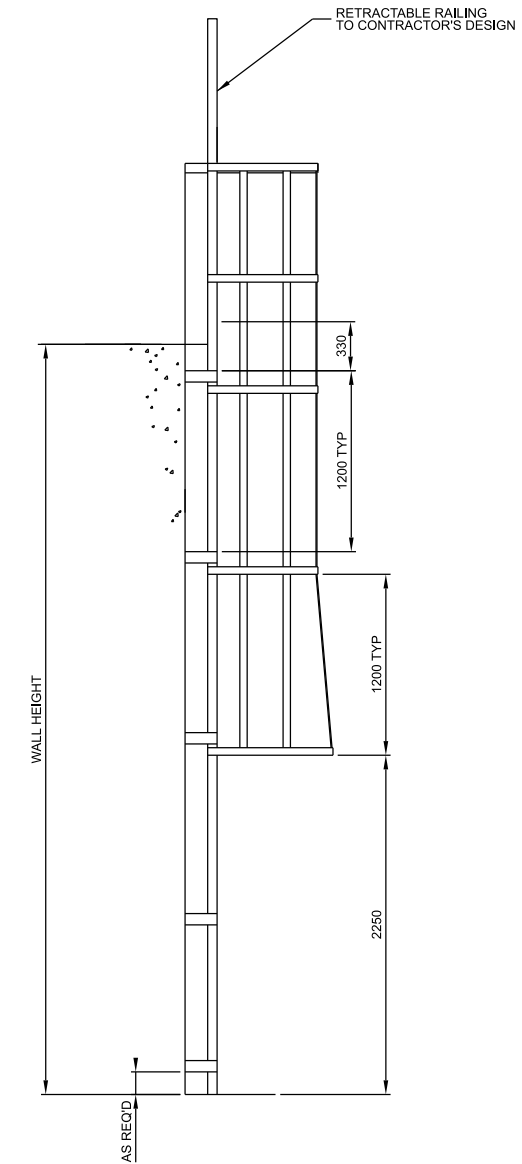



CAT LADDER PLAN
(PARAPET PLATFORM & RETURN
LADDER ARE OMITTED FOR CLARITY)

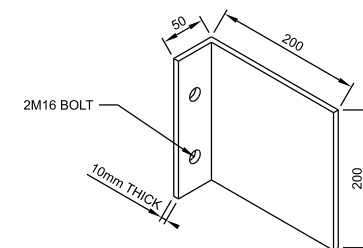

CAT LADDER DETAIL
BRACKET DETAIL TO STRUCTURE ON TOP
FACTORY FINISH ALUMINIUM-MILL FINISH

NOTES:

- ALL DIMENSIONS ARE IN MILLIMETRES UNLESS OTHERWISE STATED.
- ALL BOLTS/FASTENERS NECESSARY TO ANCHOR LADDER ARE BY OTHERS.

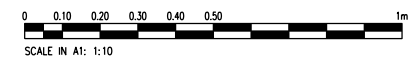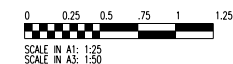

TENDER			
T1	20/05/22	ISSUED FOR TENDER C48	PK
REV	DATE	DESCRIPTION	REVIEWED
GOT		AUTHORISED	
CLIENT:			
 PUB SINGAPORE'S NATIONAL WATER AGENCY			
PROGRAMME MANAGER:			
 A JOINT VENTURE DELIVERING THE DTSS2 PROJECT			
CONSULTANT:			
 CH2M HILL Singapore Pte Ltd			
PROJECT TITLE:			
TUAS WATER RECLAMATION PLANT (TWRP) DTSS PHASE 2			
DRAWING TITLE			
ARCHITECTURAL STANDARD DETAILS PARAPET, GROOVES AND CAT LADDER			
DRAFTED: SP	DESIGNED: SP	SHEET SIZE: A1	
DRAFTING CHECK: DW	DESIGN CHECK: PE	SCALE: AS SHOWN	
DATE: 02/08/18	REVIEWED: PK	PBS: 131101	
CONTRACT:		DRAWING NUMBER:	
C4B	PUB-DTSS2-TWRP		
	SHEET NUMBER: WSW41-A-5005		REVISION: T1
THIS DRAWING IS COPYRIGHT			