




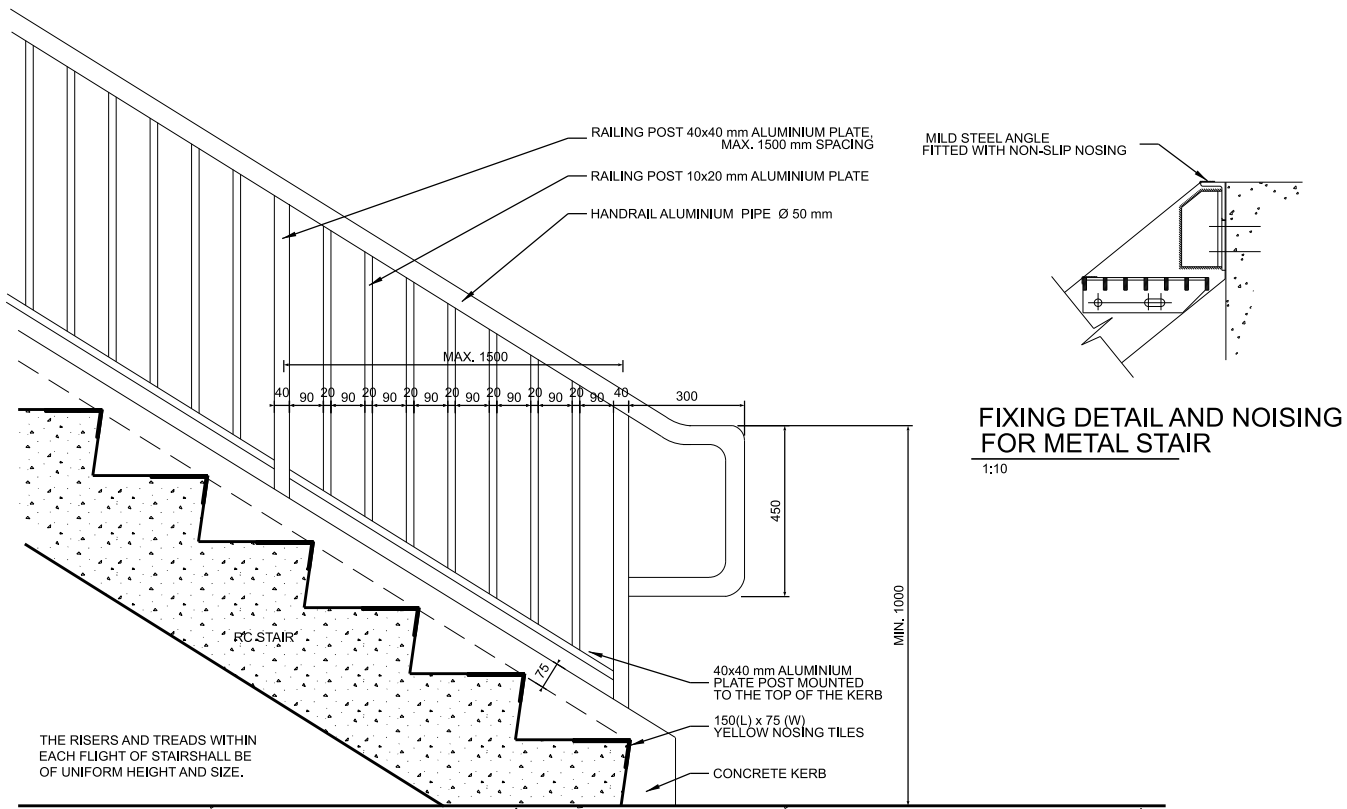

TYP. CONCRETE STAIRCASE DETAIL
1:10

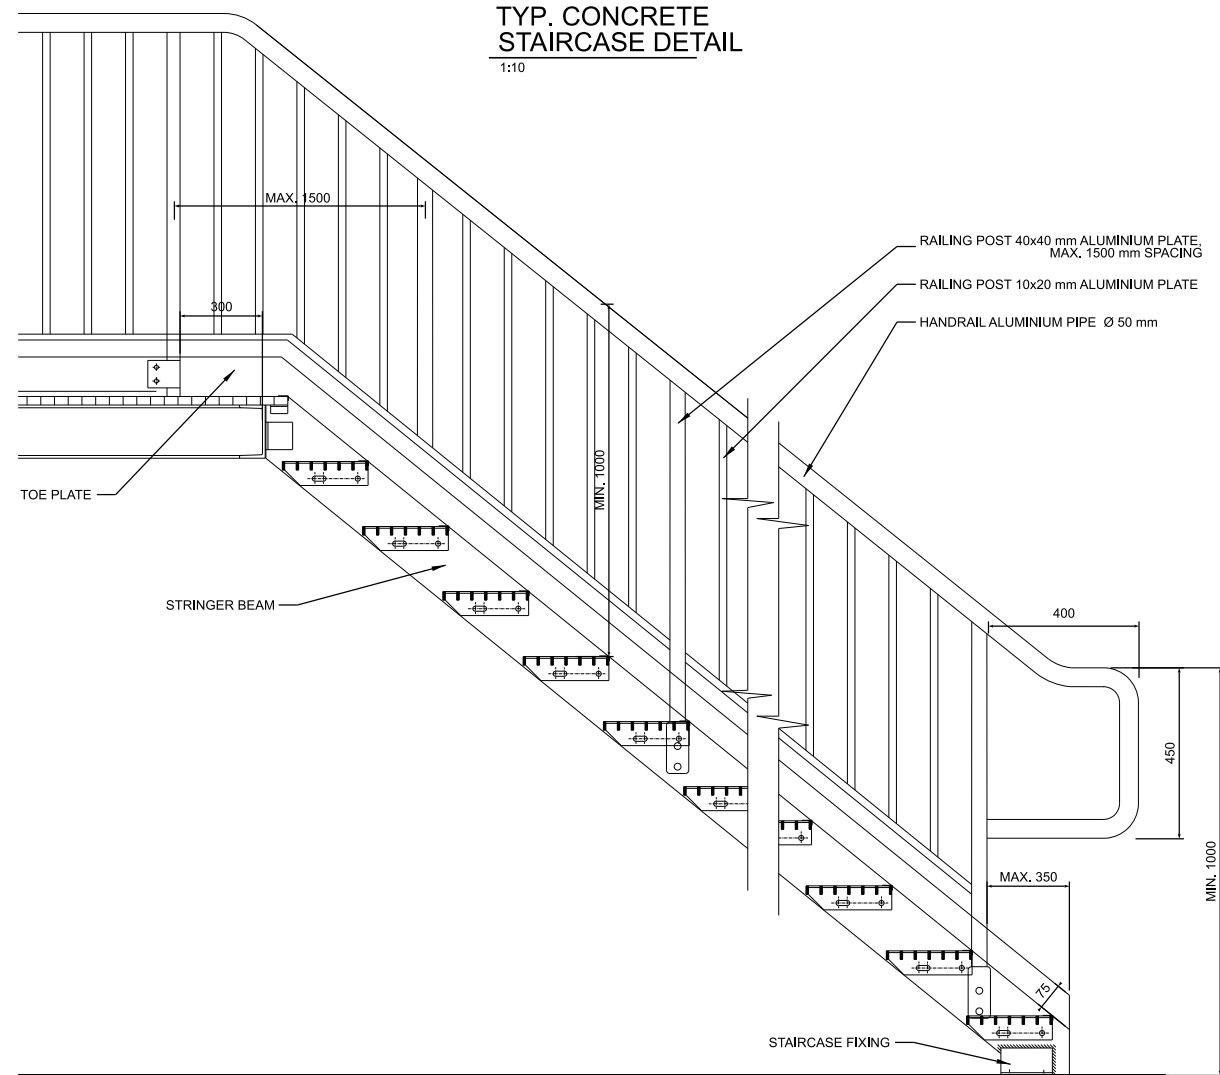


TYP. METAL STAIRCASE AND RAILING DETAIL
1:10

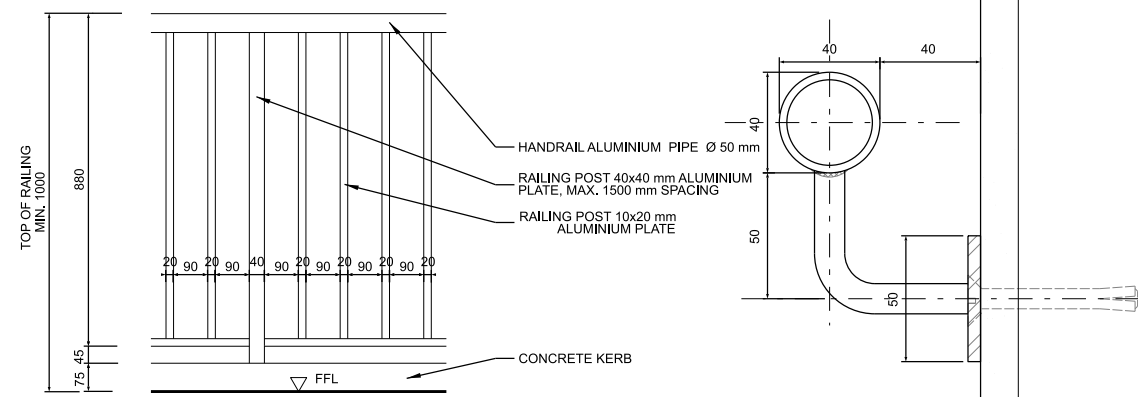


TYP. RAILING ON KERB DETAIL
1:10


TYP. HANDRAIL DETAIL
NTS

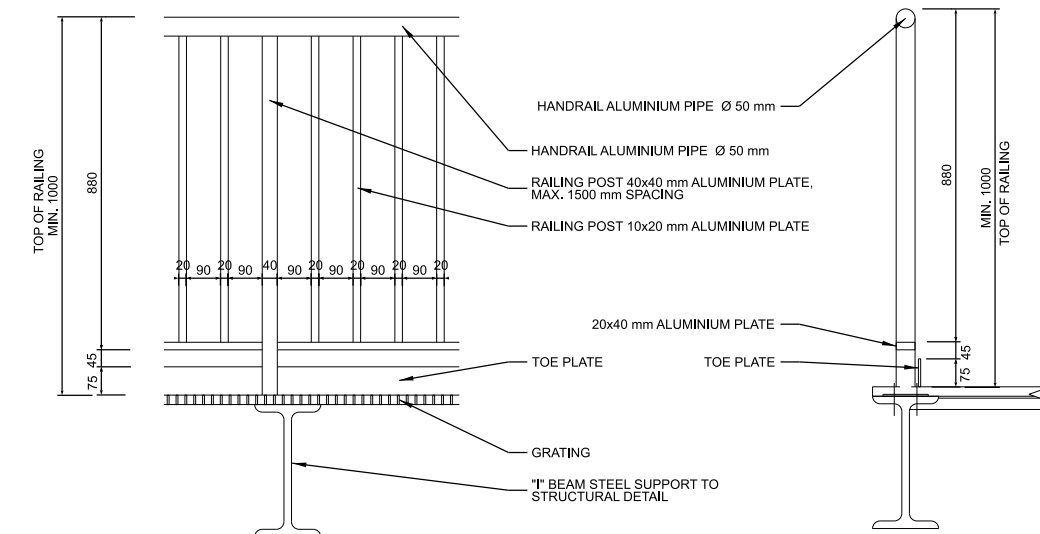

TYP. RAILING ON METAL PLATFORM DETAIL
1:10

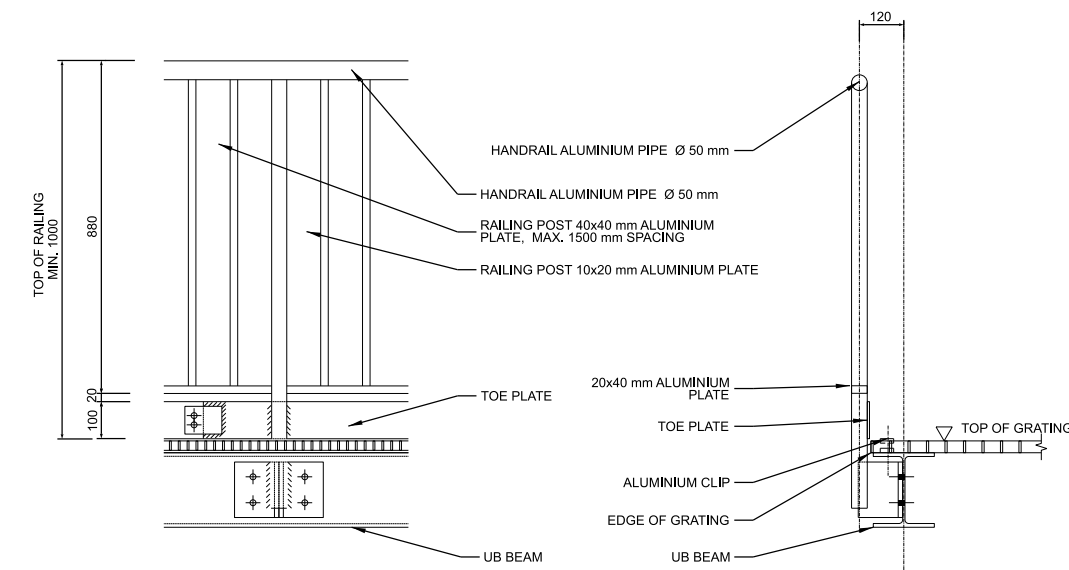

TYP. RAILING FOR CATWALK/PLATFORM
1:10

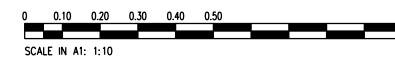

TENDER

REV	DATE	DESCRIPTION	PK	GOT
T1	20/05/22	ISSUED FOR TENDER C4B	PK	GOT
REV	DATE	DESCRIPTION	REVIEWED	AUTHORISED

CLIENT:



PROGRAMME MANAGER:



CONSULTANT:



PROJECT TITLE:

TUAS WATER RECLAMATION PLANT (TWRP)
DTSS PHASE 2

DRAWING TITLE:

ARCHITECTURAL
STANDARD DETAILS
RAILINGS

DRAFTED: AKO	DESIGNED: AKO	SHEET SIZE: A1
DRAWING CHECK: DW	DESIGN CHECK: PE	SCALE: AS SHOWN
DATE: 02/08/18	REVIEWED: PK	PBS: 131101
CONTRACT: C4B	DRAWING NUMBER: PUB-DTSS2-TWRP	SHEET NUMBER: WSW41-A-5006
		REVISION: T1

THIS DRAWING IS COPYRIGHT