



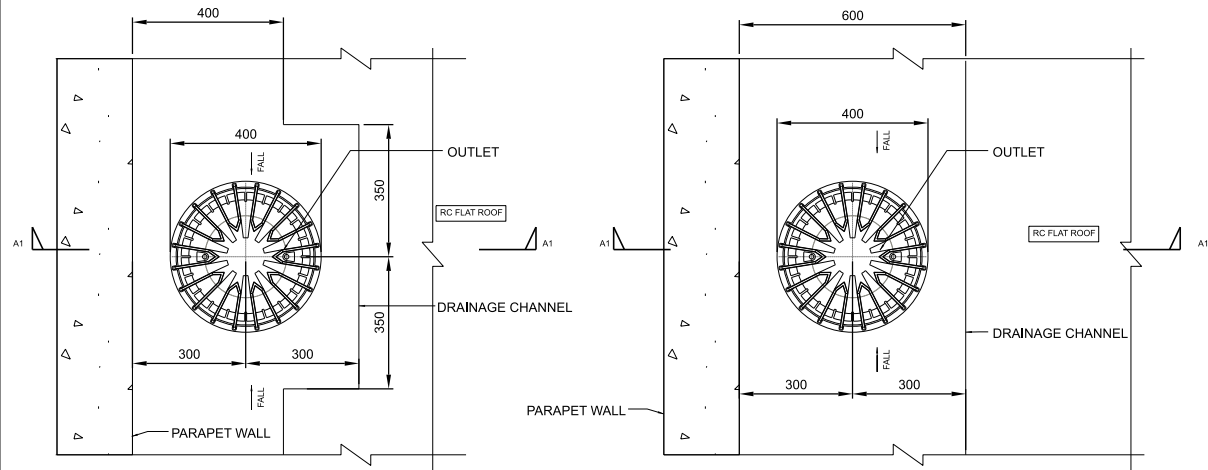


**TYPE-1
LOCALISED POCKET SCUPPER DETAIL**
1:10

**TYPE-2
WIDE SCUPPER DETAIL**
1:10

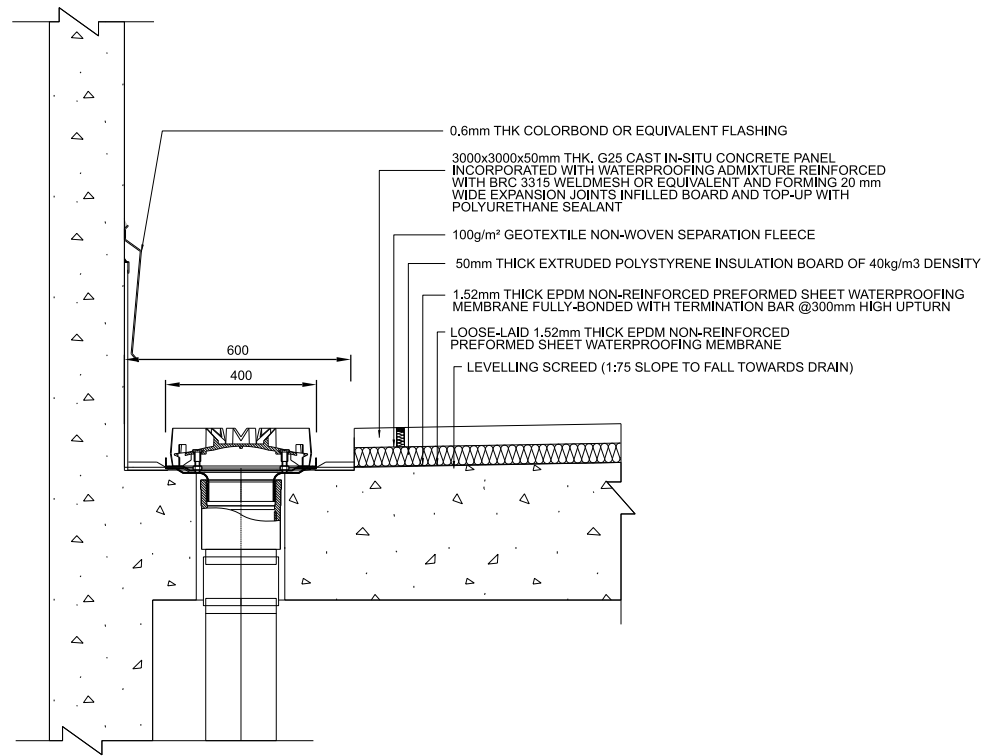


**TYP. WATERPROOFING DETAIL - SECTION A1-A1
OUTLET ON RC ROOF NEAR PARAPET WALL**
1:10

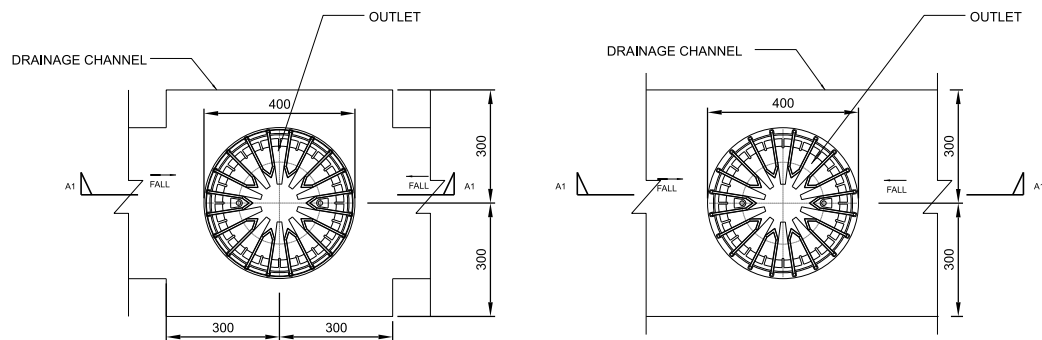


**TYPE-1
LOCALISED POCKET SCUPPER DETAIL**
1:10

**TYPE-2
LOCALISED POCKET SCUPPER DETAIL**
1:10

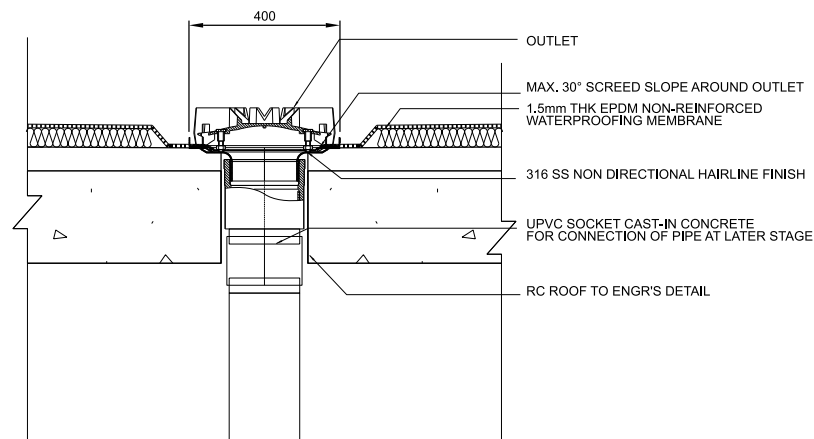

**TYP. WATERPROOFING DETAIL - SECTION A1-A1
OUTLET ON RC ROOF**
1:10

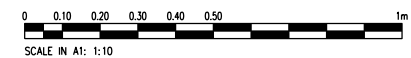

TENDER

T1	20/05/22	ISSUED FOR TENDER C4B	PK	GOT
REV	DATE	DESCRIPTION	REVIEWED	AUTHORISED

CLIENT:



PROGRAMME MANAGER:



CONSULTANT:



PROJECT TITLE:

**TUAS WATER RECLAMATION PLANT (TWRP)
DTSS PHASE 2**

DRAWING TITLE:

**ARCHITECTURAL
STANDARD DETAILS
CONVENTIONAL OUTLET**

DRAFTED: SP	DESIGNED: SP	SHEET SIZE: A1
DRAFTING CHECK: DW	DESIGN CHECK: PE	SCALE: AS SHOWN
DATE: 01/07/20	REVIEWED: PK	PBS: 131101
CONTRACT: C4B	DRAWING NUMBER: PUB-DTSS2-TWRP	REVISION: T1
	SHEET NUMBER: WSW41-A-5007	

THIS DRAWING IS COPYRIGHT