
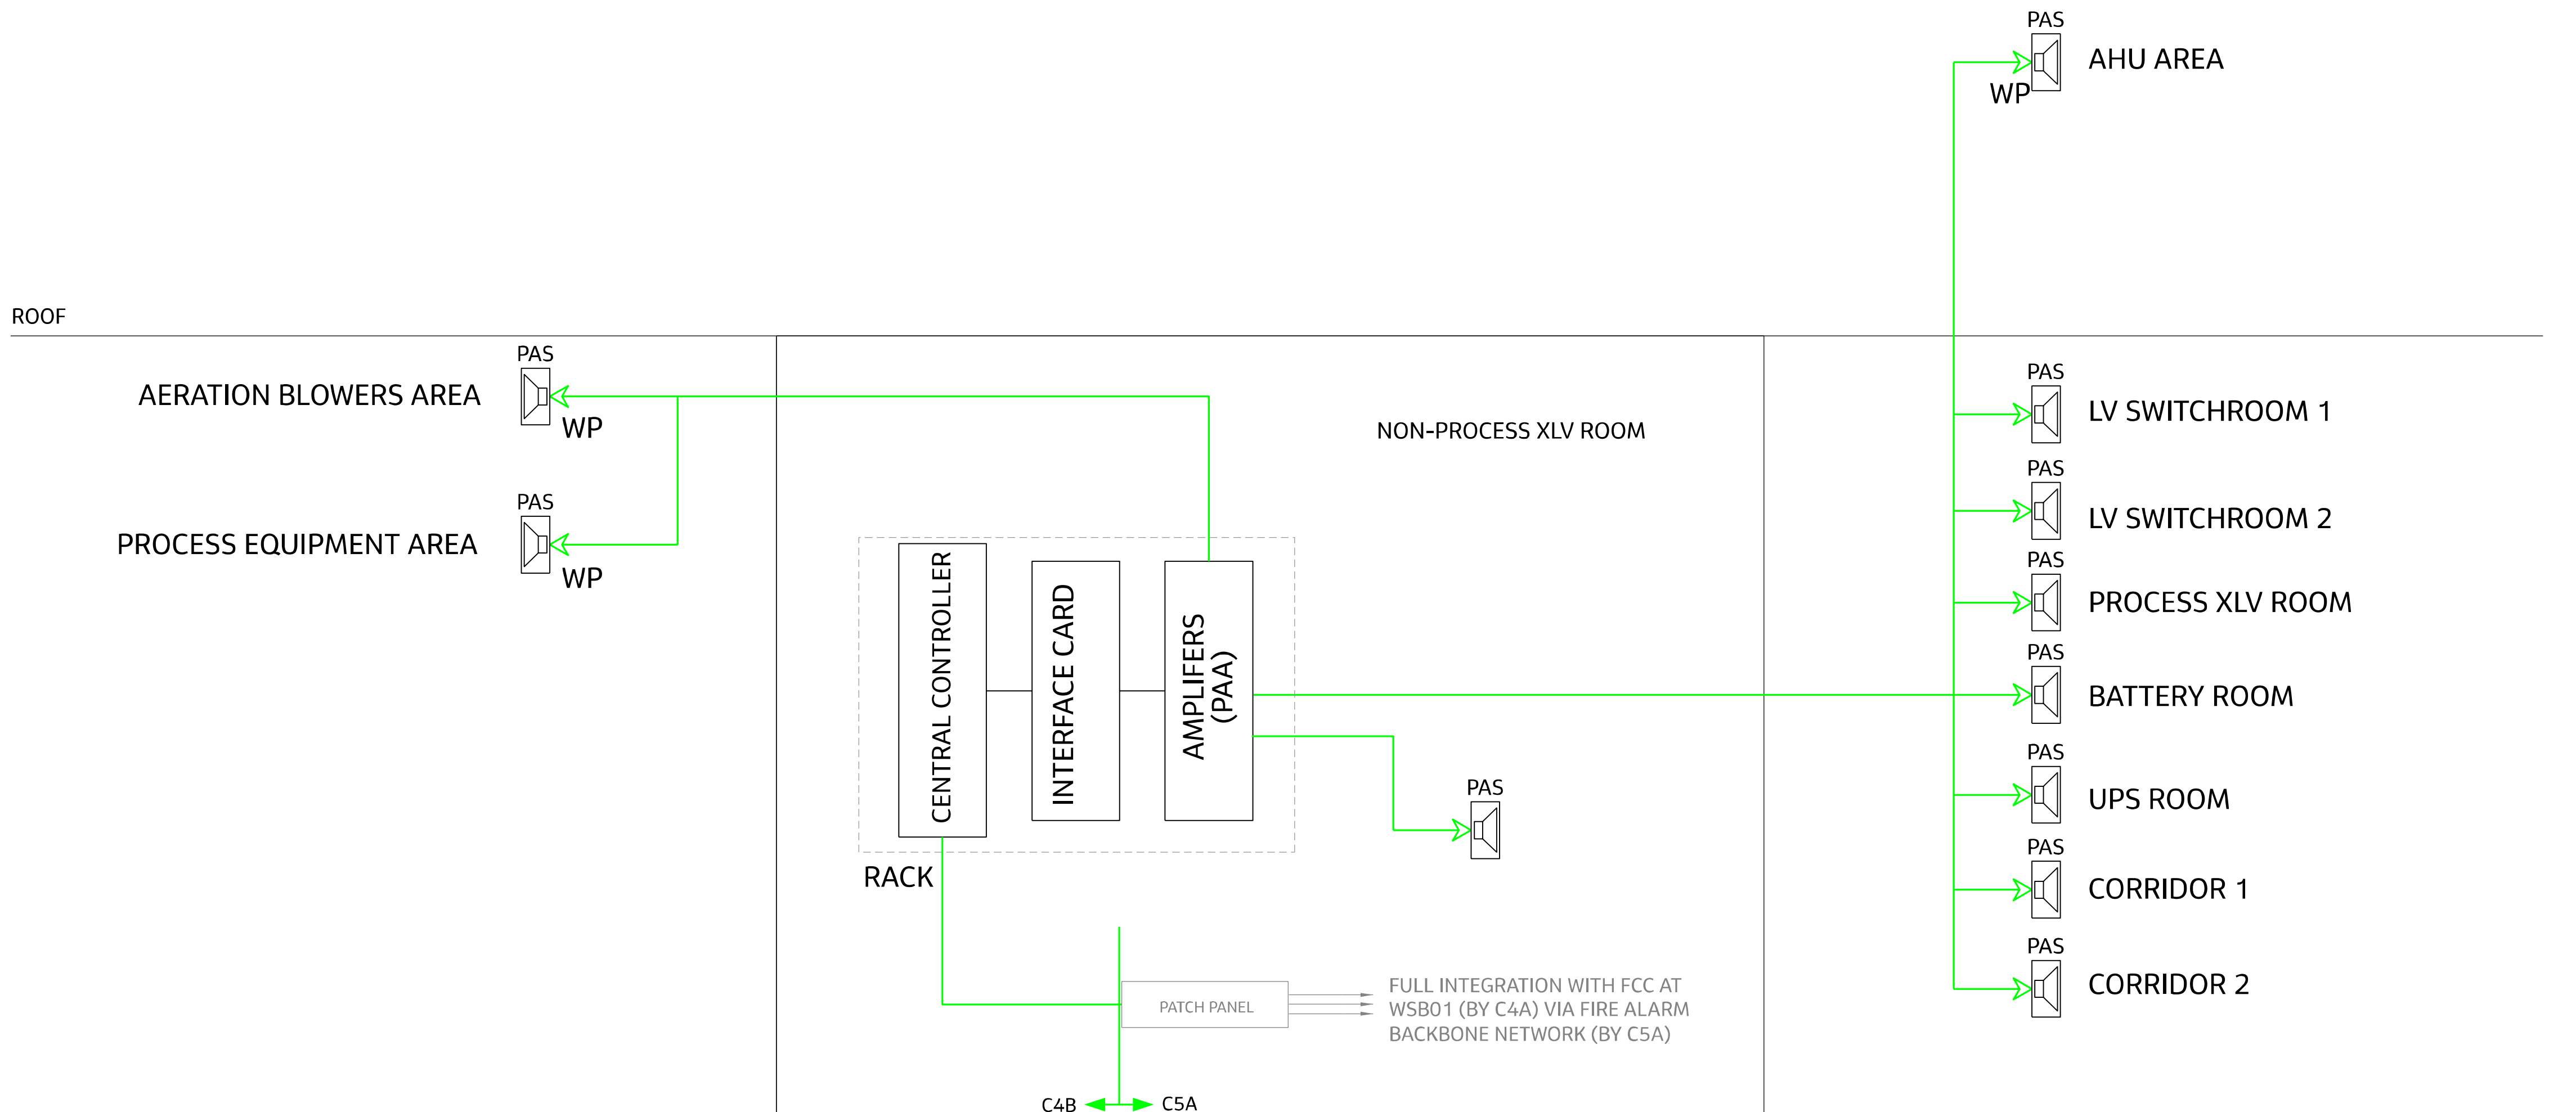


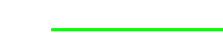

- NOTE:-**
1. QUANTITIES, LOCATION, NUMBER OF STOREY SHOWN ARE FOR INDICATIVE PURPOSES ONLY.
 2. THE SCHEMATIC IS INDICATIVE AND THE CONTRACTOR SHALL BE RESPONSIBLE FOR CONFIRMING THE FINAL QUANTITIES AND CONFIGURATION THAT COMPLY WITH THE LATEST REVISION OF THE CODE OF PRACTICE FOR EMERGENCY VOICE COMMUNICATION SYSTEMS IN BUILDINGS AND FIRE CODE AT THE TIME OF CONSTRUCTION.
 3. THE CONTRACTOR SHALL BE RESPONSIBLE FOR PROVIDING DESIGN DETAILS TO THE S.O. FOR APPROVAL PRIOR TO INSTALLATION.

LEGEND

 FIBRE OPTIC CABLE

 PUBLIC ADDRESS SPEAKERS - BOX SPEAKER

ABBREVIATIONS

PAA PUBLIC ADDRESS AMPLIFIERS

TENDER

T1	20/05/22	ISSUED FOR TENDER	HKT	HKT
REV	DATE	DESCRIPTION	REVIEWED	AUTHORISED

CLIENT:



SINGAPORE'S
NATIONAL
WATER AGENCY

PROGRAMME MANAGER:



AECOM

A JOINT VENTURE DELIVERING THE DTSS2 PROJECT

CONSULTANT:



CH2M HILL Singapore Pte Ltd

PROJECT TITLE:

TUAS WATER RECLAMATION PLANT (TWRP)
DTSS PHASE 2

DRAWING TITLE:

SIDESTREAM NITROGEN REMOVAL (WST02)
SCHEMATIC FOR PUBLIC ADDRESS
SYSTEM

DRAFTED: EZ	DESIGNED: EZ	SHEET SIZE: A1
DRAFTING CHECK: HKT	DESIGN CHECK: HKT	SCALE: NTS
DATE: 21/03/22	REVIEWED: HKT	PBS: 131101
CONTRACT:	DRAWING NUMBER: PUB-DTSS2-TWRP	
C4B	SHEET NUMBER: WST02-B-7103	REVISION: T1

THIS DRAWING IS COPYRIGHT