


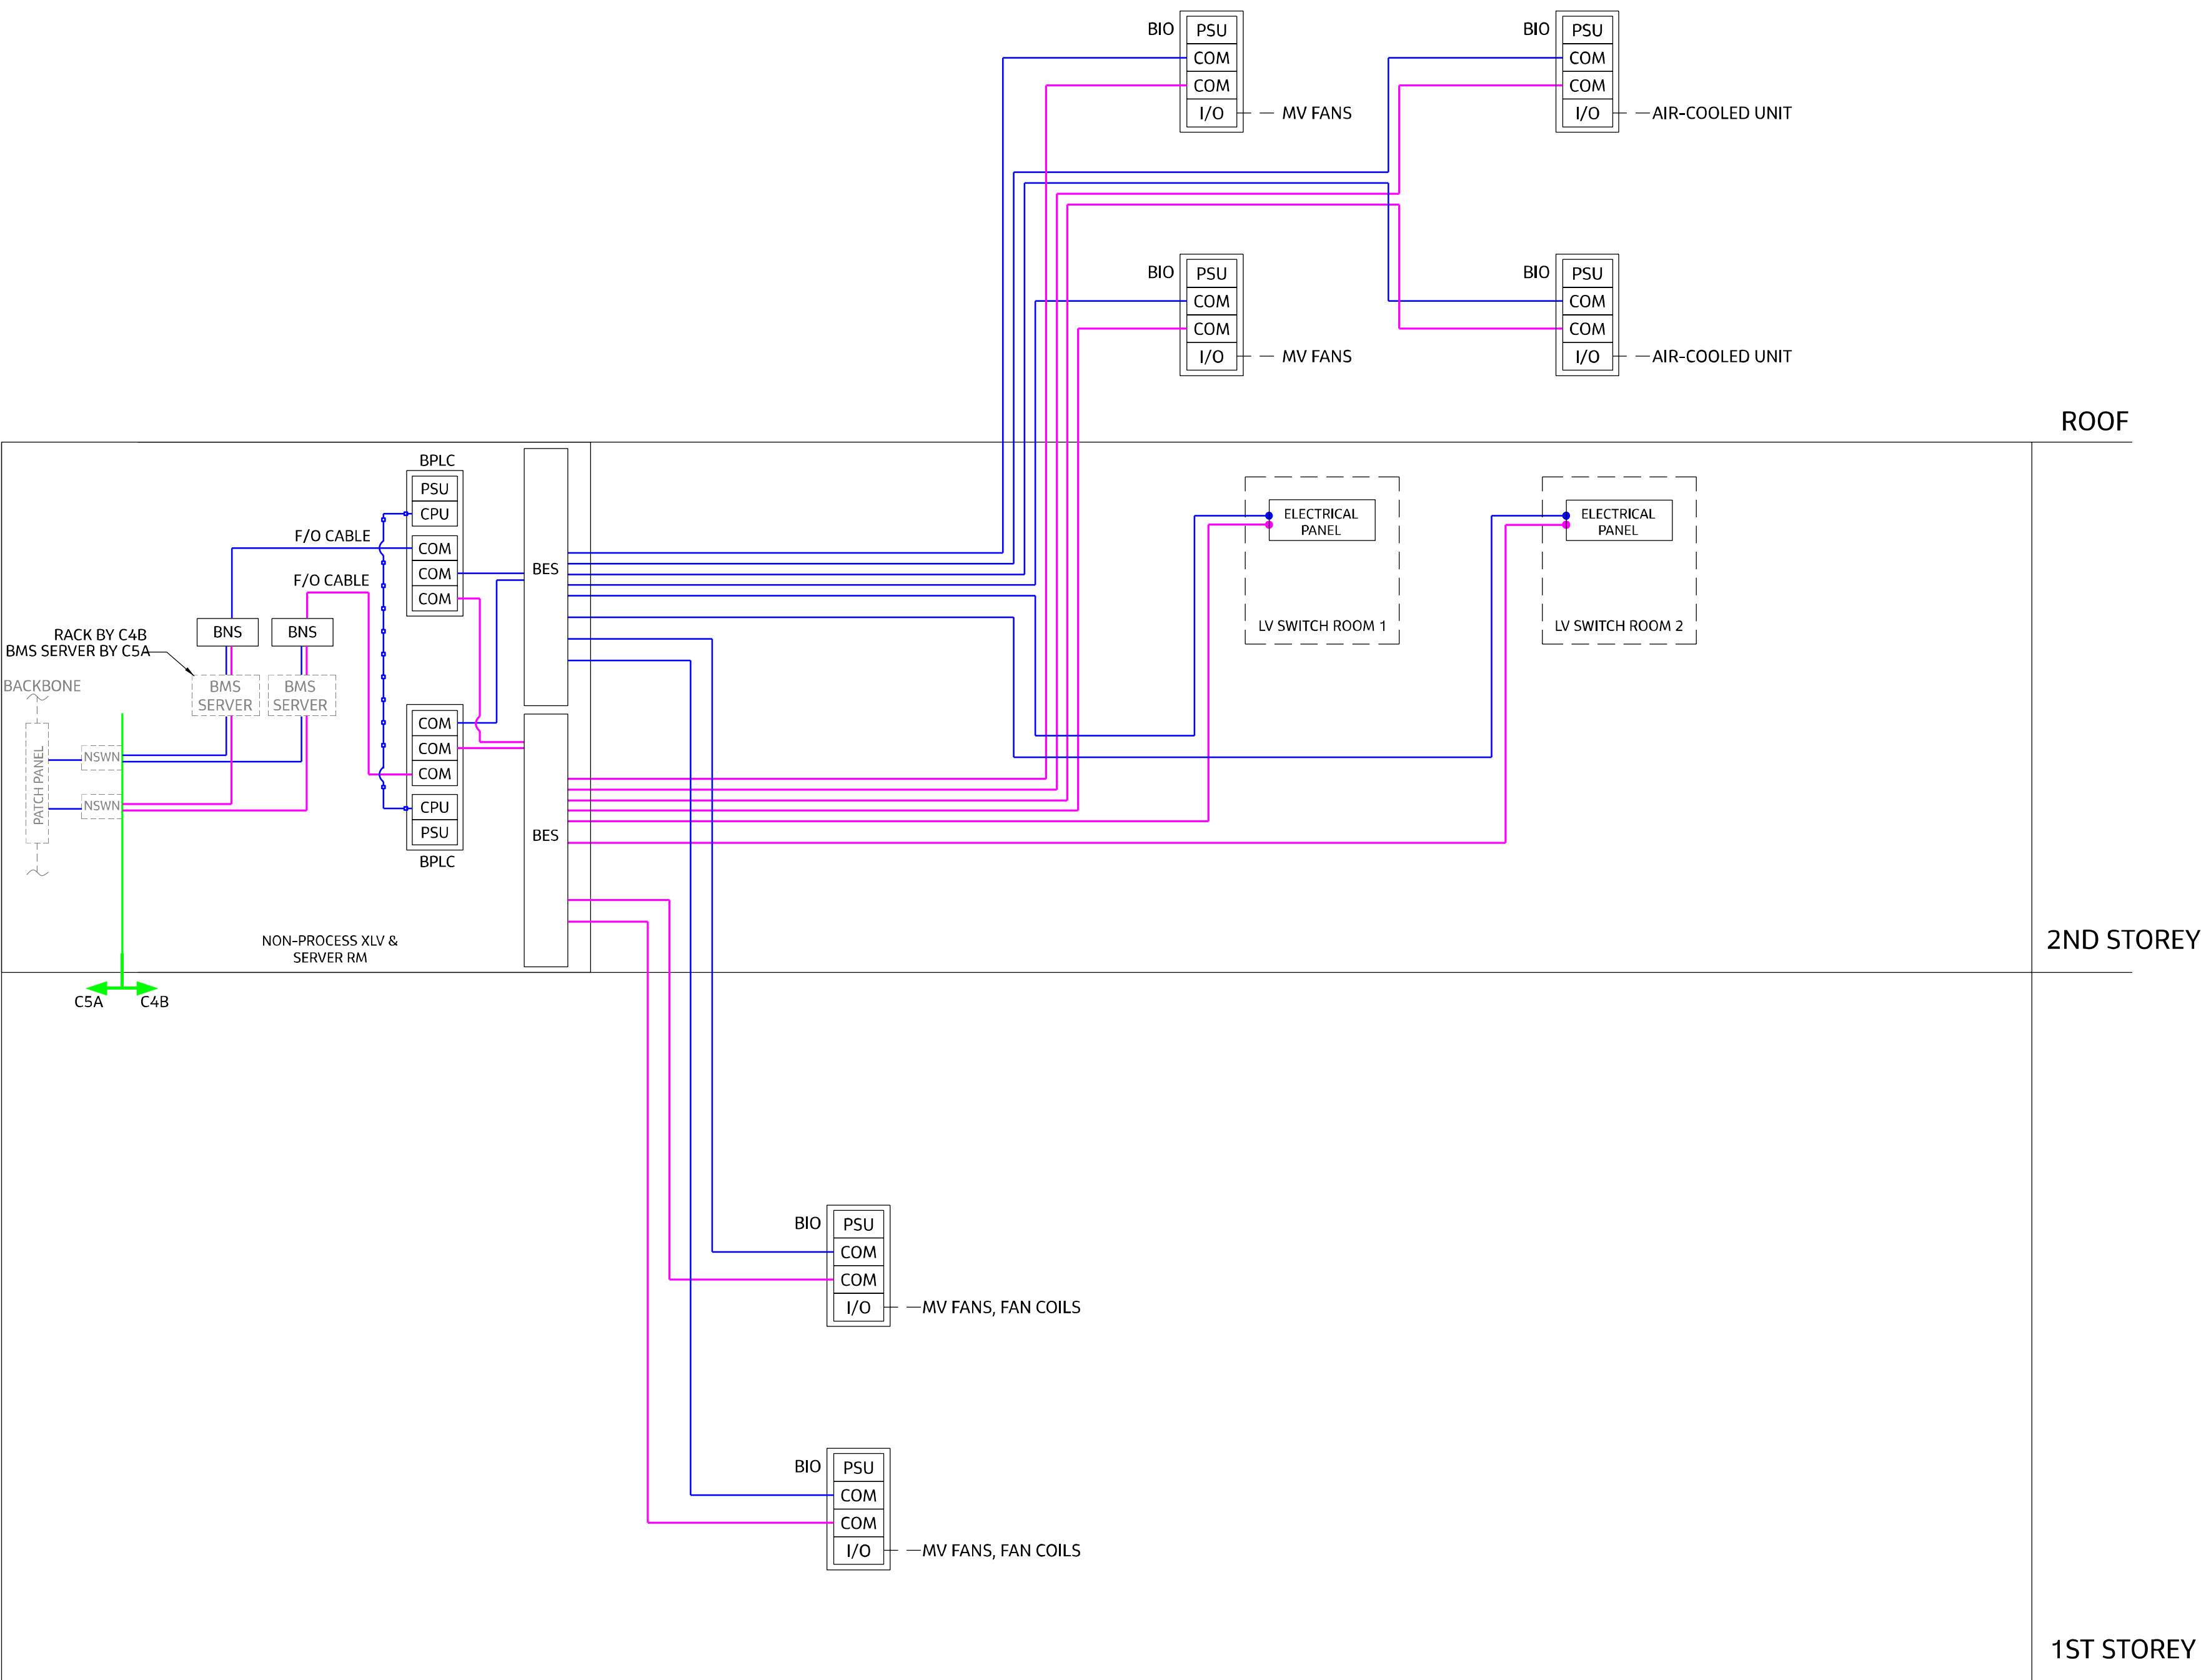

NOTE:-

1. QUANTITIES, LOCATION, NUMBER OF STOREY SHOWN ARE FOR INDICATIVE PURPOSES ONLY.
2. THE SCHEMATIC IS INDICATIVE AND THE CONTRACTOR SHALL BE RESPONSIBLE FOR CONFIRMING THE FINAL QUANTITIES AND CONFIGURATION WITH THE S.O. PRIOR INSTALLATION.
3. THE CONTRACTOR SHALL BE RESPONSIBLE FOR PROVIDING DESIGN DETAILS TO THE S.O. FOR APPROVAL PRIOR TO INSTALLATION.

LEGEND

- CAT 6 CABLES
- CAT 6 CABLES
- FIBRE-OPTIC CABLES
- FIBRE-OPTIC CABLES
- - - - COPPER CONTROL CABLE

ABBREVIATIONS:

- BPC BMS PLANT CONTROLLER
- BPLC BMS PROGRAMMABLE LOGIC CONTROLLER
- BNS BMS NETWORK SWITCH
- BWS BMS WORKSTATION
- BES BMS EDGE SWITCH
- FCU FAN COIL UNIT
- MCC MOTOR CONTROL CENTRE
- NSWN NETWORK SWITCH (MAIN BACKBONE-NON PROCESS)
- BIO INPUT / OUTPUT MODULES
- PSU POWER SUPPLY UNIT
- CPU CENTRAL PROCESSING UNIT

TENDER

T1	20/05/22	ISSUED FOR TENDER	HKT	HKT
REV	DATE	DESCRIPTION	REVIEWED	AUTHORISED



PROJECT TITLE:
TUAS WATER RECLAMATION PLANT (TWRP)
DTSS PHASE 2

DRAWING TITLE:
SIDESTREAM NITROGEN REMOVAL
(WST02) SCHEMATIC FOR BMS

DRAFTED: EZ	DESIGNED: EZ	SHEET SIZE: A1
DRAFTING CHECK: HKT	DESIGN CHECK: HKT	SCALE: NTS
DATE: 21/03/22	REVIEWED: HKT	PBS: 131101

CONTRACT: C4B	DRAWING NUMBER: PUB-DTSS2-TWRP WST02-B-7301	REVISION: T1
------------------	---	-----------------

THIS DRAWING IS COPYRIGHT