


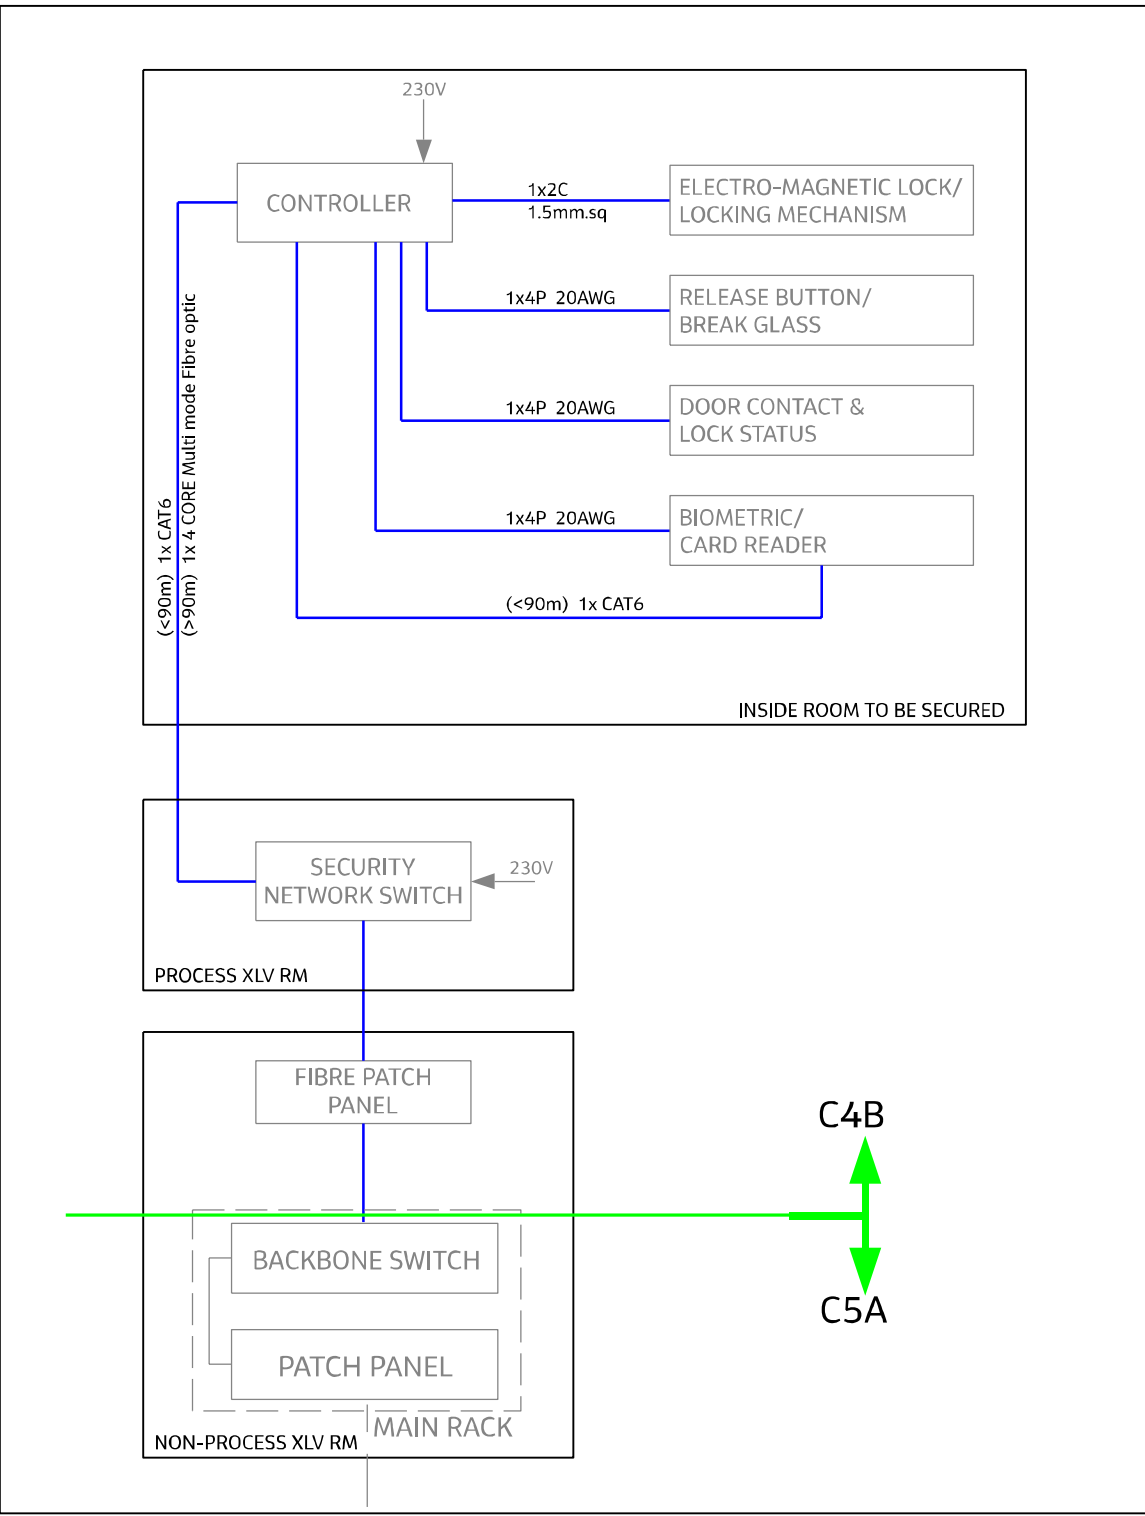

ISMS BACKBONE (SECURITY NETWORK)

LEGEND:-
SCOPE OF WORKS FOR C4B

TENDER

T1	20/05/22	ISSUED FOR TENDER	HKT	HKT
REV	DATE	DESCRIPTION	REVIEWED	AUTHORISED

CLIENT:



SINGAPORE'S
NATIONAL
WATER AGENCY

PROGRAMME MANAGER:



A JOINT VENTURE DELIVERING THE DTSS2 PROJECT

CONSULTANT:



CH2M HILL Singapore Pte Ltd

PROJECT TITLE:

TUAS WATER RECLAMATION PLANT (TWRP)
DTSS PHASE 2

DRAWING TITLE:

SIDESTREAM NITROGEN REMOVAL (WST02)
SCHEMATIC FOR DOOR ACCESS CABLING

DRAFTED: EZ	DESIGNED: EZ	SHEET SIZE: A1
DRAFTING CHECK: HKT	DESIGN CHECK: HKT	SCALE: NTS
DATE: 06/03/20	REVIEWED: HKT	PBS: 131101

CONTRACT:	DRAWING NUMBER:
C4B	PUB-DTSS2-TWRP
SHEET NUMBER:	REVISION:
WST02-B-7503	T1

THIS DRAWING IS COPYRIGHT