


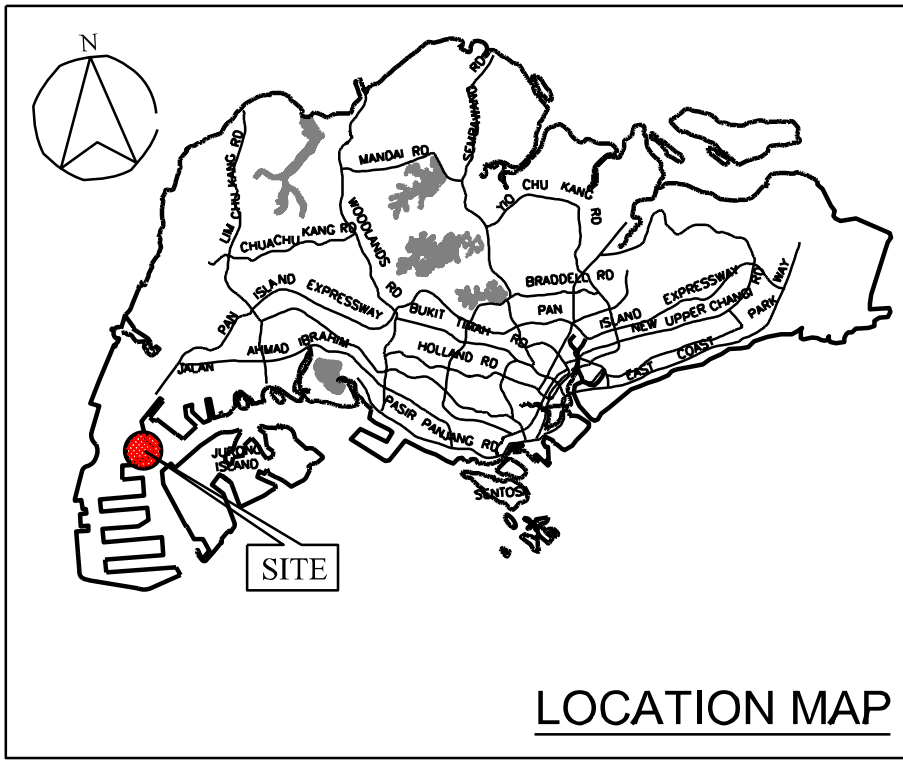


LEGEND :


- DUCT BANKS FOR SITE WIDE 22KV DISTRIBUTION
- ELECTRICAL MANHOLES

NOTES:

1. THIS DRAWING SHALL NOT BE SCALED FROM.
2. DUCT BANK ROUTING & MANHOLE LOCATIONS ARE INDICATIVE ONLY.
3. BUILDING OUTLINES AND FACILITY LOCATIONS ARE SHOWN FOR REFERENCE ONLY.
4. THE CONTRACTOR SHALL PROVIDE DUCTBANK AND MANHOLE FROM TIE IN POINT WST02-TP-E-0001 TO WST02.

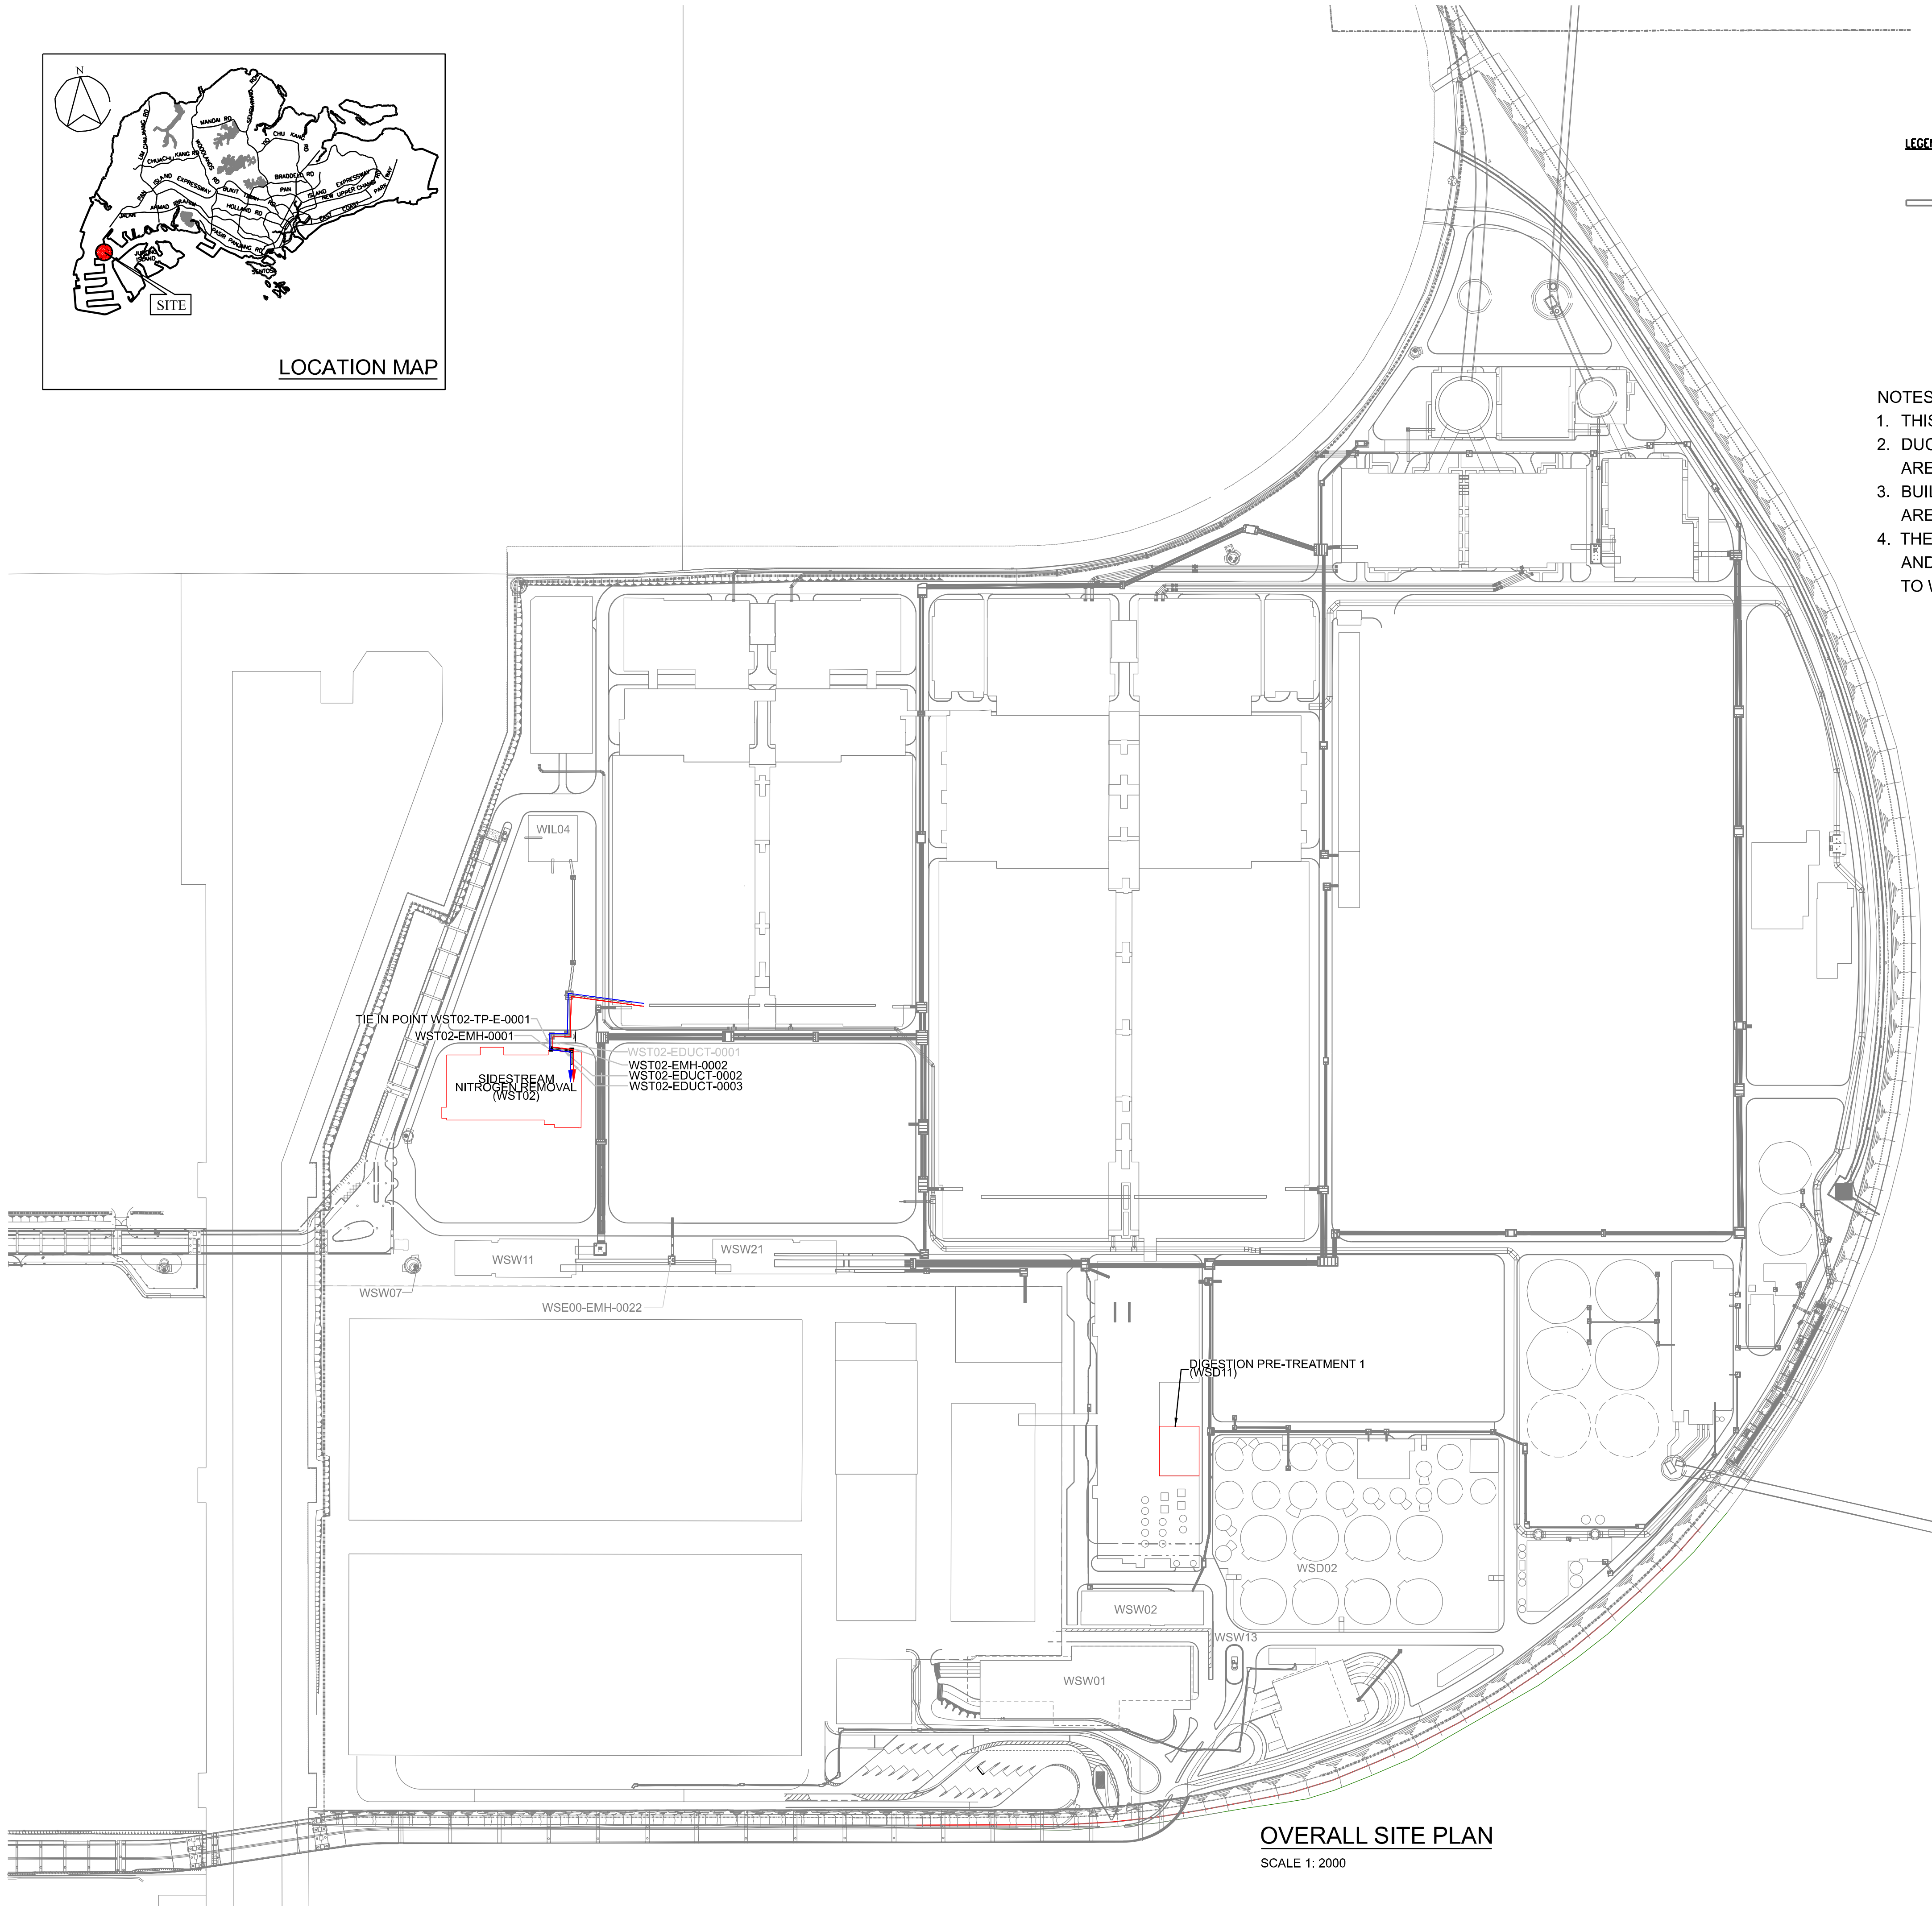

OVERALL SITE PLAN
SCALE 1: 2000

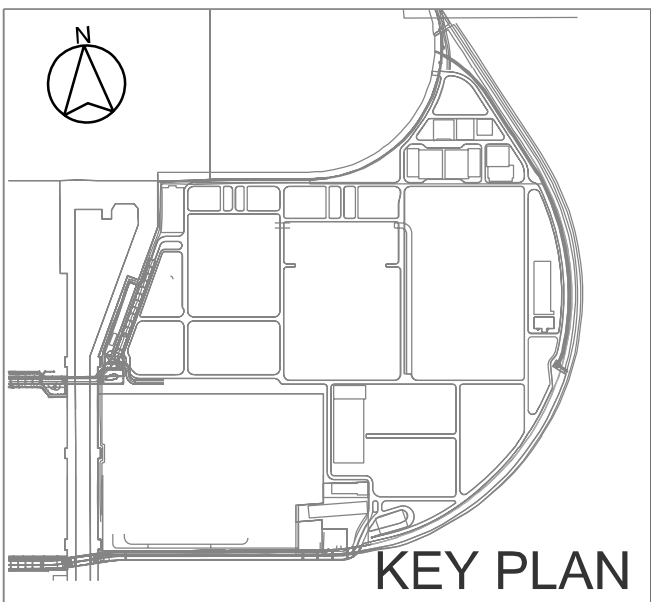

TENDER

T1	20/05/22	ISSUED FOR TENDER	LBL	LF
REV	DATE	DESCRIPTION	REVIEWED	AUTHORISED

CLIENT:



PROGRAMME MANAGER:



CONSULTANT:



PROJECT TITLE:

TUAS WATER RECLAMATION PLANT (TWRP)
DTSS PHASE 2

DRAWING TITLE

DUCTBANKS AND MANHOLES

DRAFTED: GGX/CHL	DESIGNED: GGX/CHL	SHEET SIZE: A1
DRAFTING CHECK: GGX/CHL	DESIGN CHECK: LBL	SCALE: NA
DATE: 20/05/22	REVIEWED: LBL	PBS: 131101
CONTRACT: C4B	DRAWING NUMBER: PUB-DTSS2-TWRP WSW41-E-1003	REVISION: T1

THIS DRAWING IS COPYRIGHT