


WSB01 (BIOSOLIDS BUILDING)




ITEM	TAG
E	WSD11-ECCP-1000 (HOT-STANDBY MASTER PLCs FOR THP)
N	WSD11-FOIP-0001

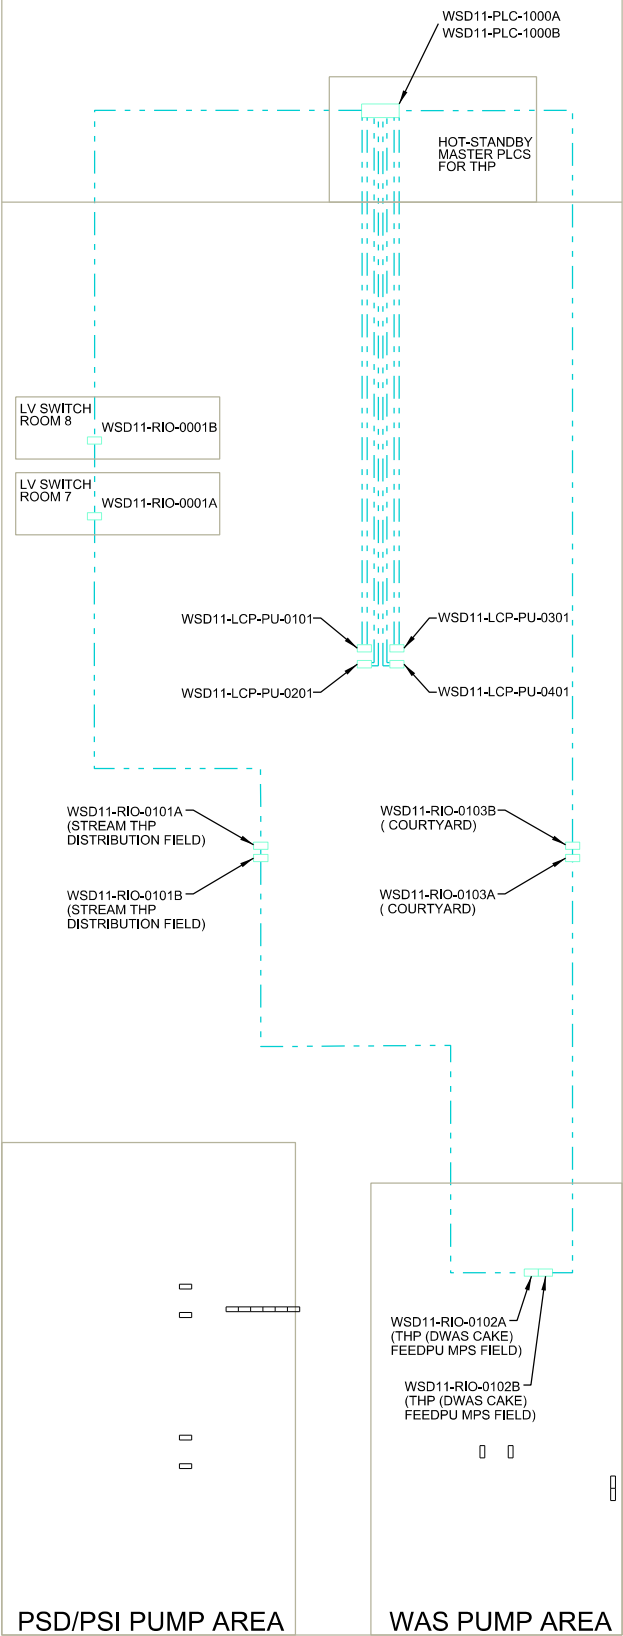

BIOSOLIDS BUILDING PROCESS XLV ROOM

DETAIL-A

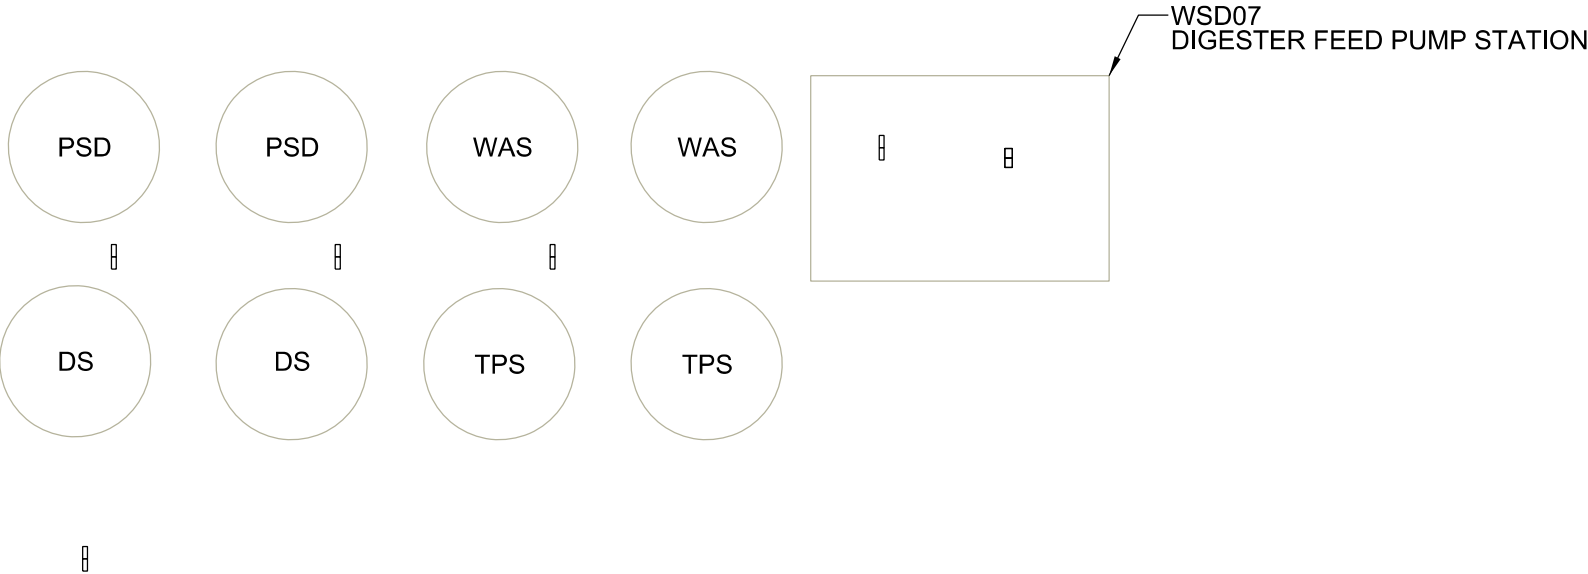

CABLE LEGEND:

- SINGLE-MODE F/O CABLES
- MULTI-MODE F/O CABLES

- NOTES:
- THIS DRAWING IS NOT DRAWN TO SCALE.
 - THIS DRAWING IS INTENDED TO SHOW INDICATIVE ICA PANELS LOCATIONS. REFER TO BIM MODEL FOR INDICATIVE SETOUT LOCATION COORDINATES.
 - THIS DRAWING SHOWS INDICATIVE CABLE ROUTING. REFER TO BIM MODEL FOR INDICATIVE SERVICE SPACE.
 - FOR DETAIL INFORMATION SEE CONTROL NETWORK DIAGRAMS: - WSD11-4-7001 TO 7004

TENDER

T1	20/05/22	ISSUED FOR TENDER C4B	JL	GOT
REV	DATE	DESCRIPTION	REVIEWED	AUTHORISED



PROJECT TITLE:
TUAS WATER RECLAMATION PLANT (TWRP)
DTSS PHASE 2

DRAWING TITLE:
BIOSOLIDS BUILDING
THP GENERAL RING PLAN

DRAFTED: PA	DESIGNED: SK	SHEET SIZE: A1
DRAFTING CHECK: RS	DESIGN CHECK: AT	SCALE: NA
DATE: 20/05/22	REVIEWED: JL	PBS: 131101
CONTRACT: C4B	DRAWING NUMBER: PUB-DTSS2-TWRP	REVISION: T1

THIS DRAWING IS COPYRIGHT