
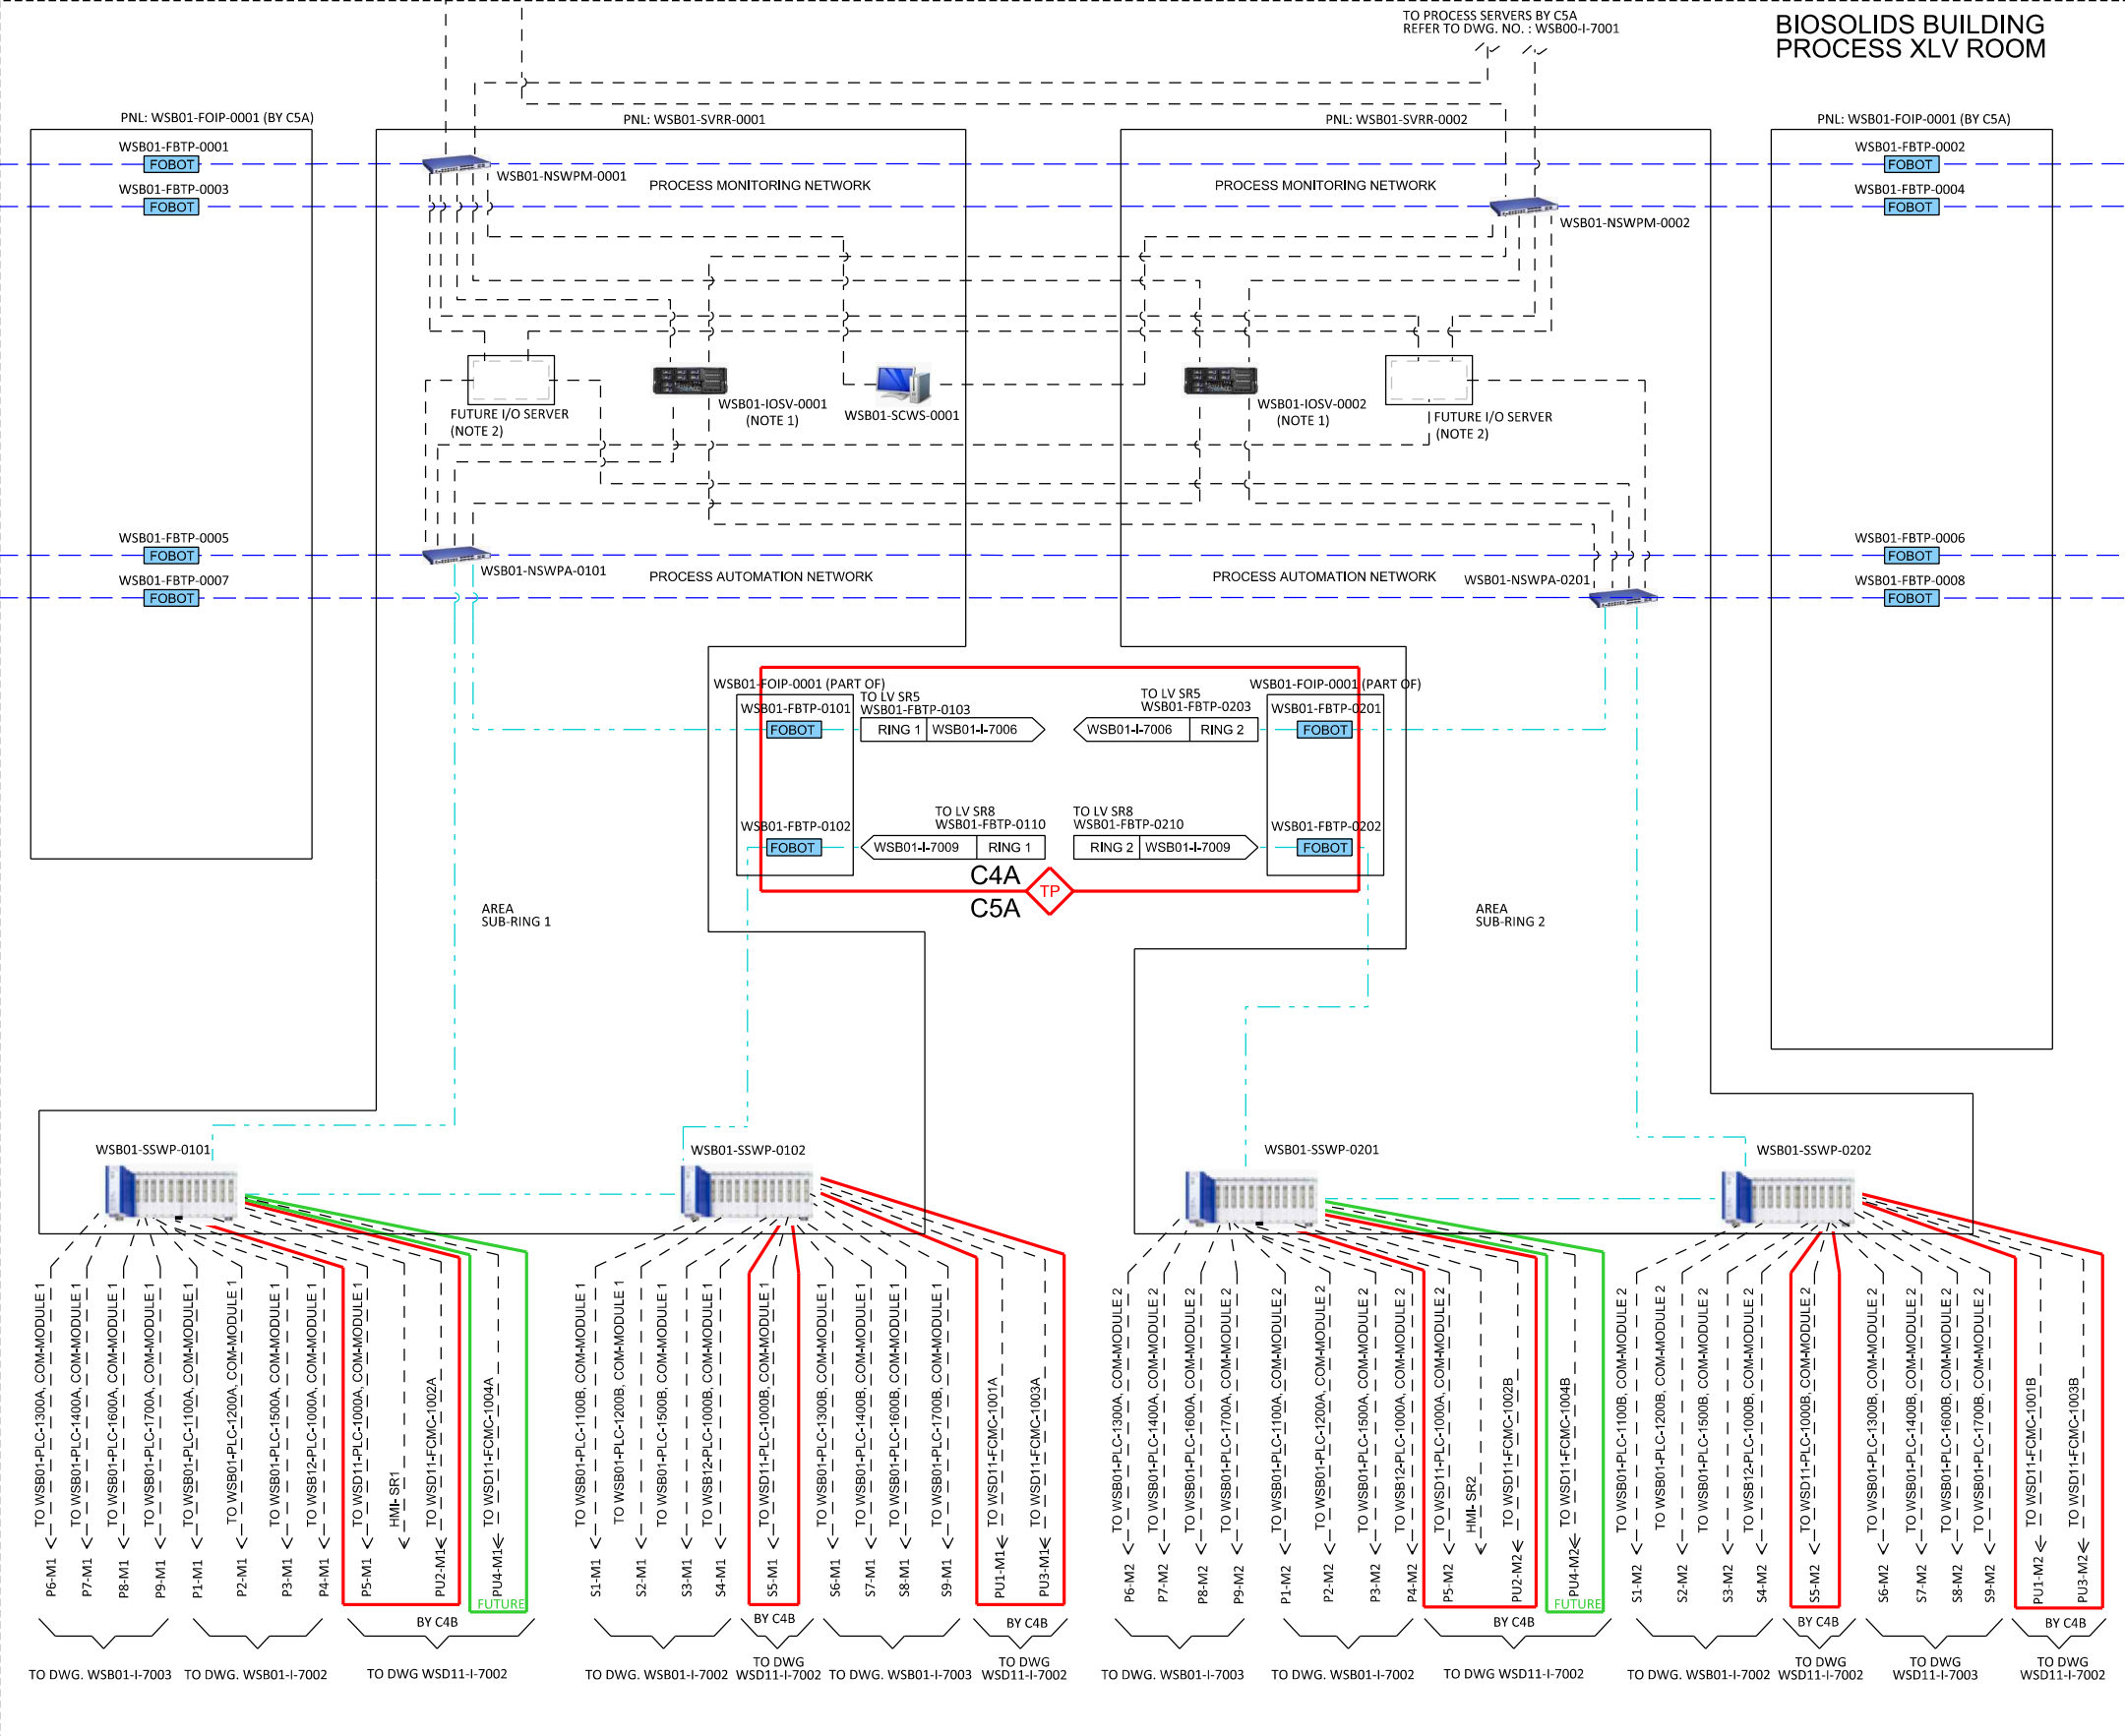


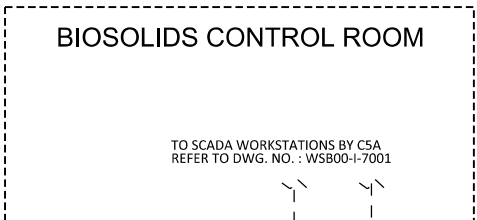

CABLE LEGEND:

----- SINGLE-MODE F/O CABLES

----- MULTI-MODE F/O CABLES

NOTES:

1. I/O SERVER IS FOR ENTIRE WSB01. I/O SERVERS SHALL BE PROVIDED WITH SHARED MONITOR, KEYBOARD AND KVM SWITCH (BY C5A, NOT SHOWN).

2. I/O SERVERS FOR FUTURE

REFERENCES:

GENERAL NOTES: 131101-WSW00-I-0010

LEGEND : 131101-WSW00-I-0011

TENDER

REV	DATE	DESCRIPTION	REVIEWED	AUTHORISED
T1	20/05/22	ISSUED FOR TENDER C4B	JL	GOT

CLIENT:

PUB SINGAPORE'S NATIONAL WATER AGENCY

PROGRAMME MANAGER:

bmies AECOM
A JOINT VENTURE DELIVERING THE DTSS2 PROJECT

CONSULTANT:

Jacobs
CH2M HILL Singapore Pte Ltd

PROJECT TITLE:

**TUAS WATER RECLAMATION PLANT (TWRP)
DTSS PHASE 2**

DRAWING TITLE:

**CONTROL NETWORK DIAGRAM
BIOSOLIDS BUILDING
PROCESS XLV ROOM
PART-1**

DRAFTED:	DESIGNED:	SHEET SIZE:
PA	SK	A1
DRAFTING CHECK:	DESIGN CHECK:	SCALE:
RS	AT	NTS
DATE:	REVIEWED:	PBS:
20/05/22	JL	131101
CONTRACT:	DRAWING NUMBER:	SHEET NUMBER:
C4B	PUB-DTSS2-TWRP	WSD11-I-7001
		REVISION:
		T1

THIS DRAWING IS COPYRIGHT