



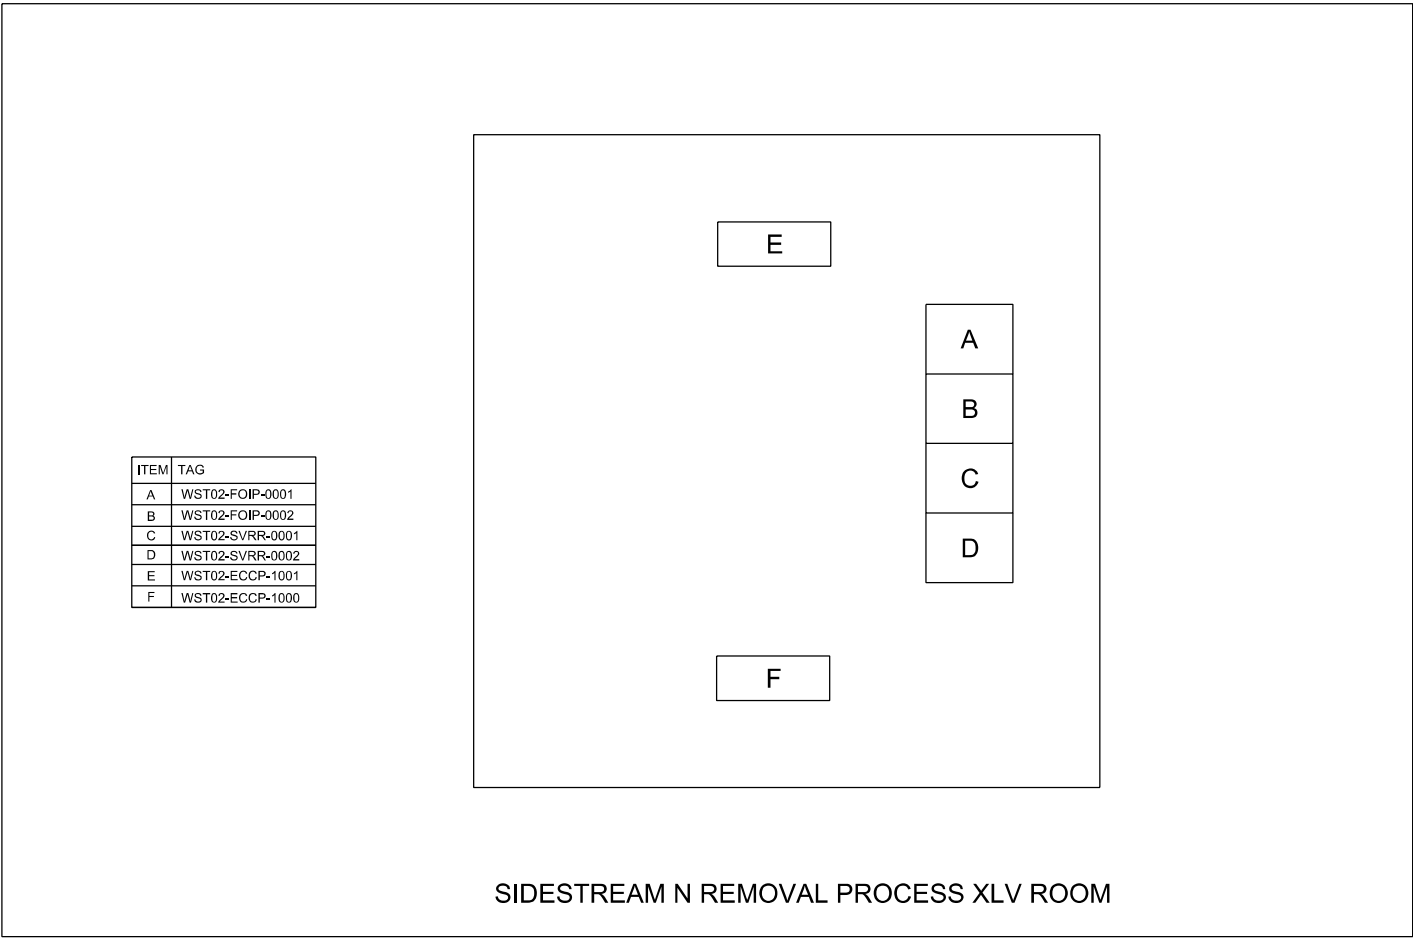

DETAIL-A

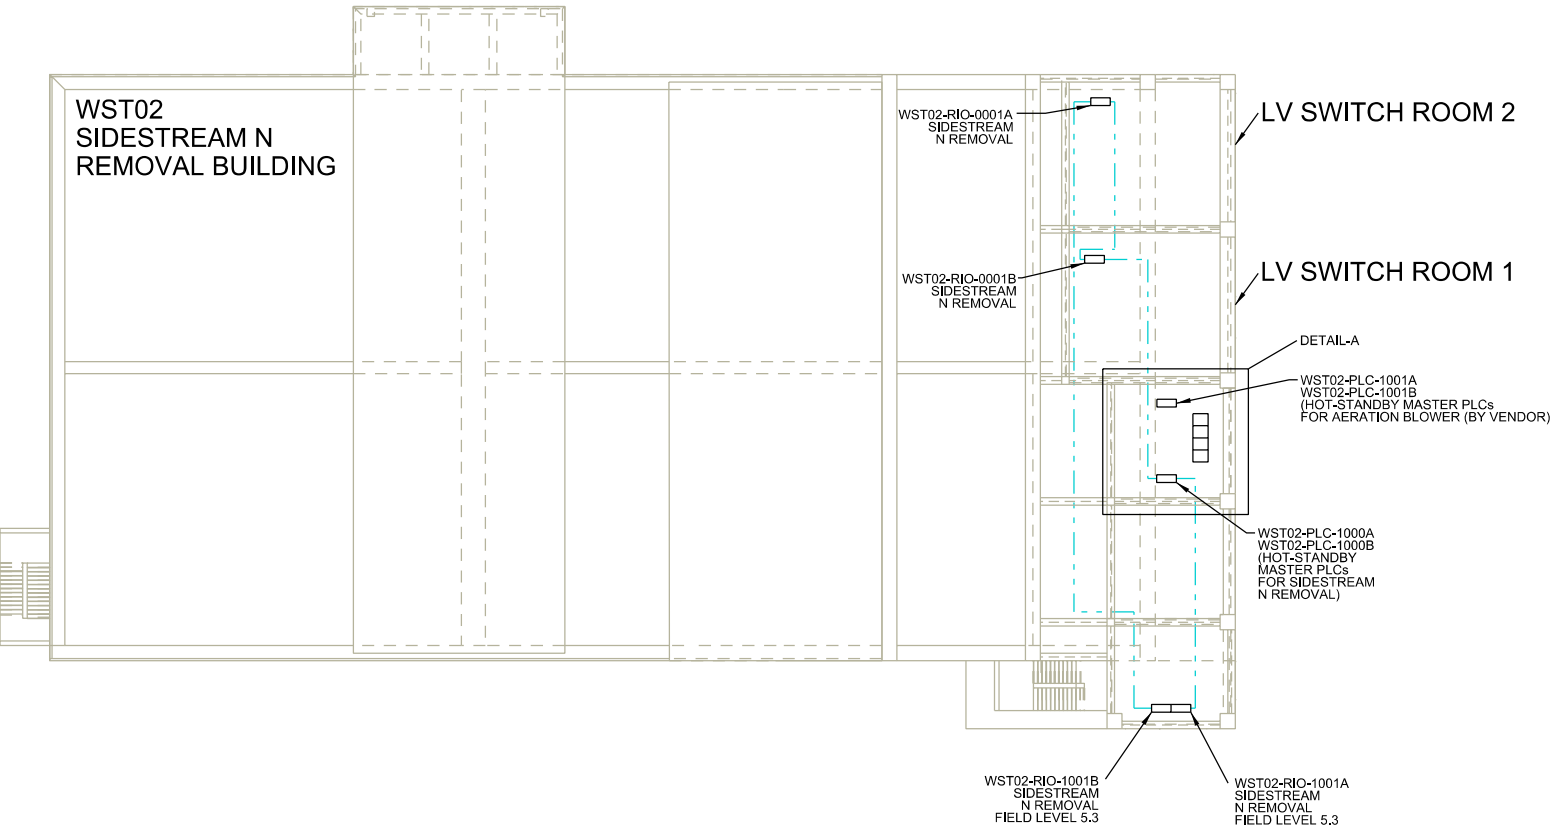

- CABLE LEGEND:
- SINGLE-MODE F/O CABLES
 - MULTI-MODE F/O CABLES
- NOTES:
- THIS DRAWING IS NOT DRAWN TO SCALE.
 - THIS DRAWING IS INTENDED TO SHOW INDICATIVE ICA PANELS LOCATIONS. REFER TO BIM MODEL FOR INDICATIVE SETOUT LOCATION COORDINATES.
 - THIS DRAWING SHOWS INDICATIVE CABLE ROUTING. REFER TO BIM MODEL FOR INDICATIVE SERVICE SPACE.
 - FOR DETAIL INFORMATION SEE CONTROL NETWORK DIAGRAMS:
 - WST02-I-7001
 - WST02-I-7010

TENDER

T1	20/05/22	ISSUED FOR TENDER C4B	JL	GOT
REV	DATE	DESCRIPTION	REVIEWED	AUTHORISED

CLIENT:



SINGAPORE'S
NATIONAL
WATER AGENCY

PROGRAMME MANAGER:



A JOINT VENTURE DELIVERING THE DTSS2 PROJECT

CONSULTANT:



CH2M HILL Singapore Pte Ltd

PROJECT TITLE:

TUAS WATER RECLAMATION PLANT (TWRP)
DTSS PHASE 2

DRAWING TITLE

SIDESTREAM N REMOVAL-
RING PLAN

DRAFTED: PA	DESIGNED: SK	SHEET SIZE: A1
DRAFTING CHECK: RS	DESIGN CHECK: AT	SCALE: NA
DATE: 20/05/22	REVIEWED: JL	PBS: 131101
CONTRACT: C4B	DRAWING NUMBER: PUB-DTSS2-TWRP	REVISION: T1
THIS DRAWING IS COPYRIGHT		