


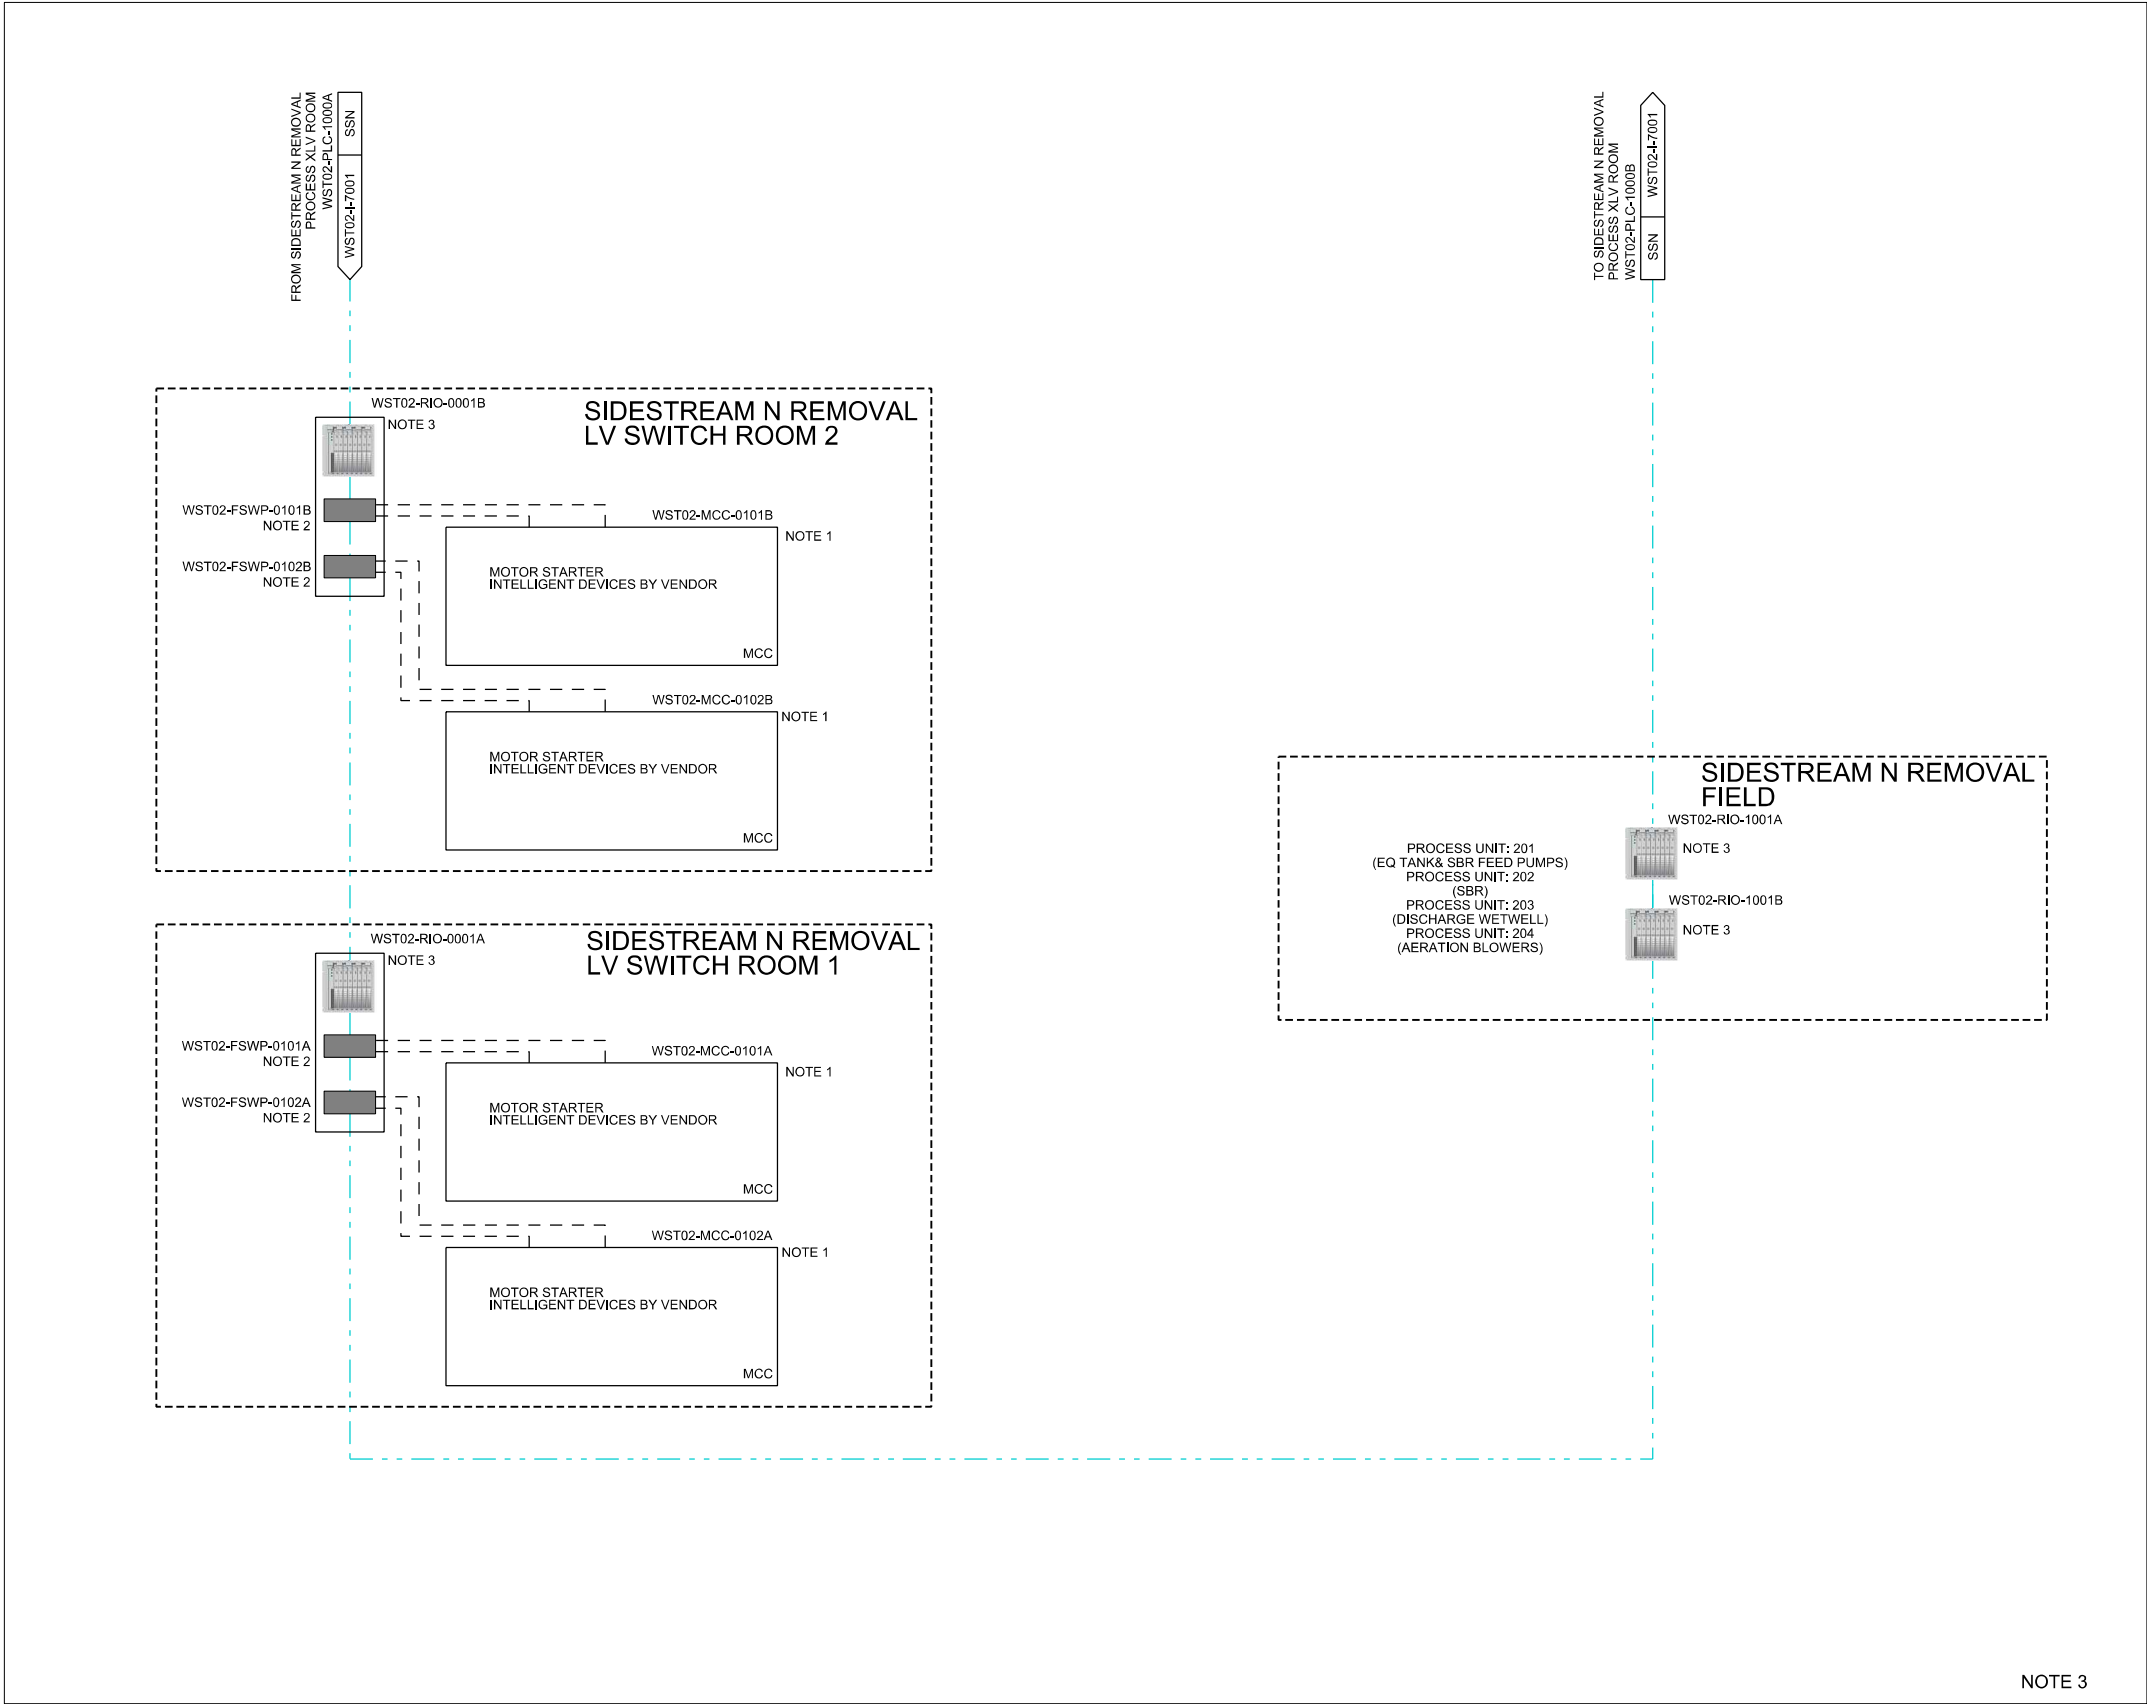

NOTE 3

CABLE LEGEND:

----- MULTI-MODE F/O CABLES

NOTES:

1. QUANTITY OF INTELLIGENT DEVICES BY MCC VENDOR AND INTERNAL MCC NETWORK TOPOLOGY DEPEND ON SELECTED MCC VENDOR BY THIS CONTRACTOR.
2. IF REQUIRED IN THE VENDOR DESIGN, FIELD ETHERNET SWITCH SHALL BE MIN. OF 16 PORT INDUSTRIAL SWITCH.
3. THE FILED CONTROL NETWORK SHOWN IN THIS SCHEMATIC IS A NOTIONAL DESIGN AND THE QUANTITY OF RIO IS INDICATIVE ONLY. THE CONTRACTOR SHALL PROVIDE FIELD NETWORK AND FIELD PANELS (RIO PANELS) THAT COMPLY WITH THE DESIGN AND BUILD REQUIREMENTS FOR A FULLY FUNCTIONING COMPLETE SYSTEM.

REFERENCES:

GENERAL NOTES: 131101-WSW00-I-0010

LEGEND : 131101-WSW00-I-0011

TENDER

|     |          |                       |          |            |
|-----|----------|-----------------------|----------|------------|
|     |          |                       |          |            |
|     |          |                       |          |            |
| T1  | 20/05/22 | ISSUED FOR TENDER C4B | JL       | GOT        |
| REV | DATE     | DESCRIPTION           | REVIEWED | AUTHORISED |

CLIENT:



PROGRAMME MANAGER:



CONSULTANT:



PROJECT TITLE:

TUAS WATER RECLAMATION PLANT (TWRP)  
DTSS PHASE 2

DRAWING TITLE

CONTROL NETWORK DIAGRAM  
SIDESTREAM N REMOVAL  
FIELD & MCC

|                       |                     |                   |
|-----------------------|---------------------|-------------------|
| DRAFTED:<br>PA        | DESIGNED:<br>SK     | SHEET SIZE:<br>A1 |
| DRAFTING CHECK:<br>RS | DESIGN CHECK:<br>AT | SCALE:<br>NTS     |
| DATE:<br>20/05/22     | REVIEWED:<br>JL     | PBS:<br>131101    |

|                  |                                   |                 |
|------------------|-----------------------------------|-----------------|
| CONTRACT:<br>C4B | DRAWING NUMBER:<br>PUB-DTSS2-TWRP | REVISION:<br>T1 |
|                  | SHEET NUMBER:<br>WST02-I-7010     |                 |

THIS DRAWING IS COPYRIGHT