


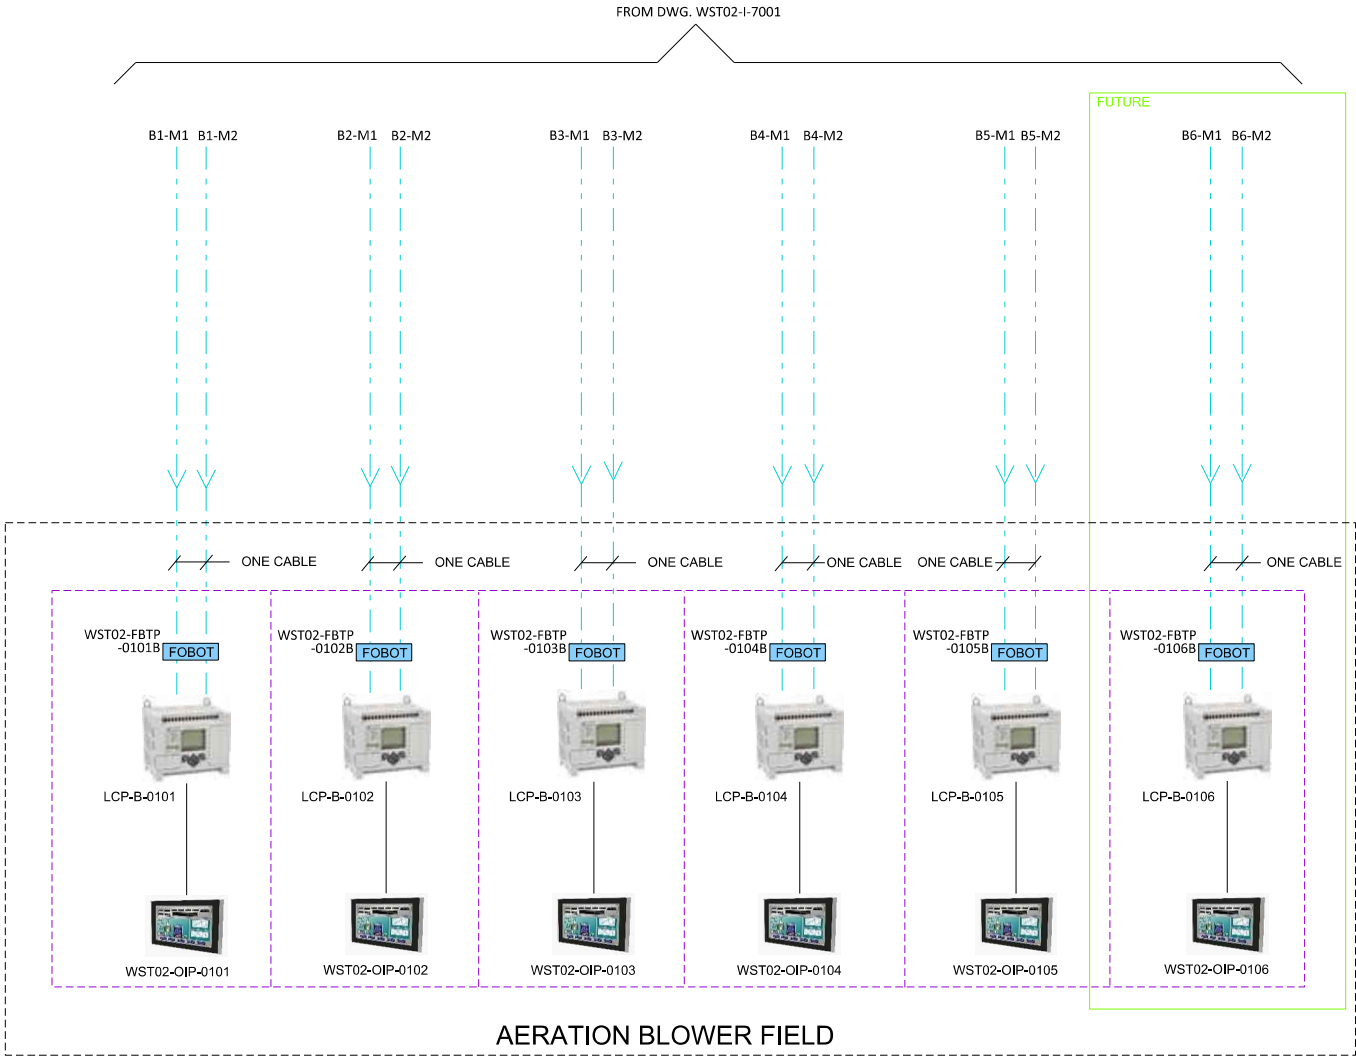

CABLE LEGEND:

----- MULTIMODE F/O CABLES

REFERENCES:
GENERAL NOTES: 131101-WSW004-0010
LEGEND : 131101-WSW004-0011

TENDER

T1	20/05/22	ISSUED FOR TENDER C4B	JL	GOT
REV	DATE	DESCRIPTION	REVIEWED	AUTHORISED

CLIENT:



PROGRAMME MANAGER:



CONSULTANT:



PROJECT TITLE:

TUAS WATER RECLAMATION PLANT (TWRP)
DTSS PHASE 2

DRAWING TITLE

CONTROL NETWORK DIAGRAM
AERATION BLOWER FIELD

DRAFTED: PA	DESIGNED: SK	SHEET SIZE: A1
DRAFTING CHECK: RS	DESIGN CHECK: AT	SCALE: NTS
DATE: 20/05/22	REVIEWED: JL	PBS: 131101
CONTRACT: C4B	DRAWING NUMBER: PUB-DTSS2-TWRP	REVISION: T1

THIS DRAWING IS COPYRIGHT