


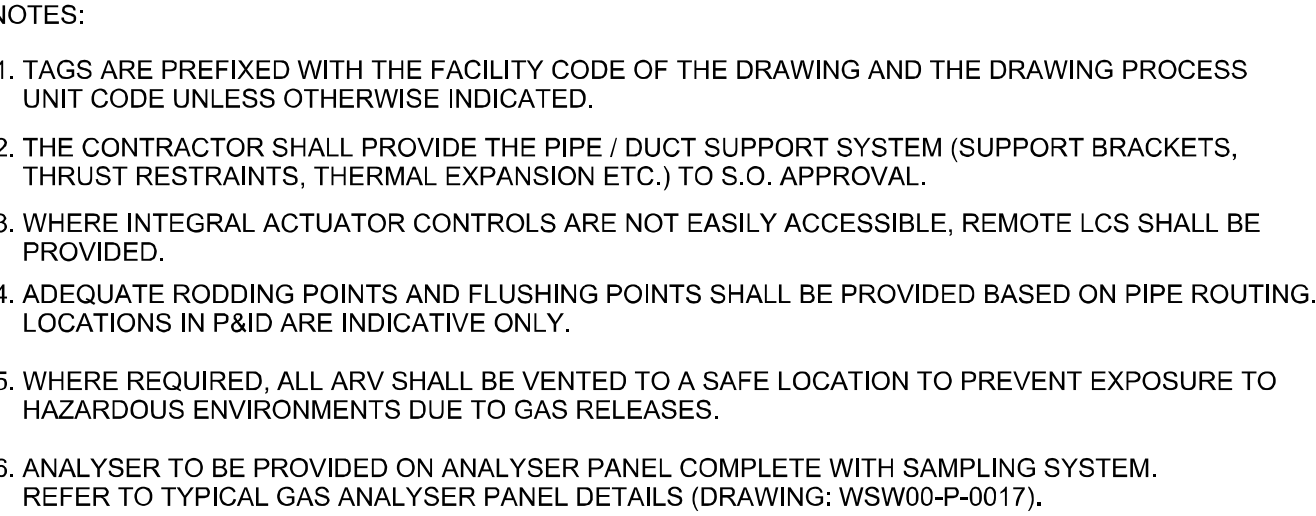

PROGRAMME MANAGER:

 **binnies** **AECOM**

A JOINT VENTURE DELIVERING THE DTSS2 PROJECT

CONSULTANT:

Jacobs

CH2M HILL Singapore Pte Ltd

PROJECT TITLE:

TUAS WATER RECLAMATION PLANT (TWRP)
DTSS PHASE 2

P&ID
GRIT TANKS 5 & 6

DRAFTED: ML	DESIGNED: SYC	SHEET SIZE: A1	
DRAFTING CHECK: DW	DESIGN CHECK: DT	SCALE: NTS	
DATE: 16/11/17	REVIEWED: CN	PBS:	131101
CONTRACT:	DRAWING NUMBER: PUB-DTSS2-TWRP		
-	SHEET NUMBER: WIL11-P-6008		REVISION: T1
THIS DRAWING IS COPYRIGHT			