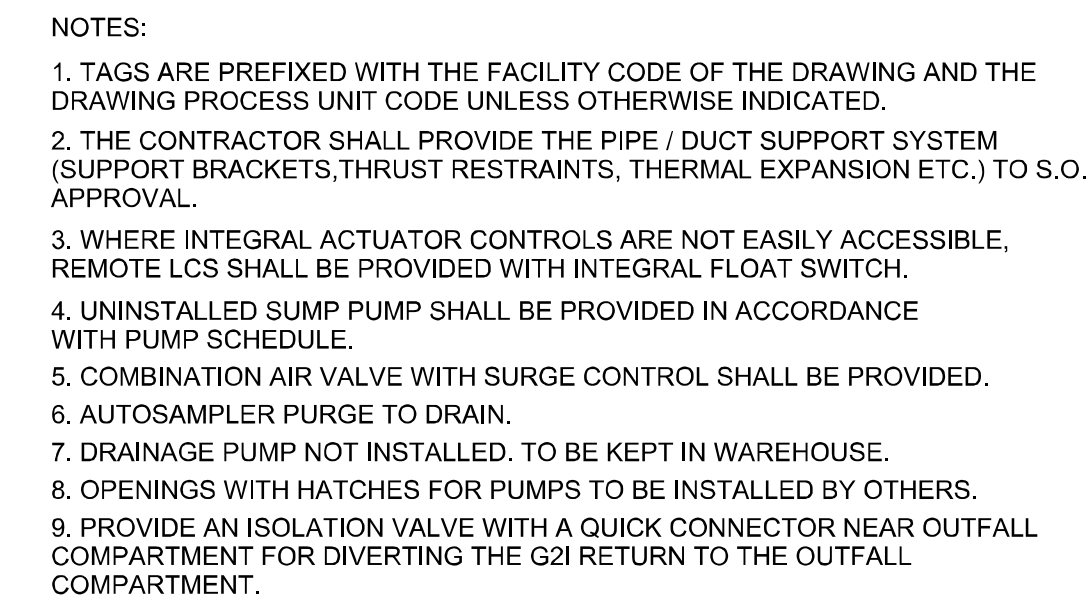


T1	20/05/22	ISSUED FOR TENDER C4B		CN	GOT
T1	17/07/20	ISSUED FOR TENDER C3B1		CN	GOT
T1	24/04/20	ISSUED FOR TENDER C3A		CN	GOT
REV	DATE	DESCRIPTION		REVIEWED	AUTHORISED

PROGRAMME MANAGER:

 **binnies AECOM**

A JOINT VENTURE DELIVERING THE DTSS2 PROJECT

PROJECT TITLE:

TUAS WATER RECLAMATION PLANT (TWRP)
DTSS PHASE 2

DRAWING TITLE

P&ID
MBR FILTRATE TANK
AND TRANSFER PUMPS
PART 2

DRAFTED: JMJ	DESIGNED: KT	SHEET SIZE: A1
DRAFTING CHECK: DW	DESIGN CHECK: RM	SCALE: NTS
DATE: 06/12/17	REVIEWED: CN	PBS: 131101
CONTRACT:	DRAWING NUMBER: PUB-DTSS2-TWRP	
-	SHEET NUMBER: WIL13-P-6080	REVISION: T1
THIS DRAWING IS COPYRIGHT		