


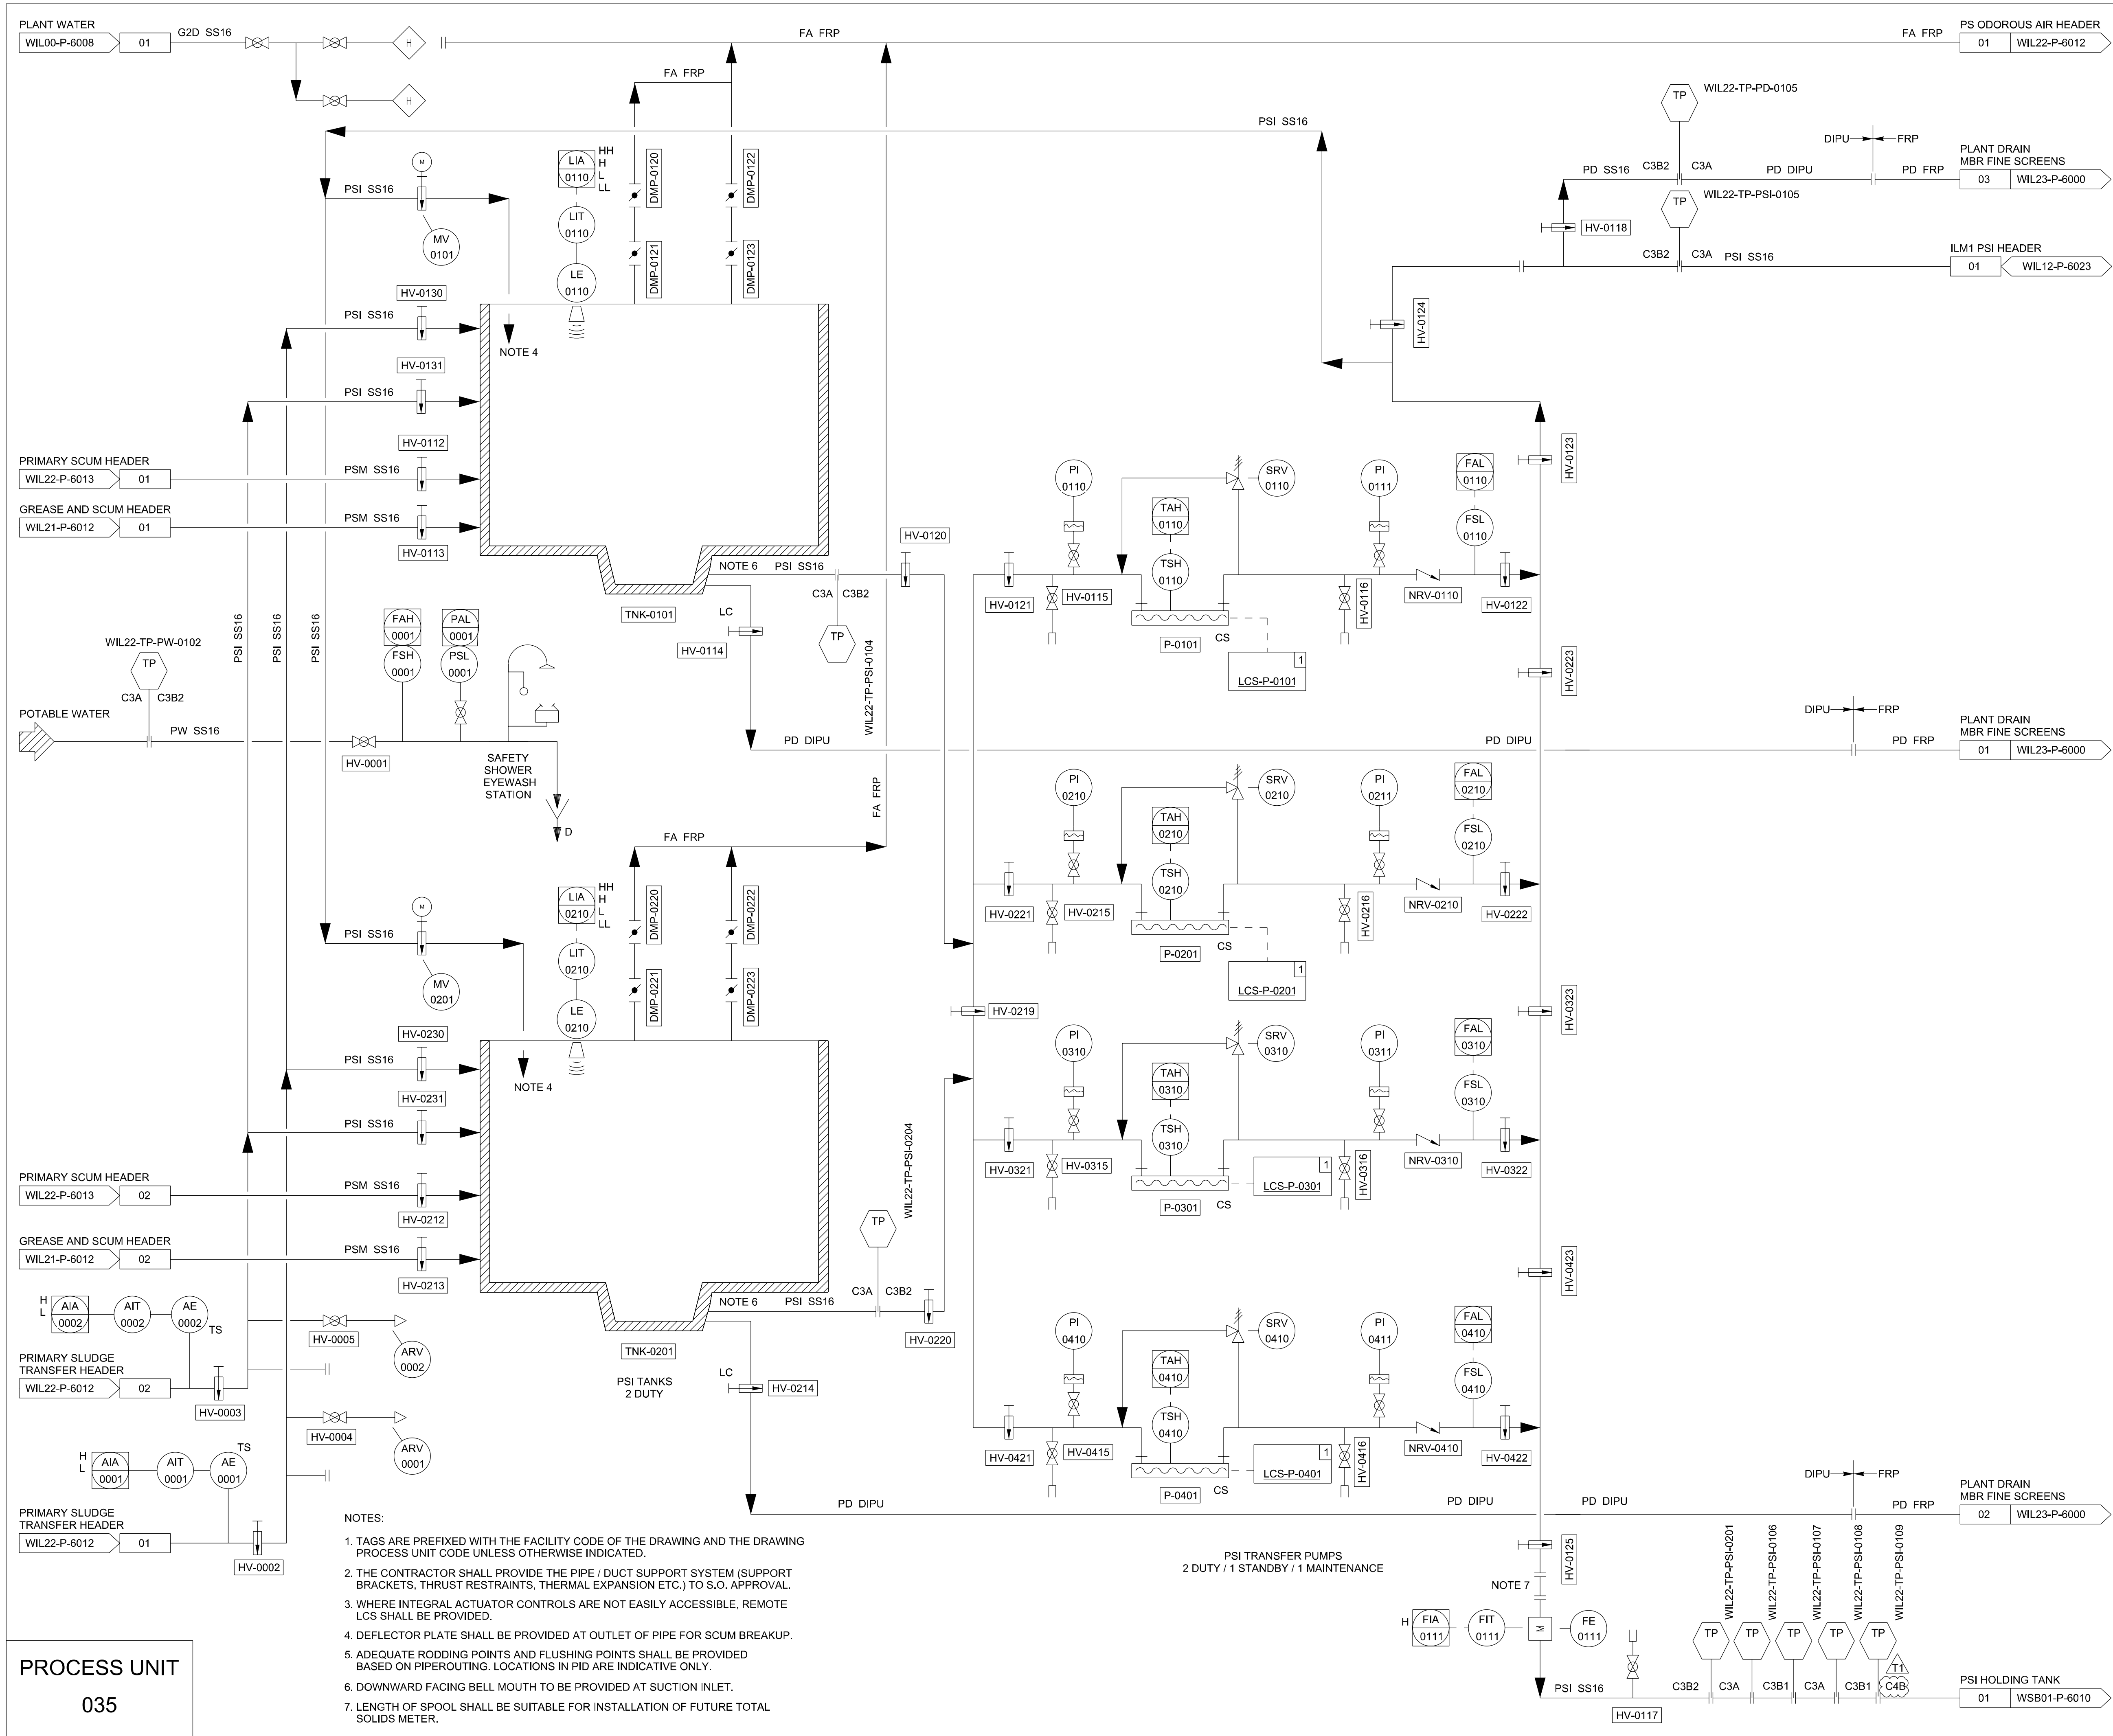

TENDER

T1	20/05/22	ISSUED FOR TENDER C4B	CN	GOT
T1	26/02/21	ISSUED FOR TENDER C3B1	CN	GOT
T1	24/04/20	ISSUED FOR TENDER C3A	CN	GOT
REV	DATE	DESCRIPTION	REVIEWED	AUTHORISED

CLIENT:

PUB

SINGAPORE'S NATIONAL WATER AGENCY

PROGRAMME MANAGER:

binnies AECOM

A JOINT VENTURE DELIVERING THE DTSS2 PROJECT

CONSULTANT:

Jacobs

CH2M HILL Singapore Pte Ltd

DRAWING TITLE:

TUAS WATER RECLAMATION PLANT (TWRP)
DTSS PHASE 2

DRAFTING TITLE:

P&ID
PSI TANKS
AND TRANSFER PUMPS

DRAFTED: JMJ	DESIGNED: SYC	SHEET SIZE: A1
DRAFTING CHECK: DW	DESIGN CHECK: DT	SCALE: NTS
DATE: 13/02/18	REVIEWED: CN	PBS: 131101
CONTRACT:		

DRAWING NUMBER:

PUB-DTSS2-TWRP

SHEET NUMBER:

WIL22-P-6023

REVISION:

T1

THIS DRAWING IS COPYRIGHT