


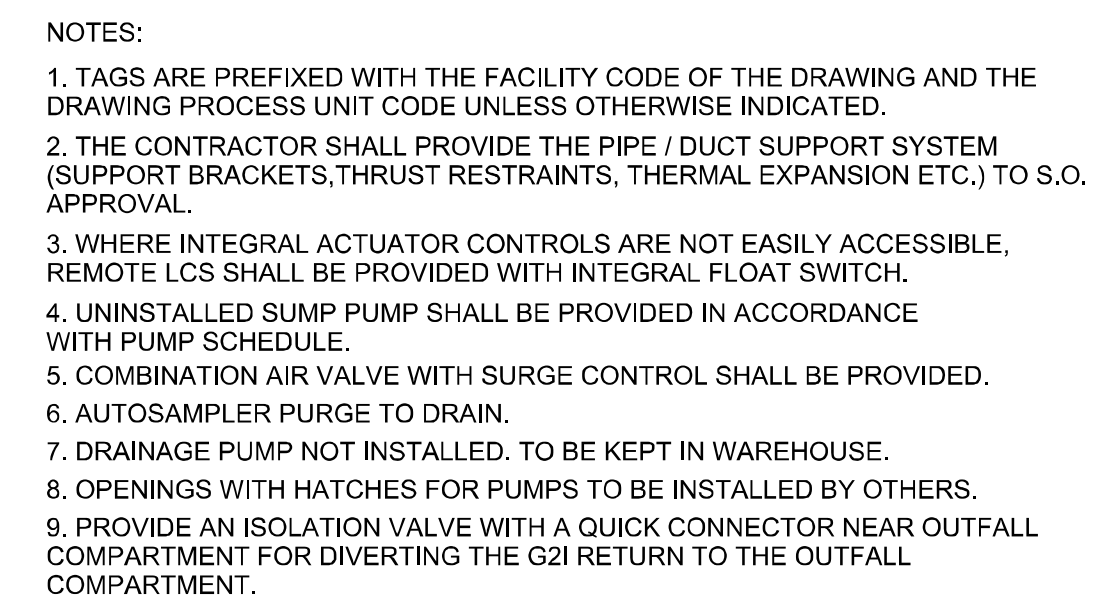

T1	20/05/22	ISSUED FOR TENDER C4B	CN	GOT	
T1	26/02/21	ISSUED FOR TENDER C3B1	CN	GOT	
T1	24/04/20	ISSUED FOR TENDER C3A	CN	GOT	
REV	DATE	DESCRIPTION	REVIEWED / AUTHORISED		

CLIENT:



PROGRAMME MANAGER:



CONSULTANT:

Jacobs.
CH2M HILL Singapore Pte Ltd

PROJECT TITLE:

TUAS WATER RECLAMATION PLANT (TWRP)
DTSS PHASE 2

	DRAWING TITLE
--	---------------

P&ID MBR FILTRATE TANK AND TRANSFER PUMPS PART 2

DRAFTED: A1	DESIGNED: KT	SHEET SIZE: A1
DRAFTING CHECK: DW	DESIGN CHECK: RM	SCALE: NTS
DATE: 06/12/17	REVIEWED: CN	PBS: 131101
CONTRACT: DRAWING NUMBER:		
PUB-DTSS2-TWRP		
SHEET NUMBER: WIL23-P-6080		REVISION: T1
THIS DRAWING IS COPYRIGHT		