


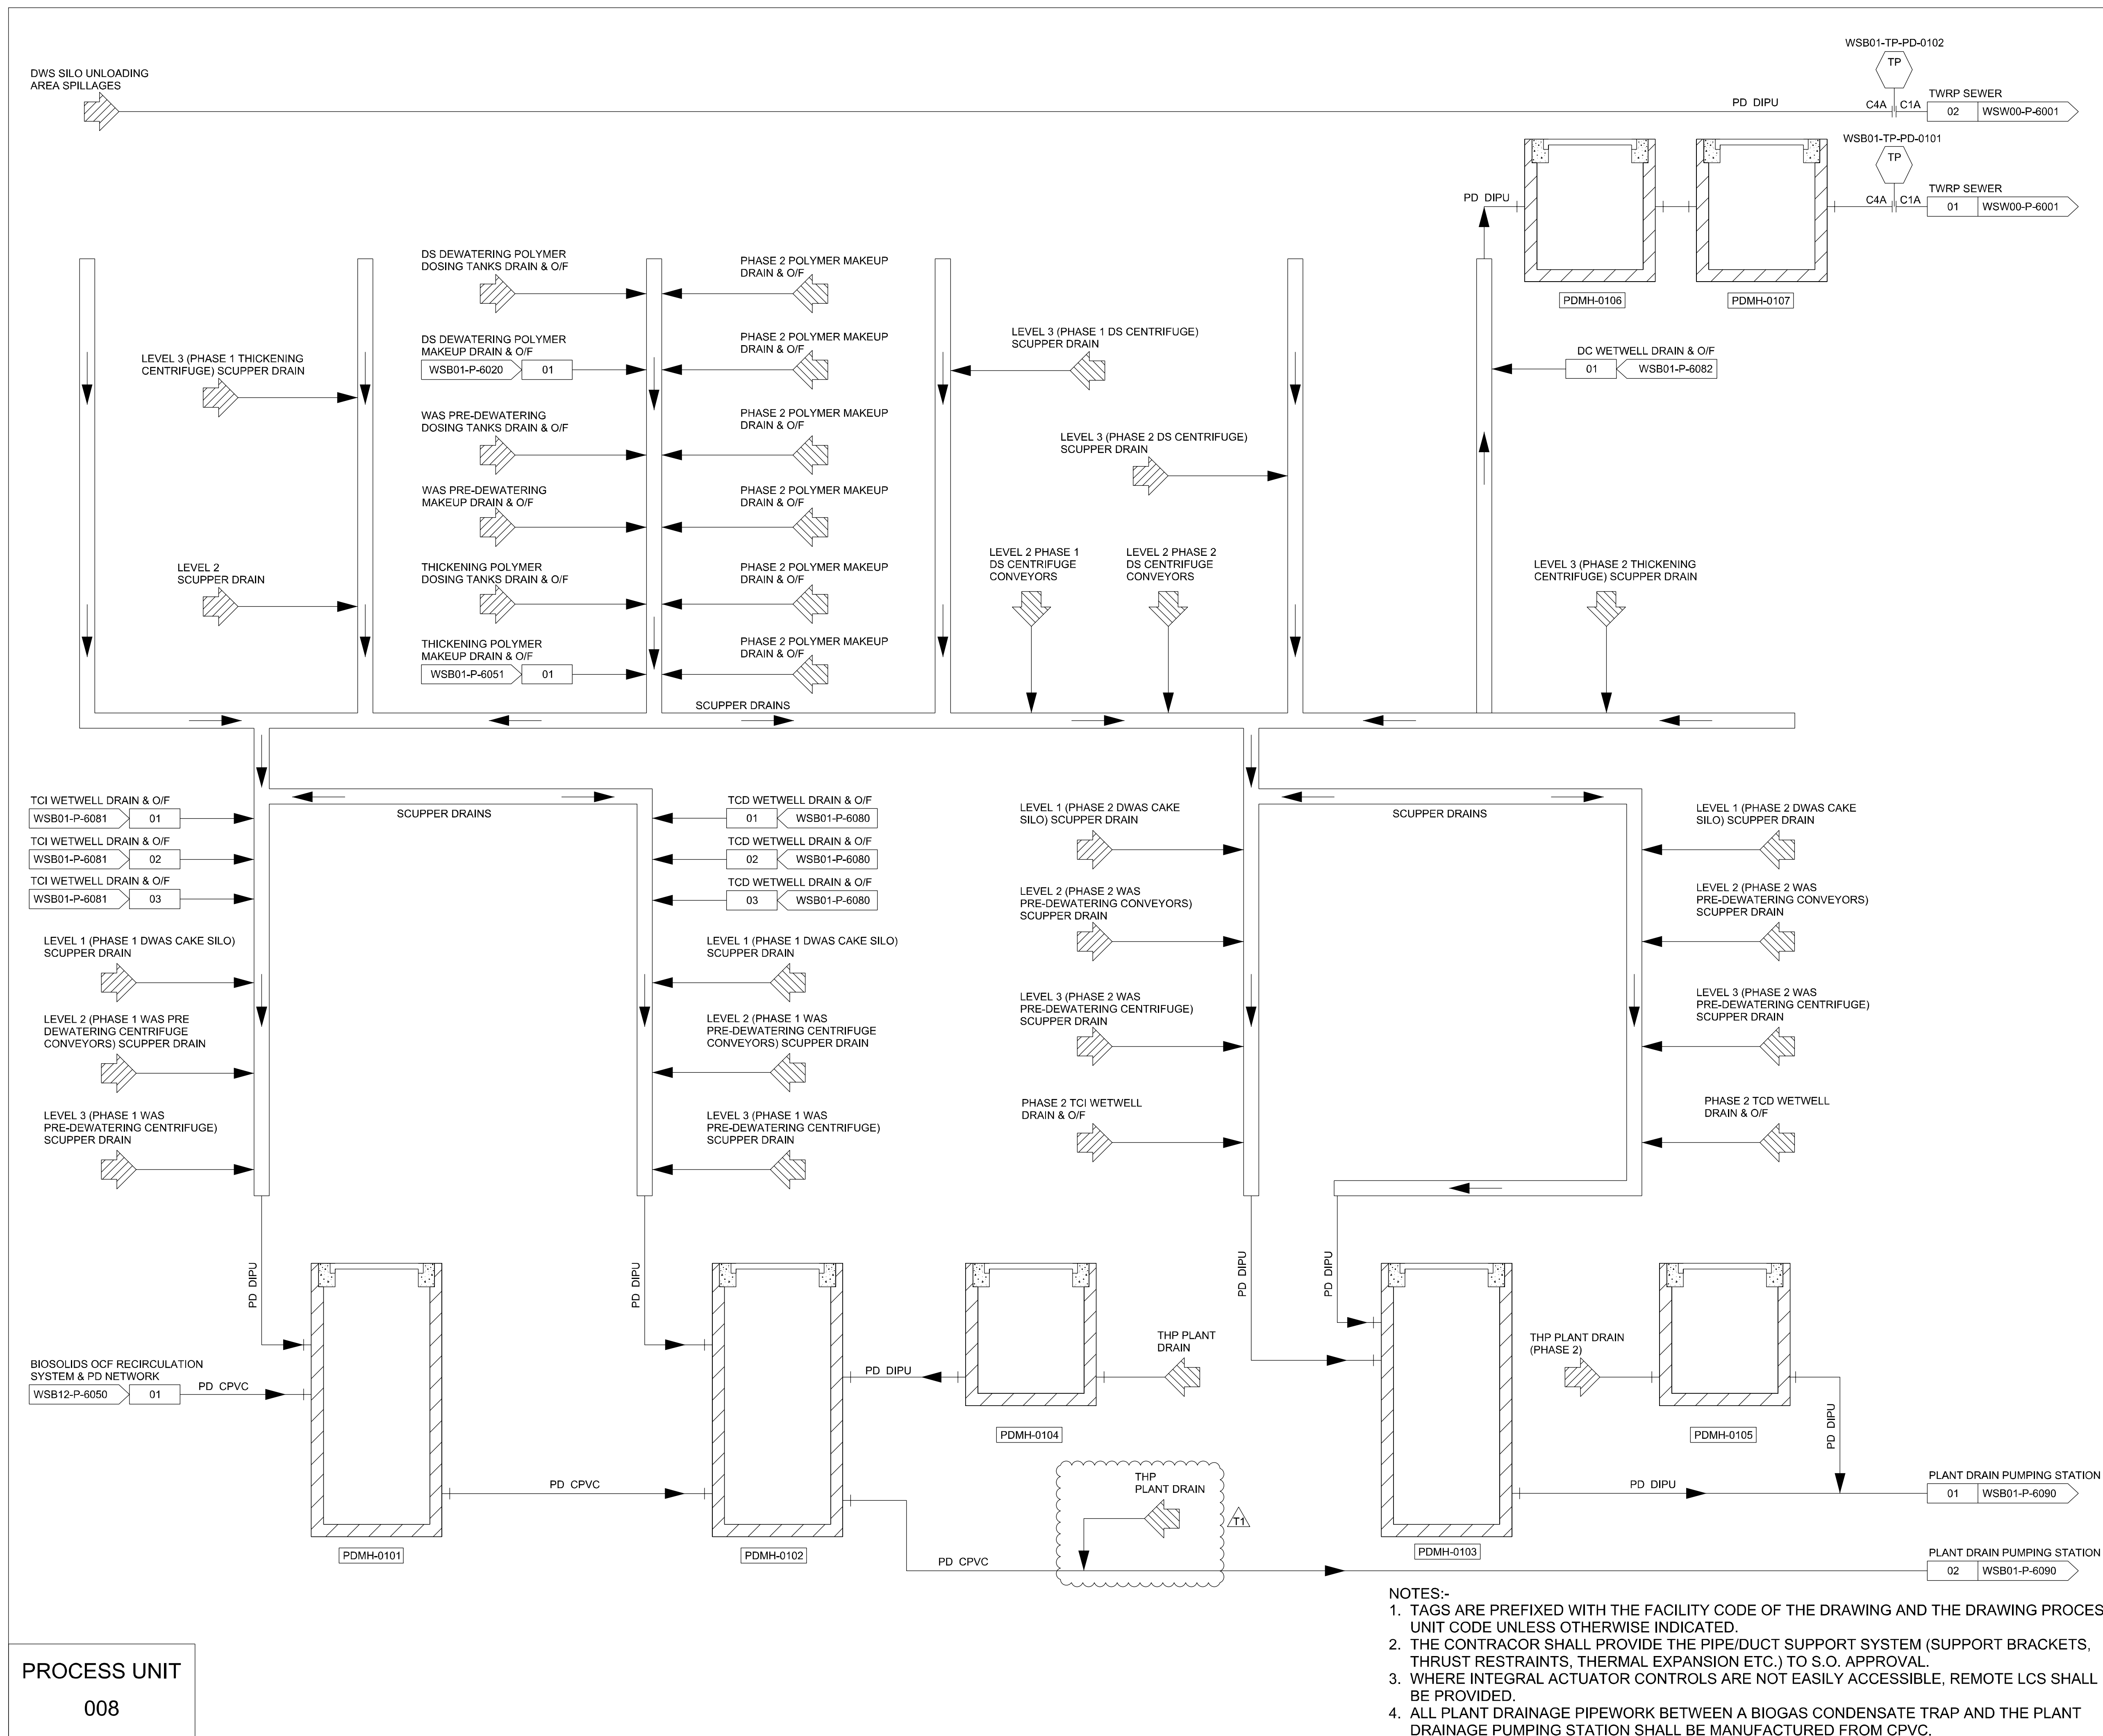

TENDER

T1	20/05/22	ISSUED FOR TENDER C4B	CN	GOT
T2	23/09/19	ISSUED FOR ADDENDUM 1	CN	GOT
T3	23/08/19	ISSUED FOR TENDER C4A	CN	GOT
REV	DATE	DESCRIPTION	REVIEWED AUTHORISED	

CLIENT:



PROGRAMME MANAGER:

B&V ■■ AECOM
A joint venture of Black & Veatch and AECOM

CONSULTANT:

JACOBS®
CH2M HILL Singapore Pte Ltd

PROJECT TITLE:

TUAS WATER RECLAMATION PLANT (TWRP)
DTSS PHASE 2

DRAWING TITLE

P&ID
BIOSOLIDS BUILDING
PD NETWORK

DRAFTED: PS	DESIGNED: KV	SHEET SIZE: A1
DRAFTING CHECK: ASR	DESIGN CHECK: CN	SCALE: NTS
DATE: 04/07/19	REVIEWED: CN	PBS: 131101

PIIB-DTSS2-TWBP

SHEET NUMBER: WSB01-P-6300	REVISION: T1
--------------------------------------	------------------------

THIS DRAWING IS COPYRIGHT