


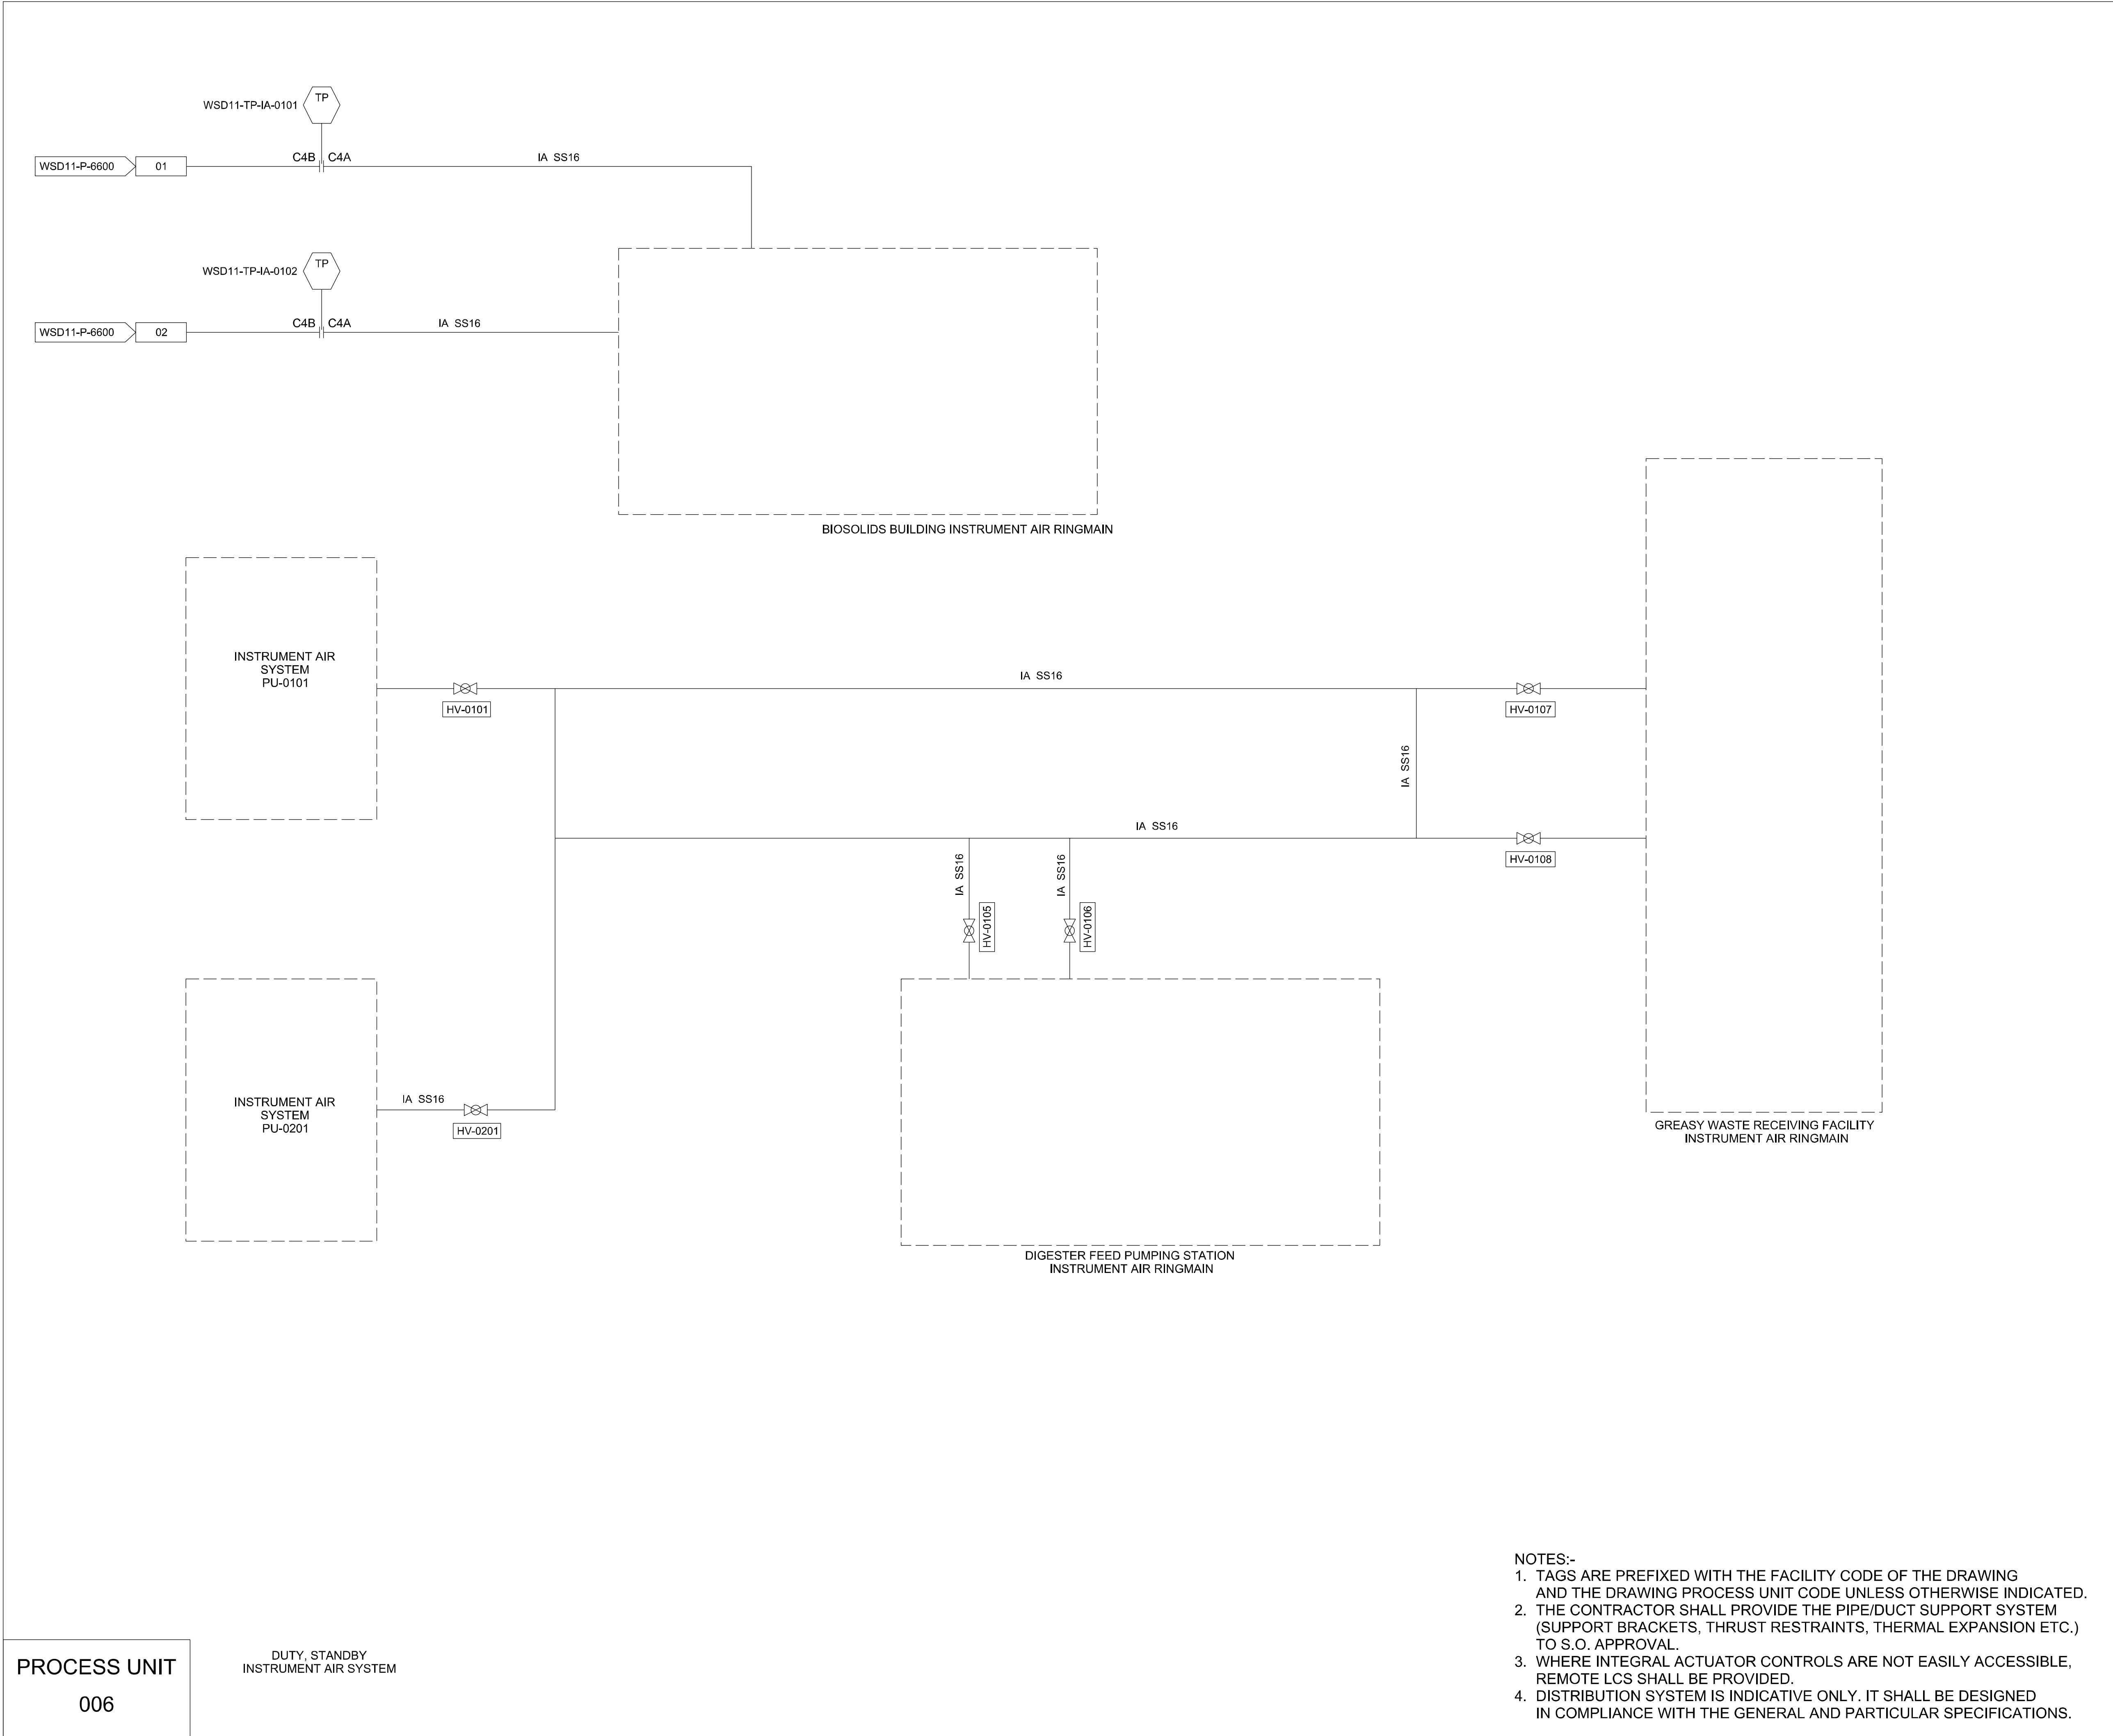

TENDER

T1	20/05/22	ISSUED FOR TENDER C4B	CN	GOT	
T1	23/08/19	ISSUED FOR TENDER C4A	CN	GOT	
REV	DATE	DESCRIPTION	REVIEWED	AUTHORISED	

CLIENT:

PROGRAMME MANAGER:

A joint venture of Black & Veatch and AECOM

CONSULTANT:

CH2M HILL Singapore Pte Ltd

PROJECT TITLE:

TUAS WATER RECLAMATION PLANT (TWRP)
DTSS PHASE 2

DRAWING TITLE

P&ID
BIOSOLID INSTRUMENT AIR
NETWORK

DRAFTED: SC	DESIGNED: KV	SHEET SIZE: A1
DRAFTING CHECK: ASR	DESIGN CHECK: CN	SCALE: NTS
DATE: 04/07/19	REVIEWED: CN	PBS: 131101

CONTRACT:	DRAWING NUMBER:	
-	PUB-DTSS2-TWRP	
	SHEET NUMBER: WSB01-P-6600	REVISION: T1

THIS DRAWING IS COPYRIGHT

- NOTES:-
1. TAGS ARE PREFIXED WITH THE FACILITY CODE OF THE DRAWING AND THE DRAWING PROCESS UNIT CODE UNLESS OTHERWISE INDICATED.
 2. THE CONTRACTOR SHALL PROVIDE THE PIPE/DUCT SUPPORT SYSTEM (SUPPORT BRACKETS, THRUST RESTRAINTS, THERMAL EXPANSION ETC.) TO S.O. APPROVAL.
 3. WHERE INTEGRAL ACTUATOR CONTROLS ARE NOT EASILY ACCESSIBLE, REMOTE LCS SHALL BE PROVIDED.
 4. DISTRIBUTION SYSTEM IS INDICATIVE ONLY. IT SHALL BE DESIGNED IN COMPLIANCE WITH THE GENERAL AND PARTICULAR SPECIFICATIONS.

PROCESS UNIT
006

DUTY, STANDBY
INSTRUMENT AIR SYSTEM