
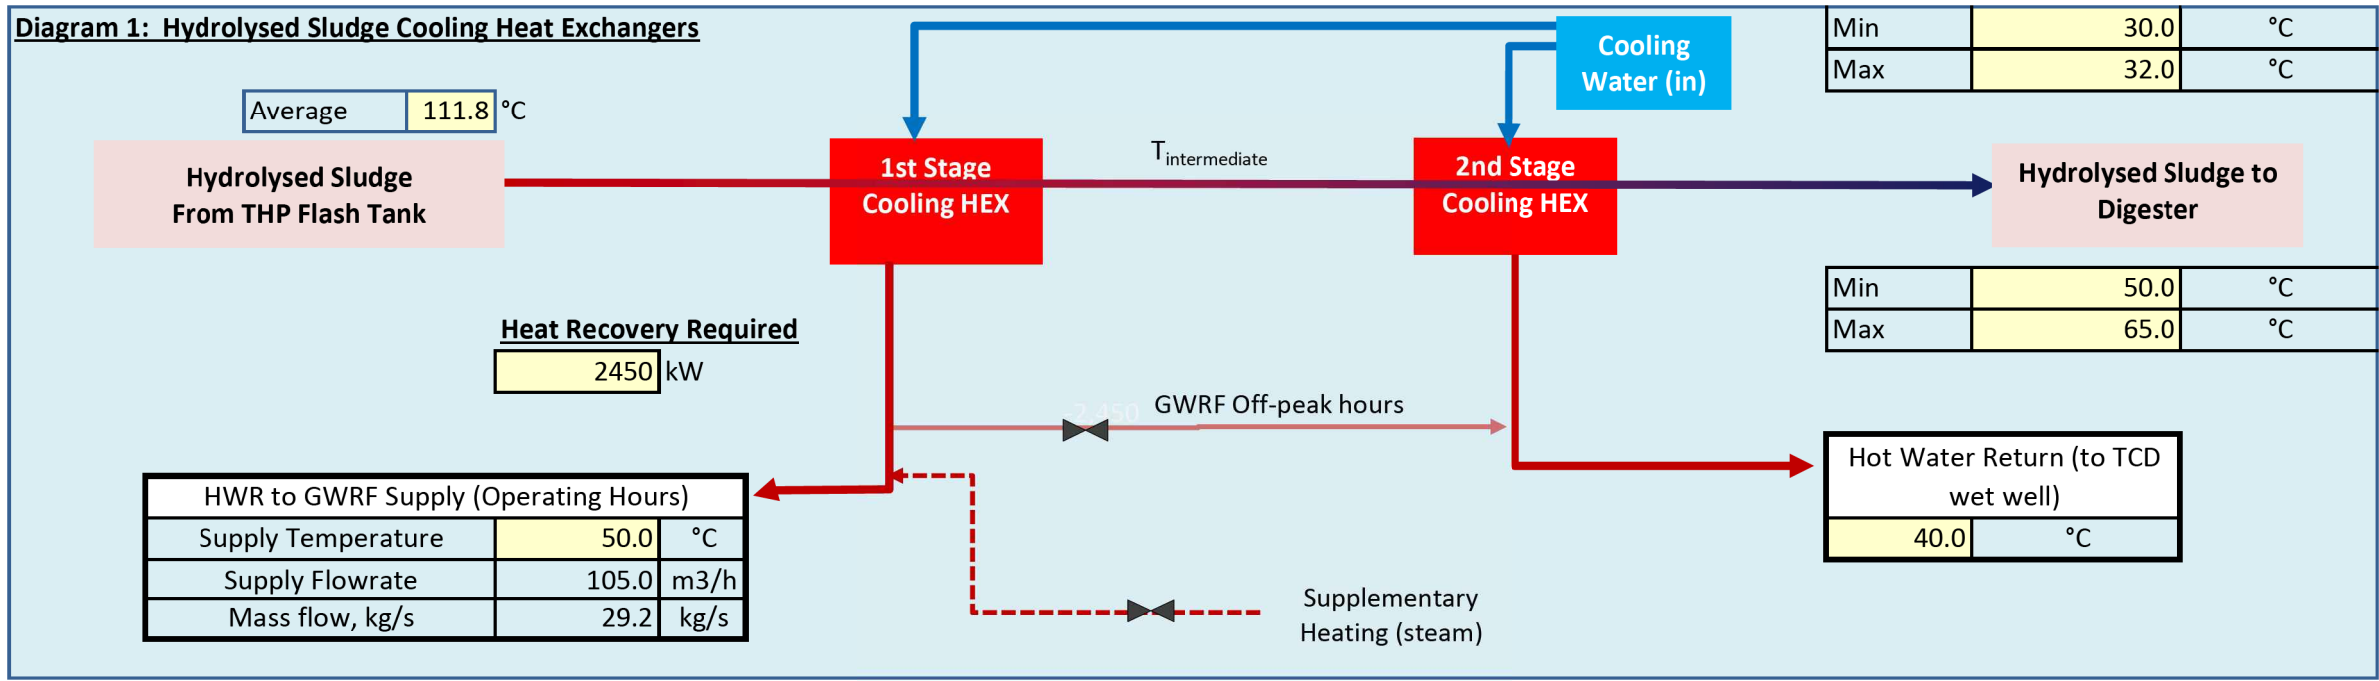


Scenario Design-AAL with PSD to THP

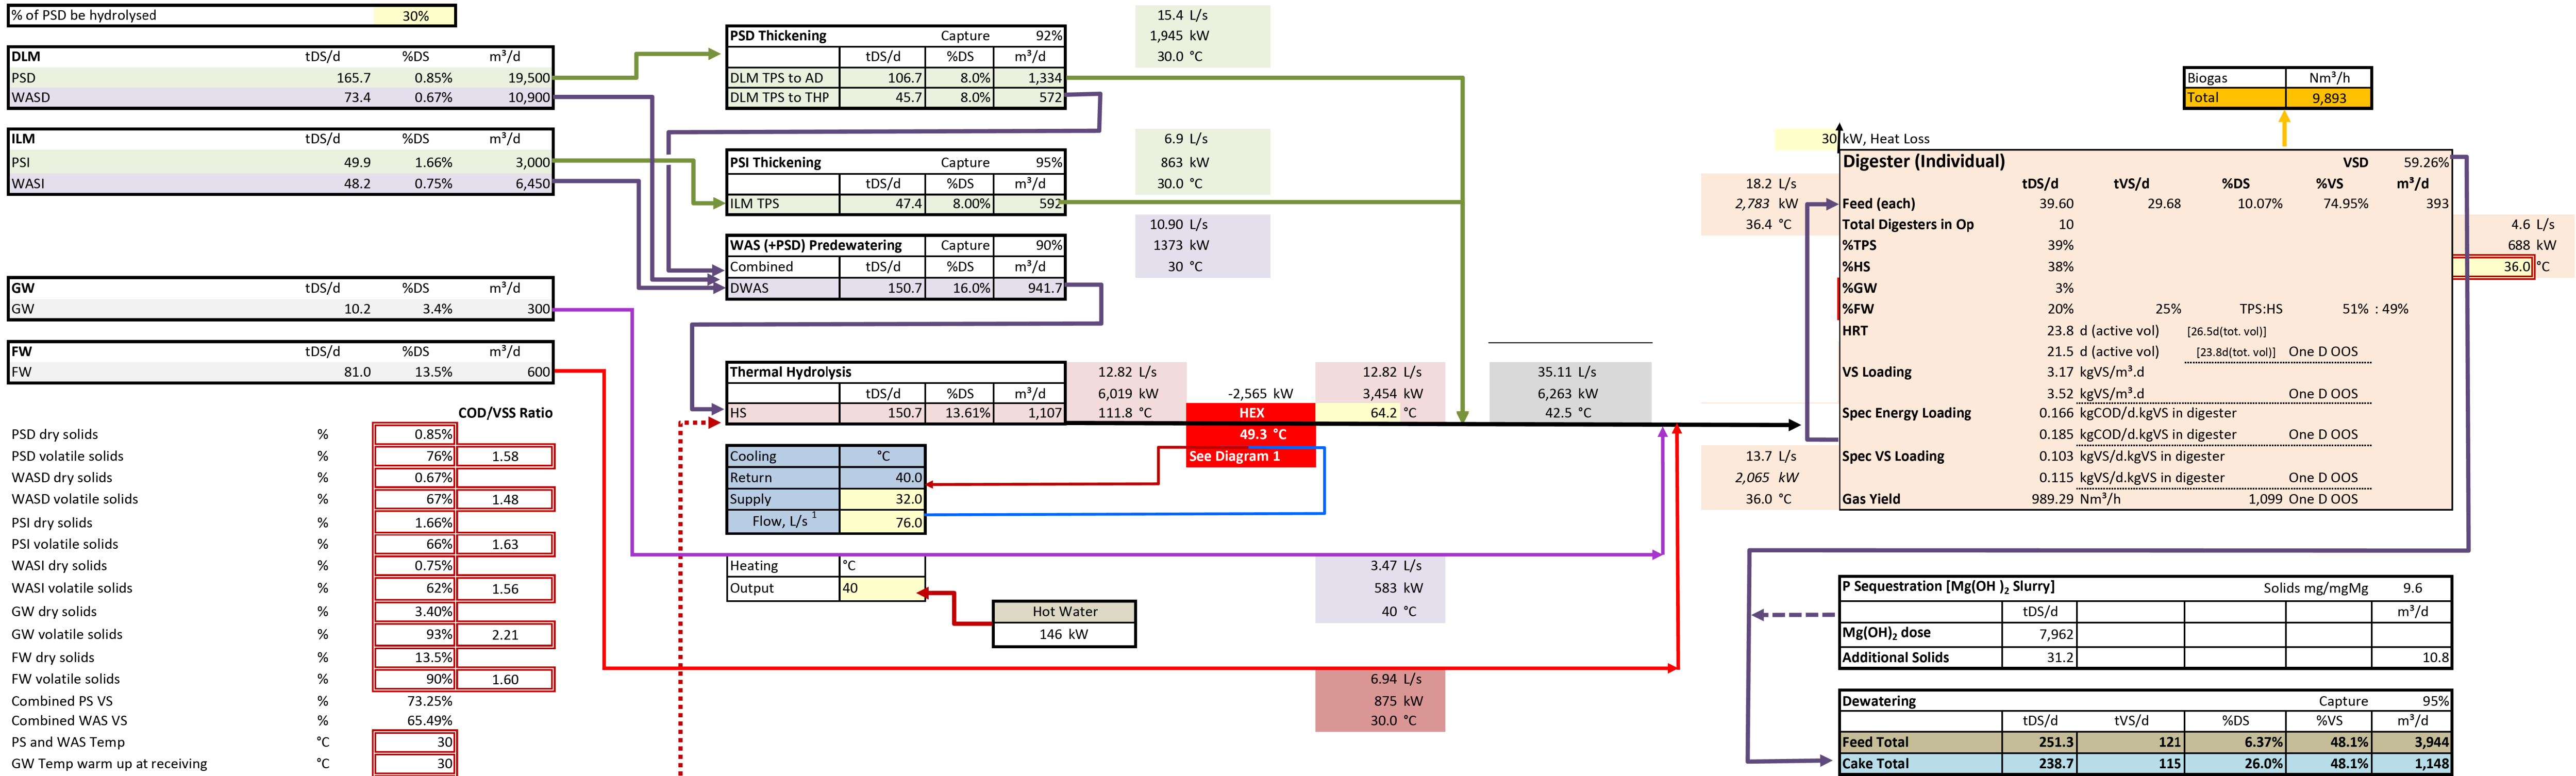

- Notes:
- 1 Cooling water flow does not include the flow required for temperature control dilution
  - 2 This mass and energy balance is provisional and mass and energy balances for particular THP systems will be required
  - 3 The kW figures shown above are values of the enthalpy of the stream

PFD- BIOSOLIDS MASS / HEAT BALANCE ANNUAL AVERAGE - PHASE 1

TENDER

|     |          |                         |          |            |
|-----|----------|-------------------------|----------|------------|
|     |          |                         |          |            |
|     |          |                         |          |            |
|     |          |                         |          |            |
| T1  | 20/05/22 | ISSUED FOR TENDER C4B   | CN       | GOT        |
| T2  | 12/11/20 | ISSUED FOR VARIATION    | CN       | GOT        |
| T1  | 16/08/19 | ISSUED FOR TENDER - C4A | CN       | GOT        |
| REV | DATE     | DESCRIPTION             | REVIEWED | AUTHORISED |



PROJECT TITLE:  
TUAS WATER RECLAMATION PLANT (TWRP)  
DTSS PHASE 2

DRAWING TITLE  
PFD  
BIOSOLIDS MASS/HEAT BALANCE  
ANNUAL AVERAGE

|                        |                                   |                               |
|------------------------|-----------------------------------|-------------------------------|
| DRAFTED:<br>AM         | DESIGNED:<br>JZ                   | SHEET SIZE:<br>A1             |
| DRAFTING CHECK:<br>ASR | DESIGN CHECK:<br>CN               | SCALE:<br>NTS                 |
| DATE:<br>16/08/19      | REVIEWED:<br>CN                   | PBS:<br>131101                |
| CONTRACT:<br>-         | DRAWING NUMBER:<br>PUB-DTSS2-TWRP | SHEET NUMBER:<br>WSD00-P-7001 |
|                        |                                   | REVISION:<br>T1               |

THIS DRAWING IS COPYRIGHT