


Scenario Design-MML with PSD to THP

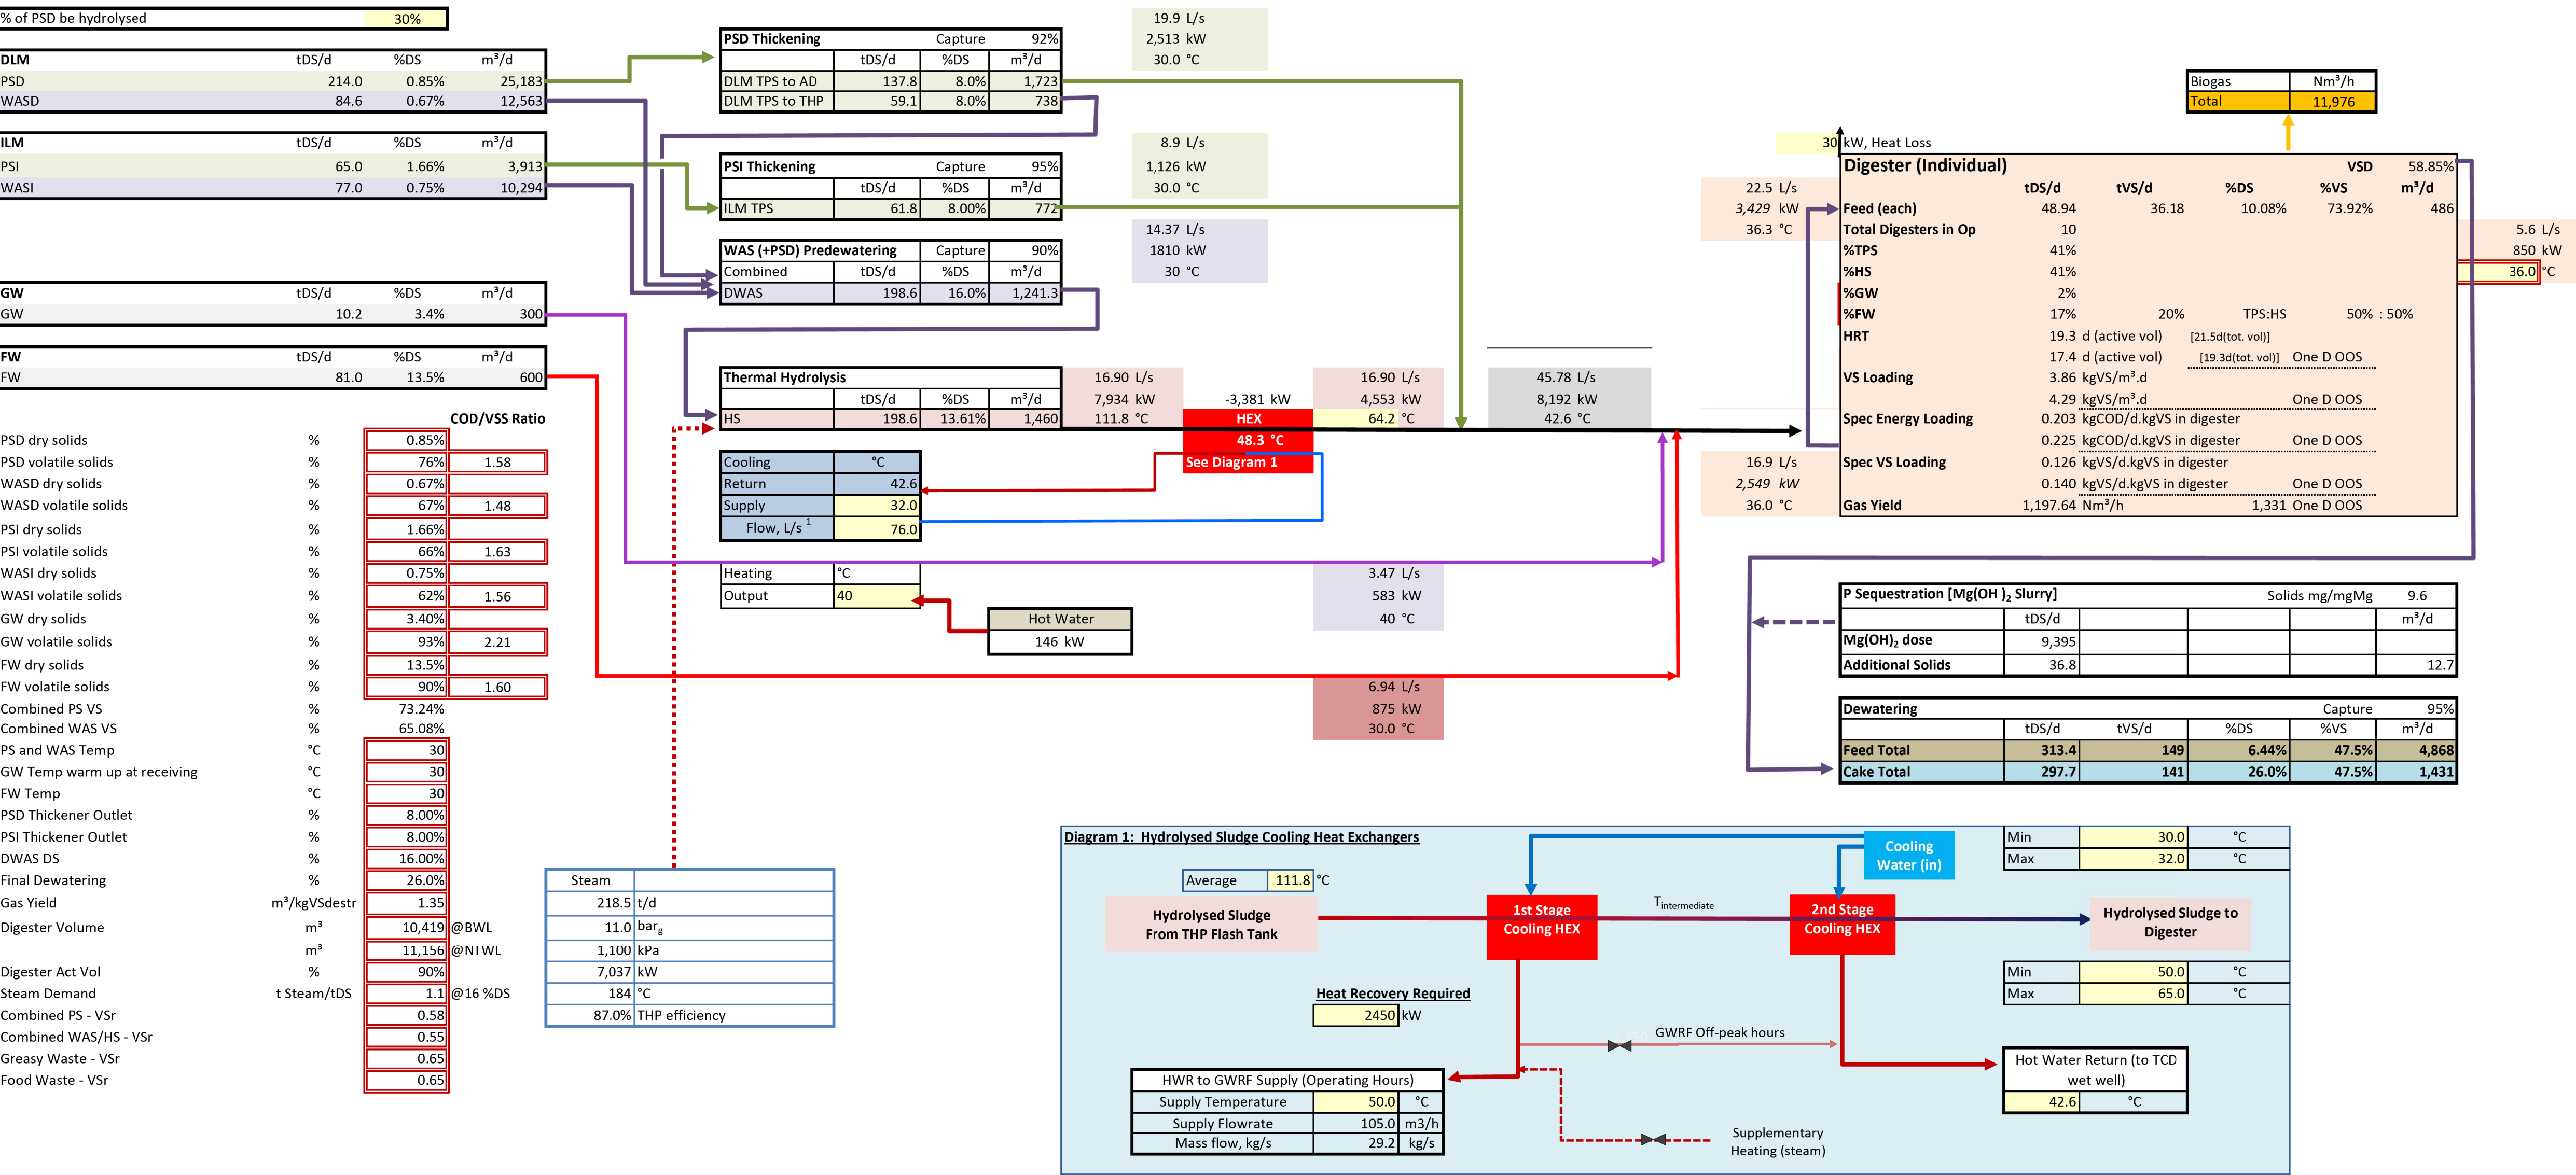

PFD- BIOSOLIDS MASS / HEAT BALANCE MONTHLY MAXIMUM - PHASE 1

TENDER

T1	20/05/22	ISSUED FOR TENDER C4B	CN GOT
T2	11/12/20	ISSUED FOR VARIATION	CN GOT
T1	16/08/19	ISSUED FOR TENDER - C4A	CN GOT
REV	DATE	DESCRIPTION	REVIEWED / AUTHORISED



PROJECT TITLE:
TUAS WATER RECLAMATION PLANT (TWRP)
DTSS PHASE 2

DRAWING TITLE:
PFD
BIOSOLIDS MASS / HEAT BALANCE
MONTHLY MAXIMUM

DRAFTED: AM	DESIGNED: JZ	SHEET SIZE: A1
DRAFTING CHECK: ASR	DESIGN CHECK: CN	SCALE: NTS
DATE: 16/08/19	REVIEWED: CN	PBS: 131101
CONTRACT:	DRAWING NUMBER: PUB-DTSS2-TWRP	REVISION: T1

THIS DRAWING IS COPYRIGHT