


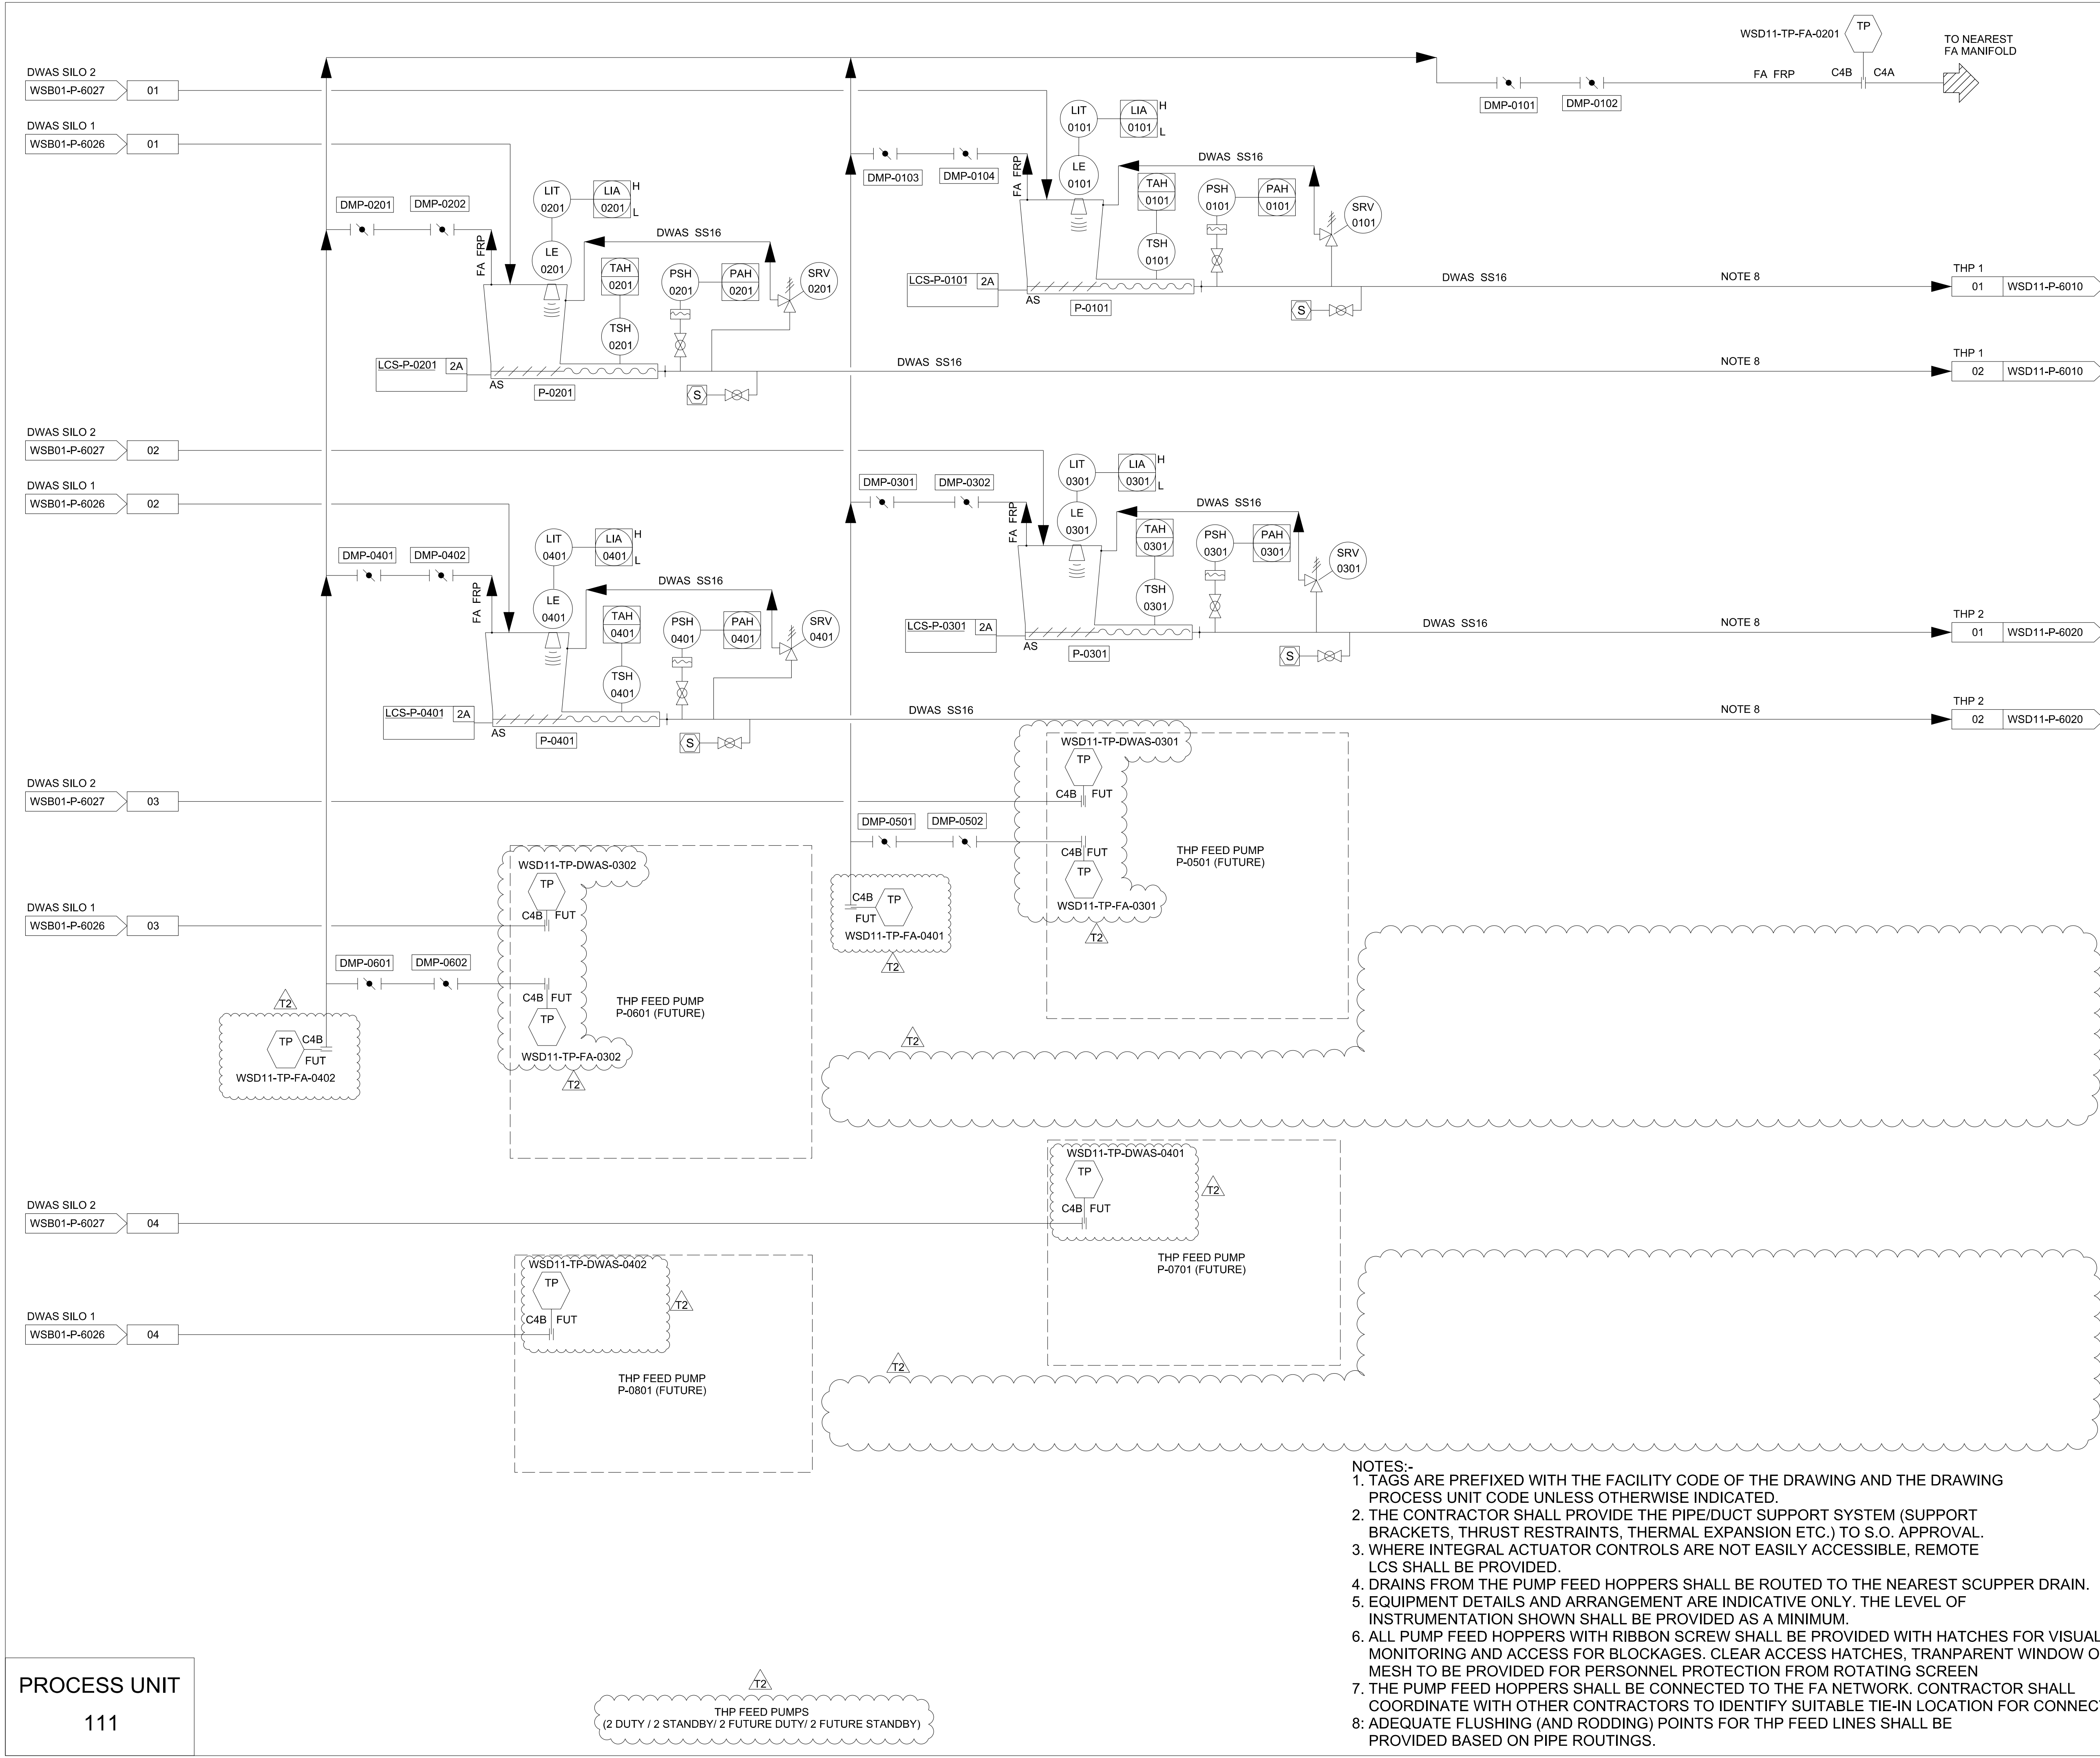

PROCESS UNIT
111

- NOTES:-
1. TAGS ARE PREFIXED WITH THE FACILITY CODE OF THE DRAWING AND THE DRAWING PROCESS UNIT CODE UNLESS OTHERWISE INDICATED.
 2. THE CONTRACTOR SHALL PROVIDE THE PIPE/DUCT SUPPORT SYSTEM (SUPPORT BRACKETS, THRUST RESTRAINTS, THERMAL EXPANSION ETC.) TO S.O. APPROVAL.
 3. WHERE INTEGRAL ACTUATOR CONTROLS ARE NOT EASILY ACCESSIBLE, REMOTE LCS SHALL BE PROVIDED.
 4. DRAINS FROM THE PUMP FEED HOPPERS SHALL BE ROUTED TO THE NEAREST SCUPPER DRAIN.
 5. EQUIPMENT DETAILS AND ARRANGEMENT ARE INDICATIVE ONLY. THE LEVEL OF INSTRUMENTATION SHOWN SHALL BE PROVIDED AS A MINIMUM.
 6. ALL PUMP FEED HOPPERS WITH RIBBON SCREW SHALL BE PROVIDED WITH HATCHES FOR VISUAL MONITORING AND ACCESS FOR BLOCKAGES. CLEAR ACCESS HATCHES, TRANSPARENT WINDOW OR MESH TO BE PROVIDED FOR PERSONNEL PROTECTION FROM ROTATING SCREEN
 7. THE PUMP FEED HOPPERS SHALL BE CONNECTED TO THE FA NETWORK. CONTRACTOR SHALL COORDINATE WITH OTHER CONTRACTORS TO IDENTIFY SUITABLE TIE-IN LOCATION FOR CONNECTOR.
 8. ADEQUATE FLUSHING (AND RODDING) POINTS FOR THP FEED LINES SHALL BE PROVIDED BASED ON PIPE ROUTINGS.

TENDER

T2	25/11/22	ISSUED FOR TENDER C4B (2ND STAGE)	CN	GOT
T1	20/05/22	ISSUED FOR TENDER C4B	CN	GOT
REV	DATE	DESCRIPTION	REVIEWED	AUTHORISED

CLIENT:

PUB

SINGAPORE'S
NATIONAL
WATER AGENCY

PROGRAMME MANAGER:

binnies

AECOM

A JOINT VENTURE DELIVERING THE DTSS2 PROJECT

CONSULTANT:

Jacobs

CH2M HILL Singapore Pte Ltd

PROJECT TITLE:

TUAS WATER RECLAMATION PLANT (TWRP)
DTSS PHASE 2

DRAWING TITLE

P&ID
THP FEED PUMPS

DRAFTED: PS	DESIGNED: KV	SHEET SIZE: A1
DRAFTING CHECK: ASR	DESIGN CHECK: CN	SCALE: NTS
DATE: 04/07/19	REVIEWED: CN	PBS: 131101
CONTRACT:	DRAWING NUMBER: PUB-DTSS2-TWRP	
	SHEET NUMBER: WSD11-P-6000	REVISION: T2

THIS DRAWING IS COPYRIGHT