


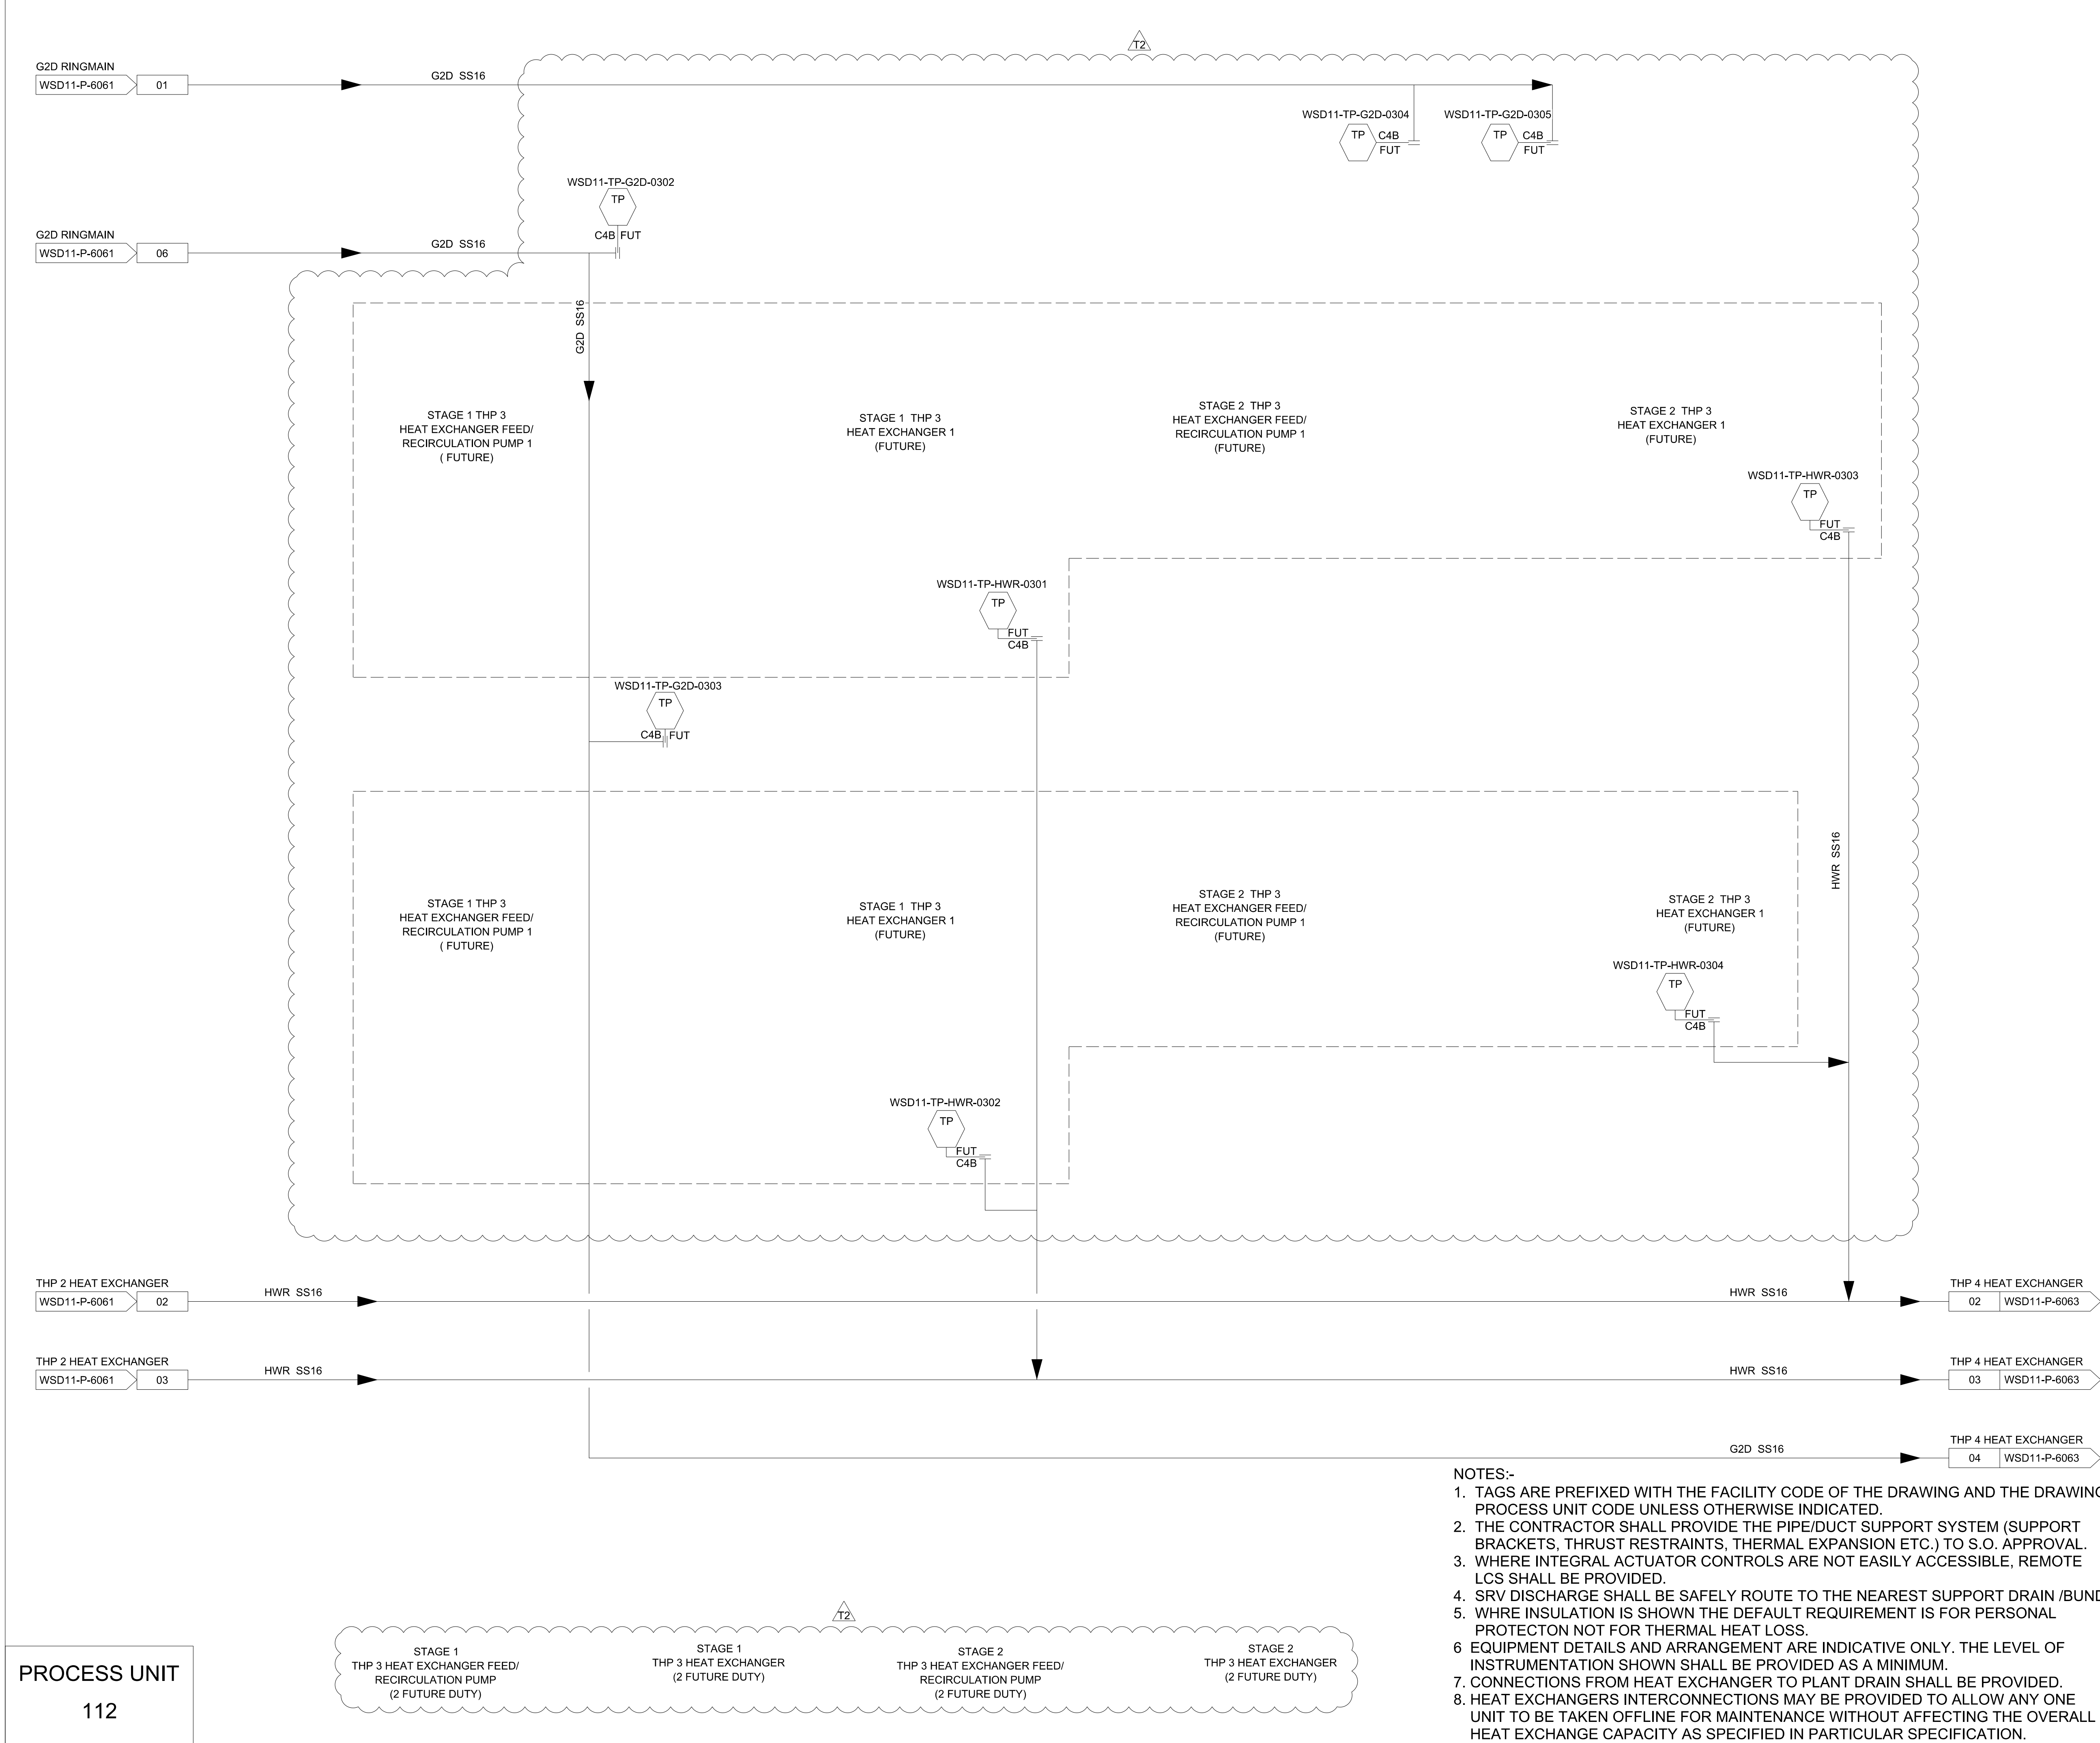

## TENDER

|     |          |                                   |          |            |
|-----|----------|-----------------------------------|----------|------------|
|     |          |                                   |          |            |
|     |          |                                   |          |            |
|     |          |                                   |          |            |
| T2  | 25/11/22 | ISSUED FOR TENDER C48 (2ND STAGE) | CN       | GOT        |
| T1  | 20/05/22 | ISSUED FOR TENDER C48             | CN       | GOT        |
| REV | DATE     | DESCRIPTION                       | REVIEWED | AUTHORISED |

CLIENT:



PROGRAMME MANAGER:



CONSULTANT:



PROJECT TITLE:

TUAS WATER RECLAMATION PLANT (TWRP)  
DTSS PHASE 2

DRAWING TITLE

P&ID  
THP 3 HEAT EXCHANGERS

|                        |                                   |                               |
|------------------------|-----------------------------------|-------------------------------|
| DRAFTED:<br>RSR        | DESIGNED:<br>KV                   | SHEET SIZE:<br>A1             |
| DRAFTING CHECK:<br>ASR | DESIGN CHECK:<br>CN               | SCALE:<br>NTS                 |
| DATE:<br>04/07/19      | REVIEWED:<br>CN                   | PBS:<br>131101                |
| CONTRACT:<br>-         | DRAWING NUMBER:<br>PUB-DTSS2-TWRP | SHEET NUMBER:<br>WSD11-P-6062 |
|                        |                                   | REVISION:<br>T2               |

THIS DRAWING IS COPYRIGHT