


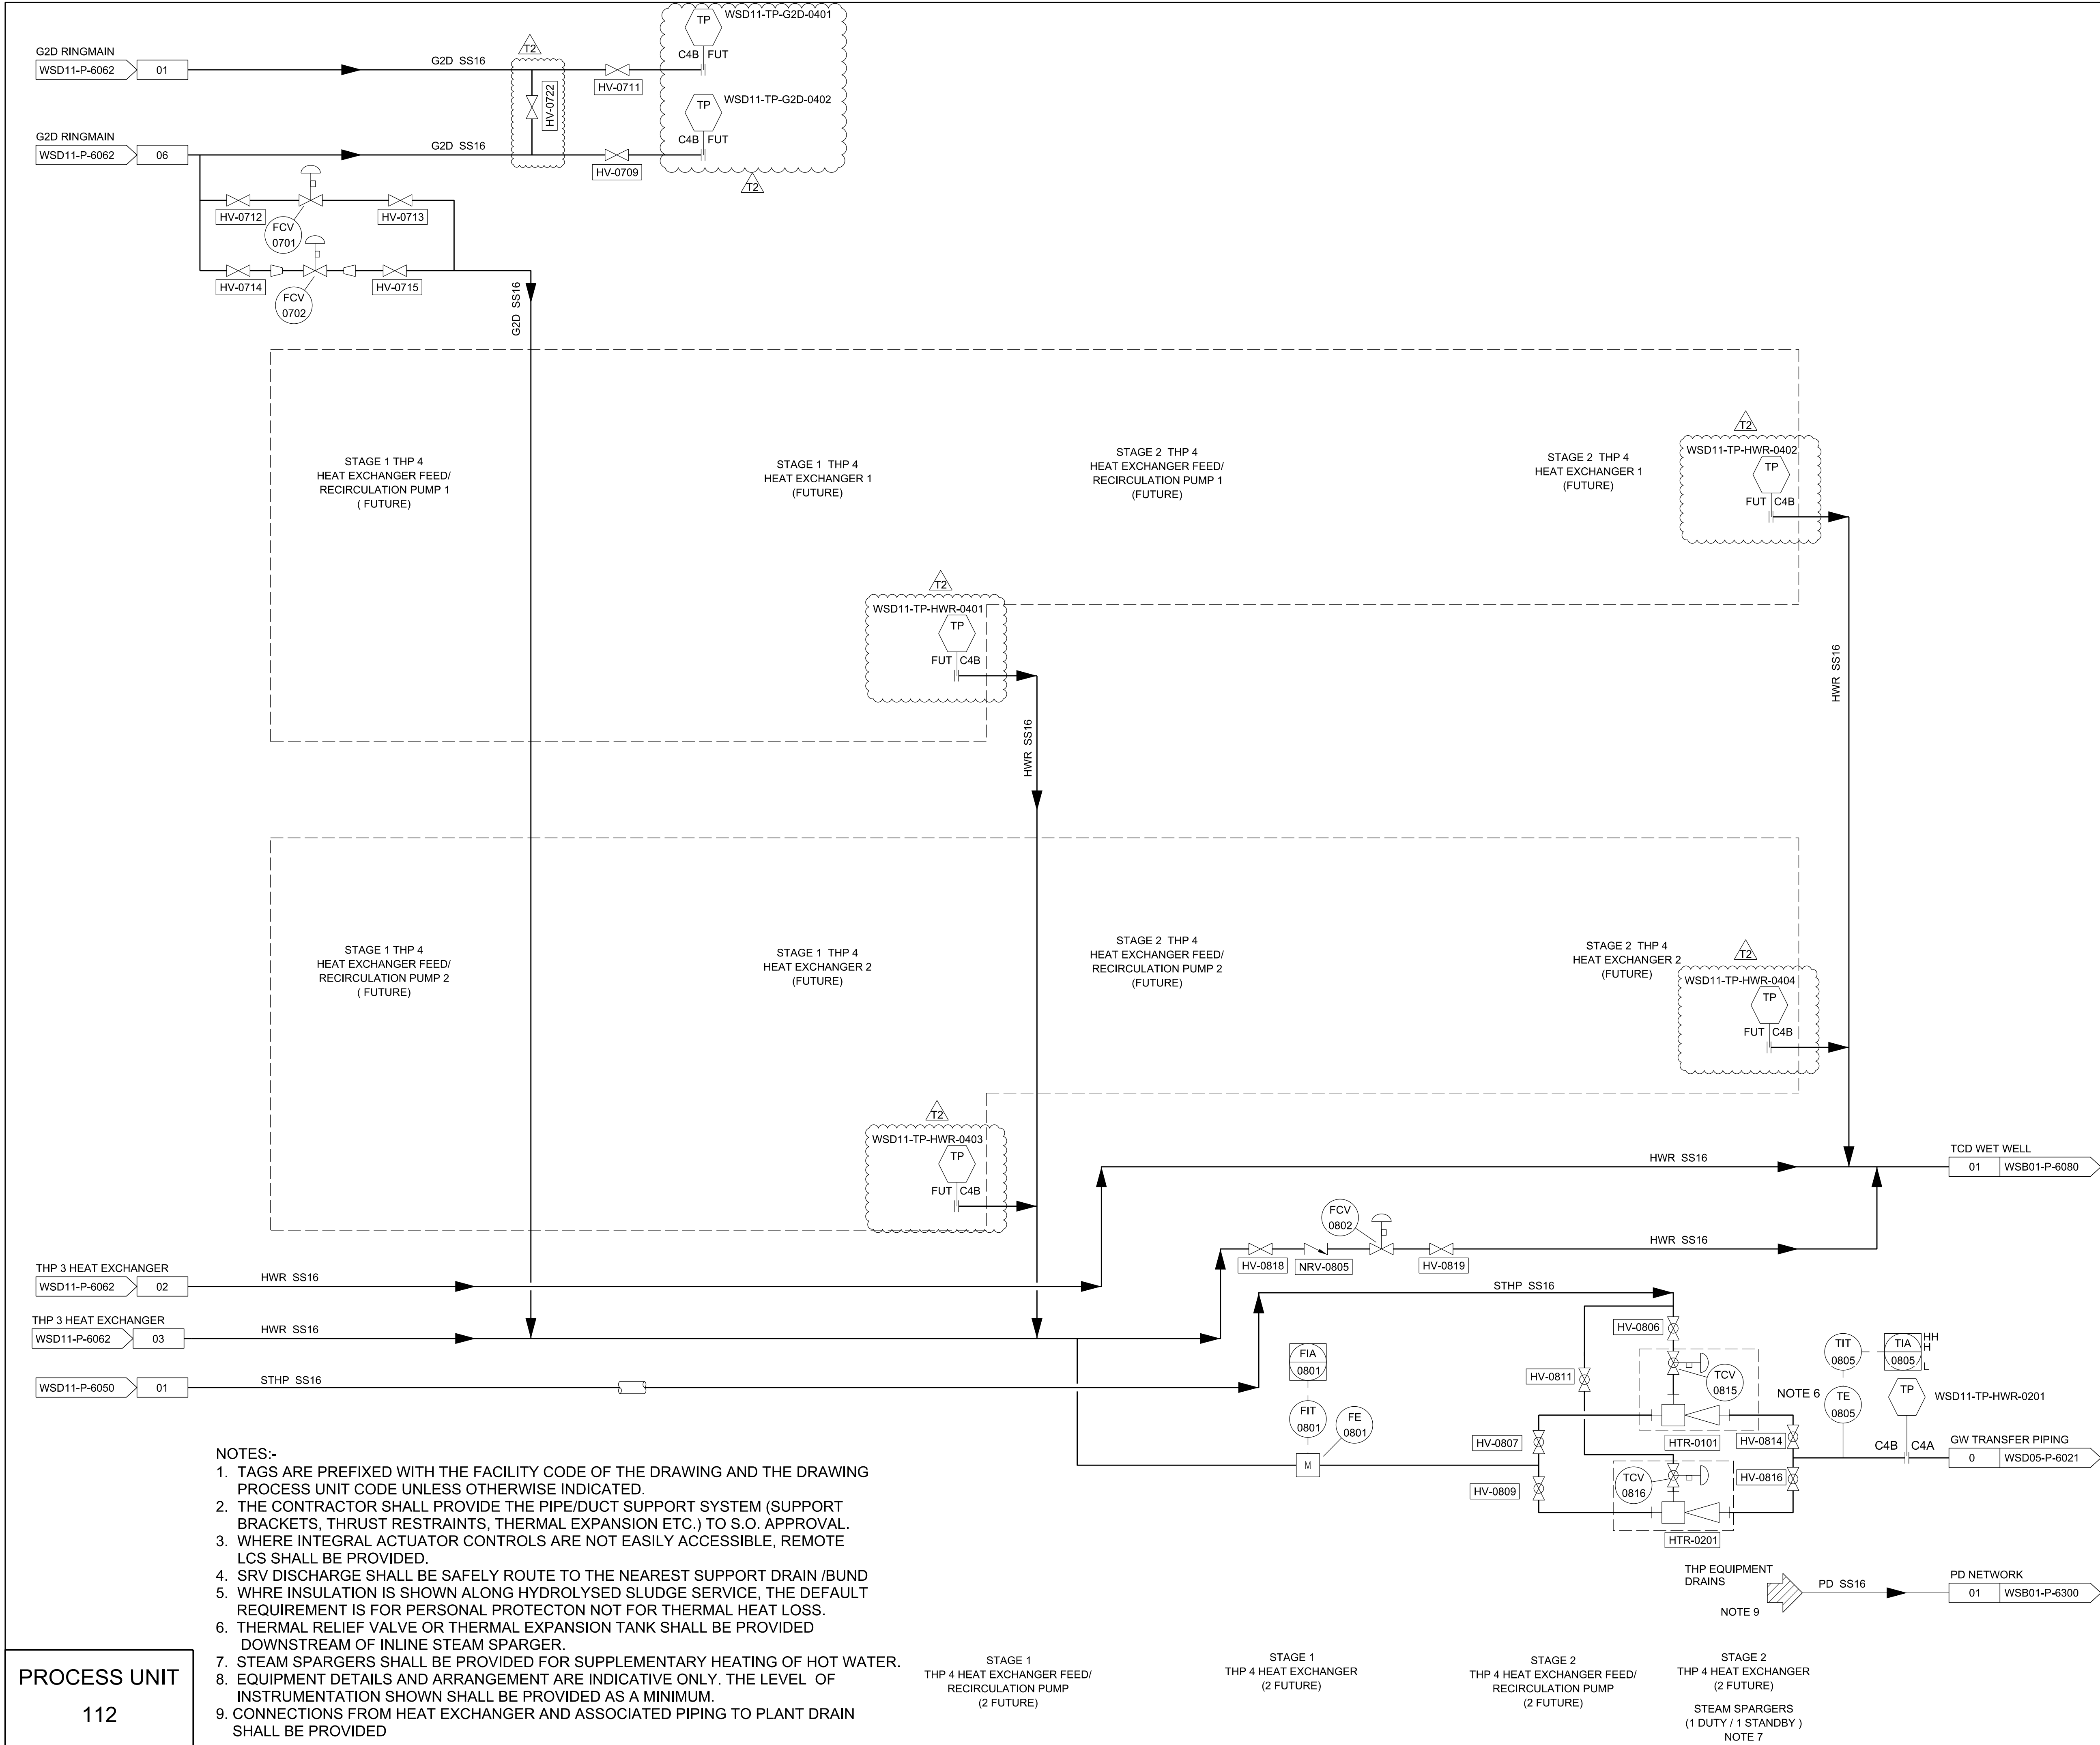

TENDER

T2	25/11/22	ISSUED FOR TENDER C4B (2ND STAGE)	CN	GOT
T1	20/05/22	ISSUED FOR TENDER C4B	CN	GOT
REV	DATE	DESCRIPTION	REVIEWED	AUTHORISED

CLIENT:

**PUB**
SINGAPORE'S NATIONAL WATER AGENCY

PROGRAMME MANAGER:

**binnies AECOM**
A JOINT VENTURE DELIVERING THE DTSS2 PROJECT

CONSULTANT:

**Jacobs**
CH2M HILL Singapore Pte Ltd

PROJECT TITLE:
**TUAS WATER RECLAMATION PLANT (TWRP)
DTSS PHASE 2**

DRAWING TITLE
**P&ID
THP 4 HEAT EXCHANGERS**

DRAFTED: RSR	DESIGNED: KV	SHEET SIZE: A1
DRAFTING CHECK: ASR	DESIGN CHECK: CN	SCALE: NTS
DATE: 04/07/19	REVIEWED: CN	PBS: 131101
CONTRACT: -	DRAWING NUMBER: PUB-DTSS2-TWRP	REVISION: T2
THIS DRAWING IS COPYRIGHT		