


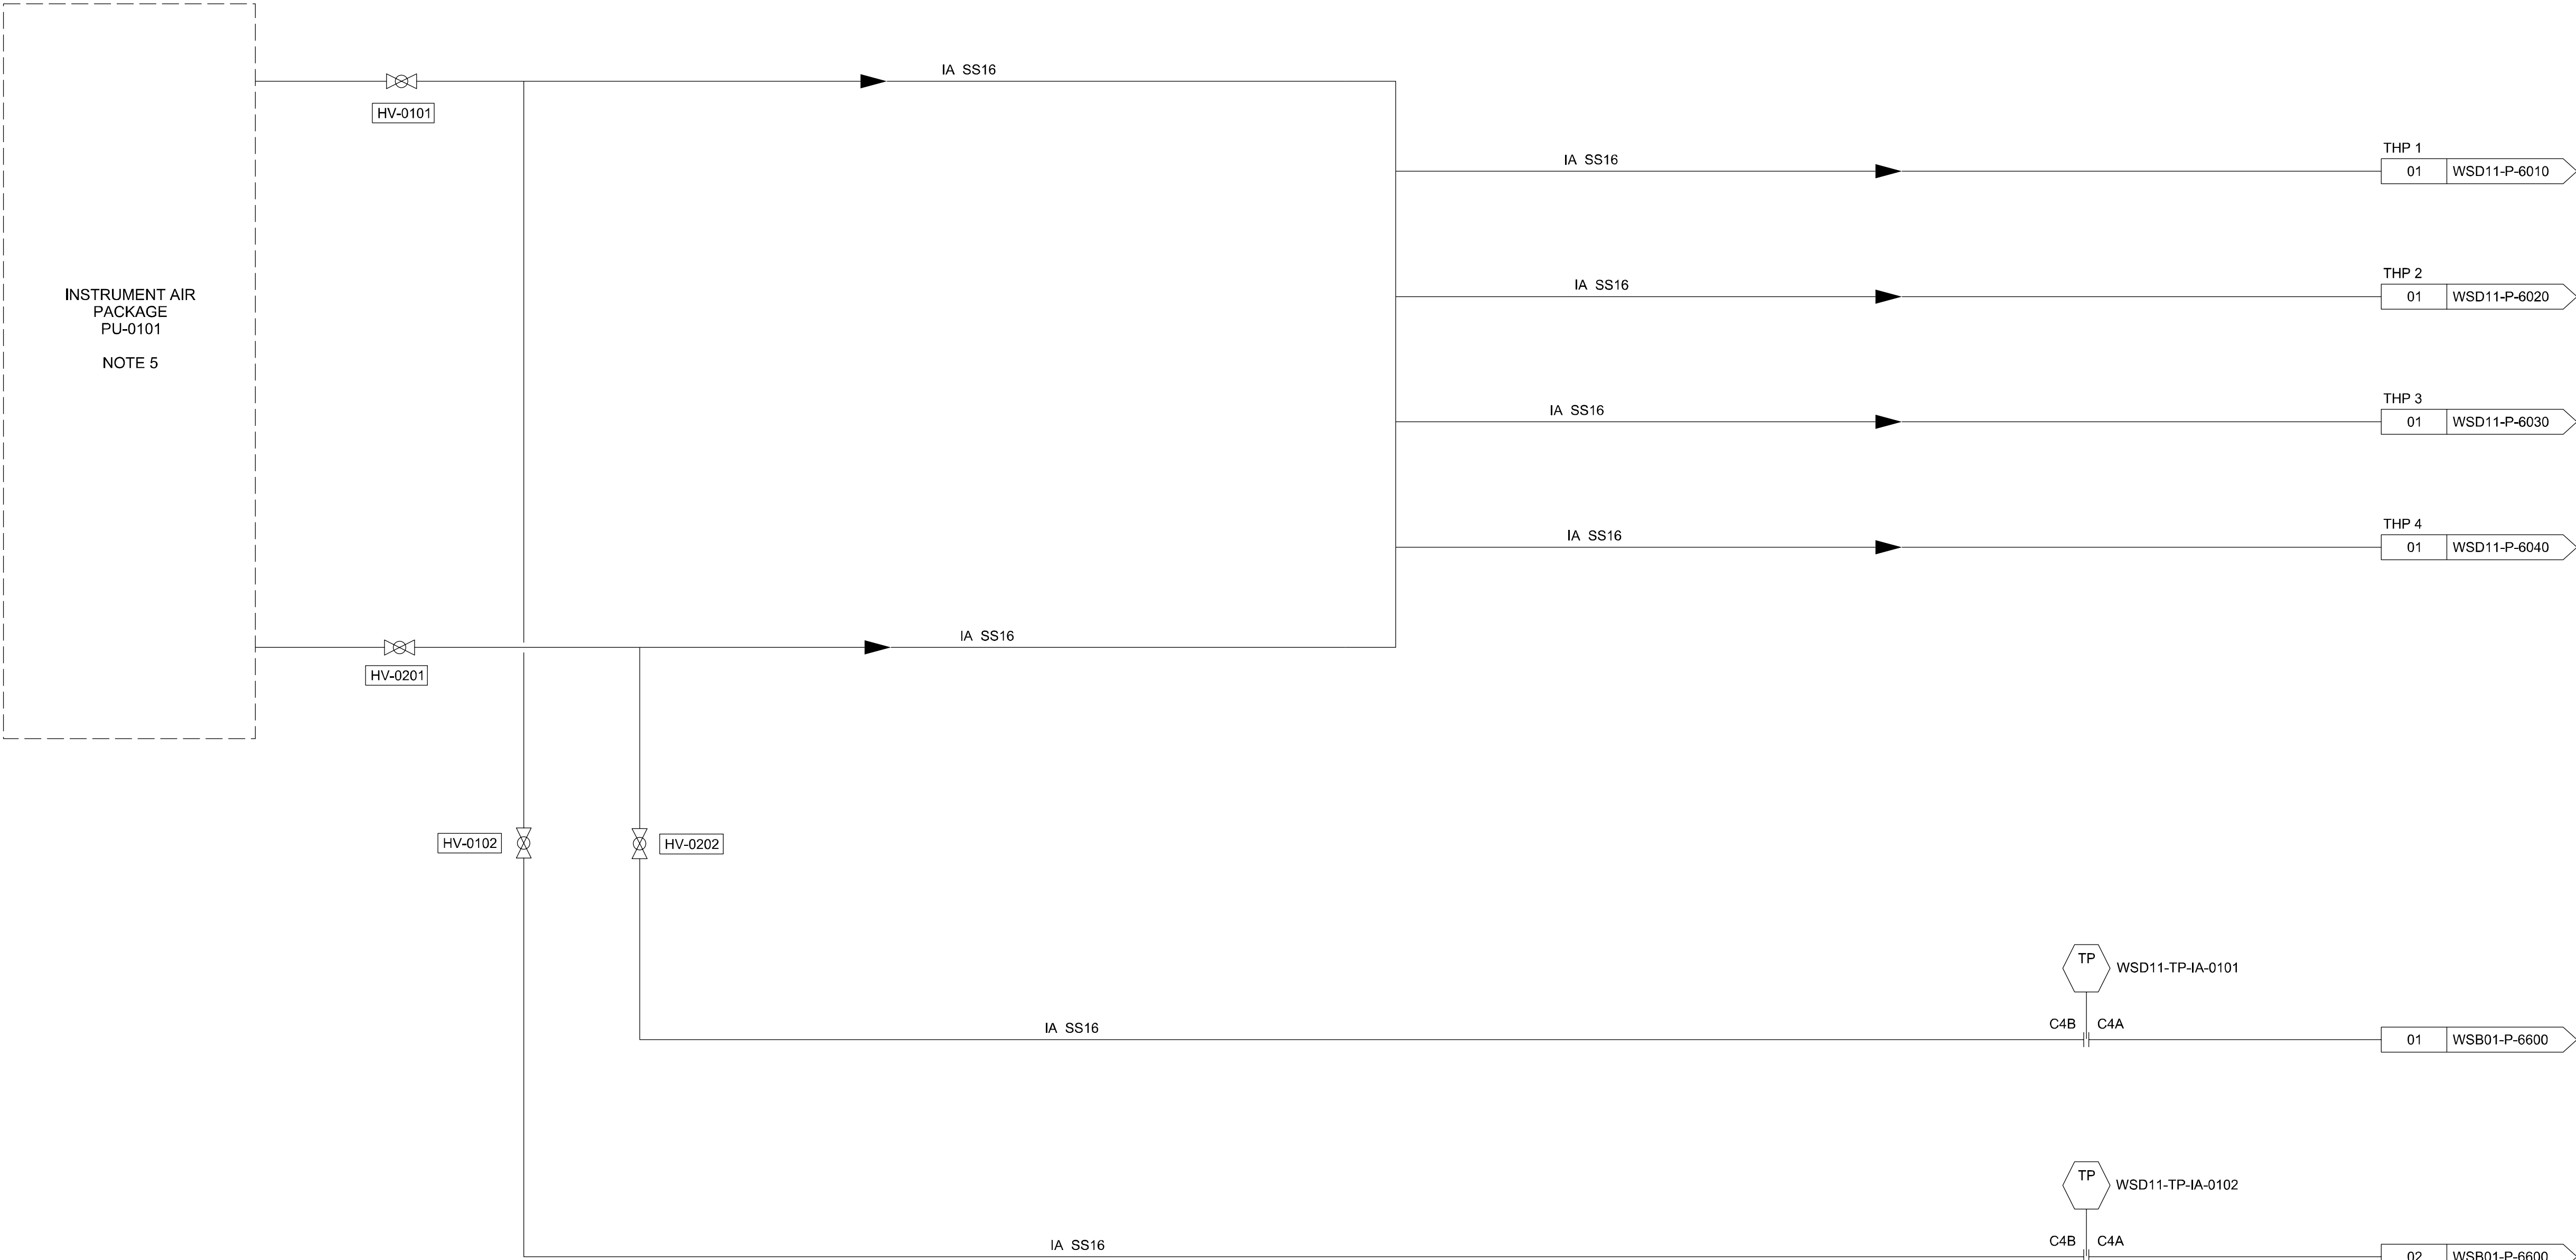

- NOTES:-
1. TAGS ARE PREFIXED WITH THE FACILITY CODE OF THE DRAWING AND THE DRAWING PROCESS UNIT CODE UNLESS OTHERWISE INDICATED.
 2. THE CONTRACTOR SHALL PROVIDE THE PIPE/DUCT SUPPORT SYSTEM (SUPPORT BRACKETS, THRUST RESTRAINTS, THERMAL EXPANSION ETC.) TO S.O. APPROVAL.
 3. WHERE INTEGRAL ACTUATOR CONTROLS ARE NOT EASILY ACCESSIBLE, REMOTE LCS SHALL BE PROVIDED.
 4. SRV RELEASE SHALL BE VENTED OUTSIDE THE BUILDING AND THE LOCATION OF VENTING SHALL NOT POSE A SAFETY HAZARD TO PERSONNEL.
 5. THE CONTRACTOR SHALL DESIGN TO COMPLY WITH REQUIREMENTS STATED IN THE PARTICULAR SPECIFICATIONS
 6. EQUIPMENT DETAILS AND ARRANGEMENT ARE INDICATIVE ONLY. THE LEVEL OF INSTRUMENTATION SHOWN SHALL BE PROVIDED AS A MINIMUM.

TENDER

T1	20/05/22	ISSUED FOR TENDER C4B	CN
REV	DATE	DESCRIPTION	REVIEWED / AUTHORISED

CLIENT:



SINGAPORE'S
NATIONAL
WATER AGENCY

PROGRAMME MANAGER:



A JOINT VENTURE DELIVERING THE DTSS2 PROJECT

CONSULTANT:



CH2M HILL Singapore Pte Ltd

PROJECT TITLE:

TUAS WATER RECLAMATION PLANT (TWRP)
DTSS PHASE 2

DRAWING TITLE

P&ID
THP AREA
INSTRUMENT AIR NETWORK

DRAFTED: PS	DESIGNED: KV	SHEET SIZE: A1
DRAFTING CHECK: ASR	DESIGN CHECK: CN	SCALE: NTS
DATE: 04/07/19	REVIEWED: CN	PBS: 131101
CONTRACT:	DRAWING NUMBER: PUB-DTSS2-TWRP	
-	SHEET NUMBER: WSD11-P-6600	REVISION: T1

THIS DRAWING IS COPYRIGHT