


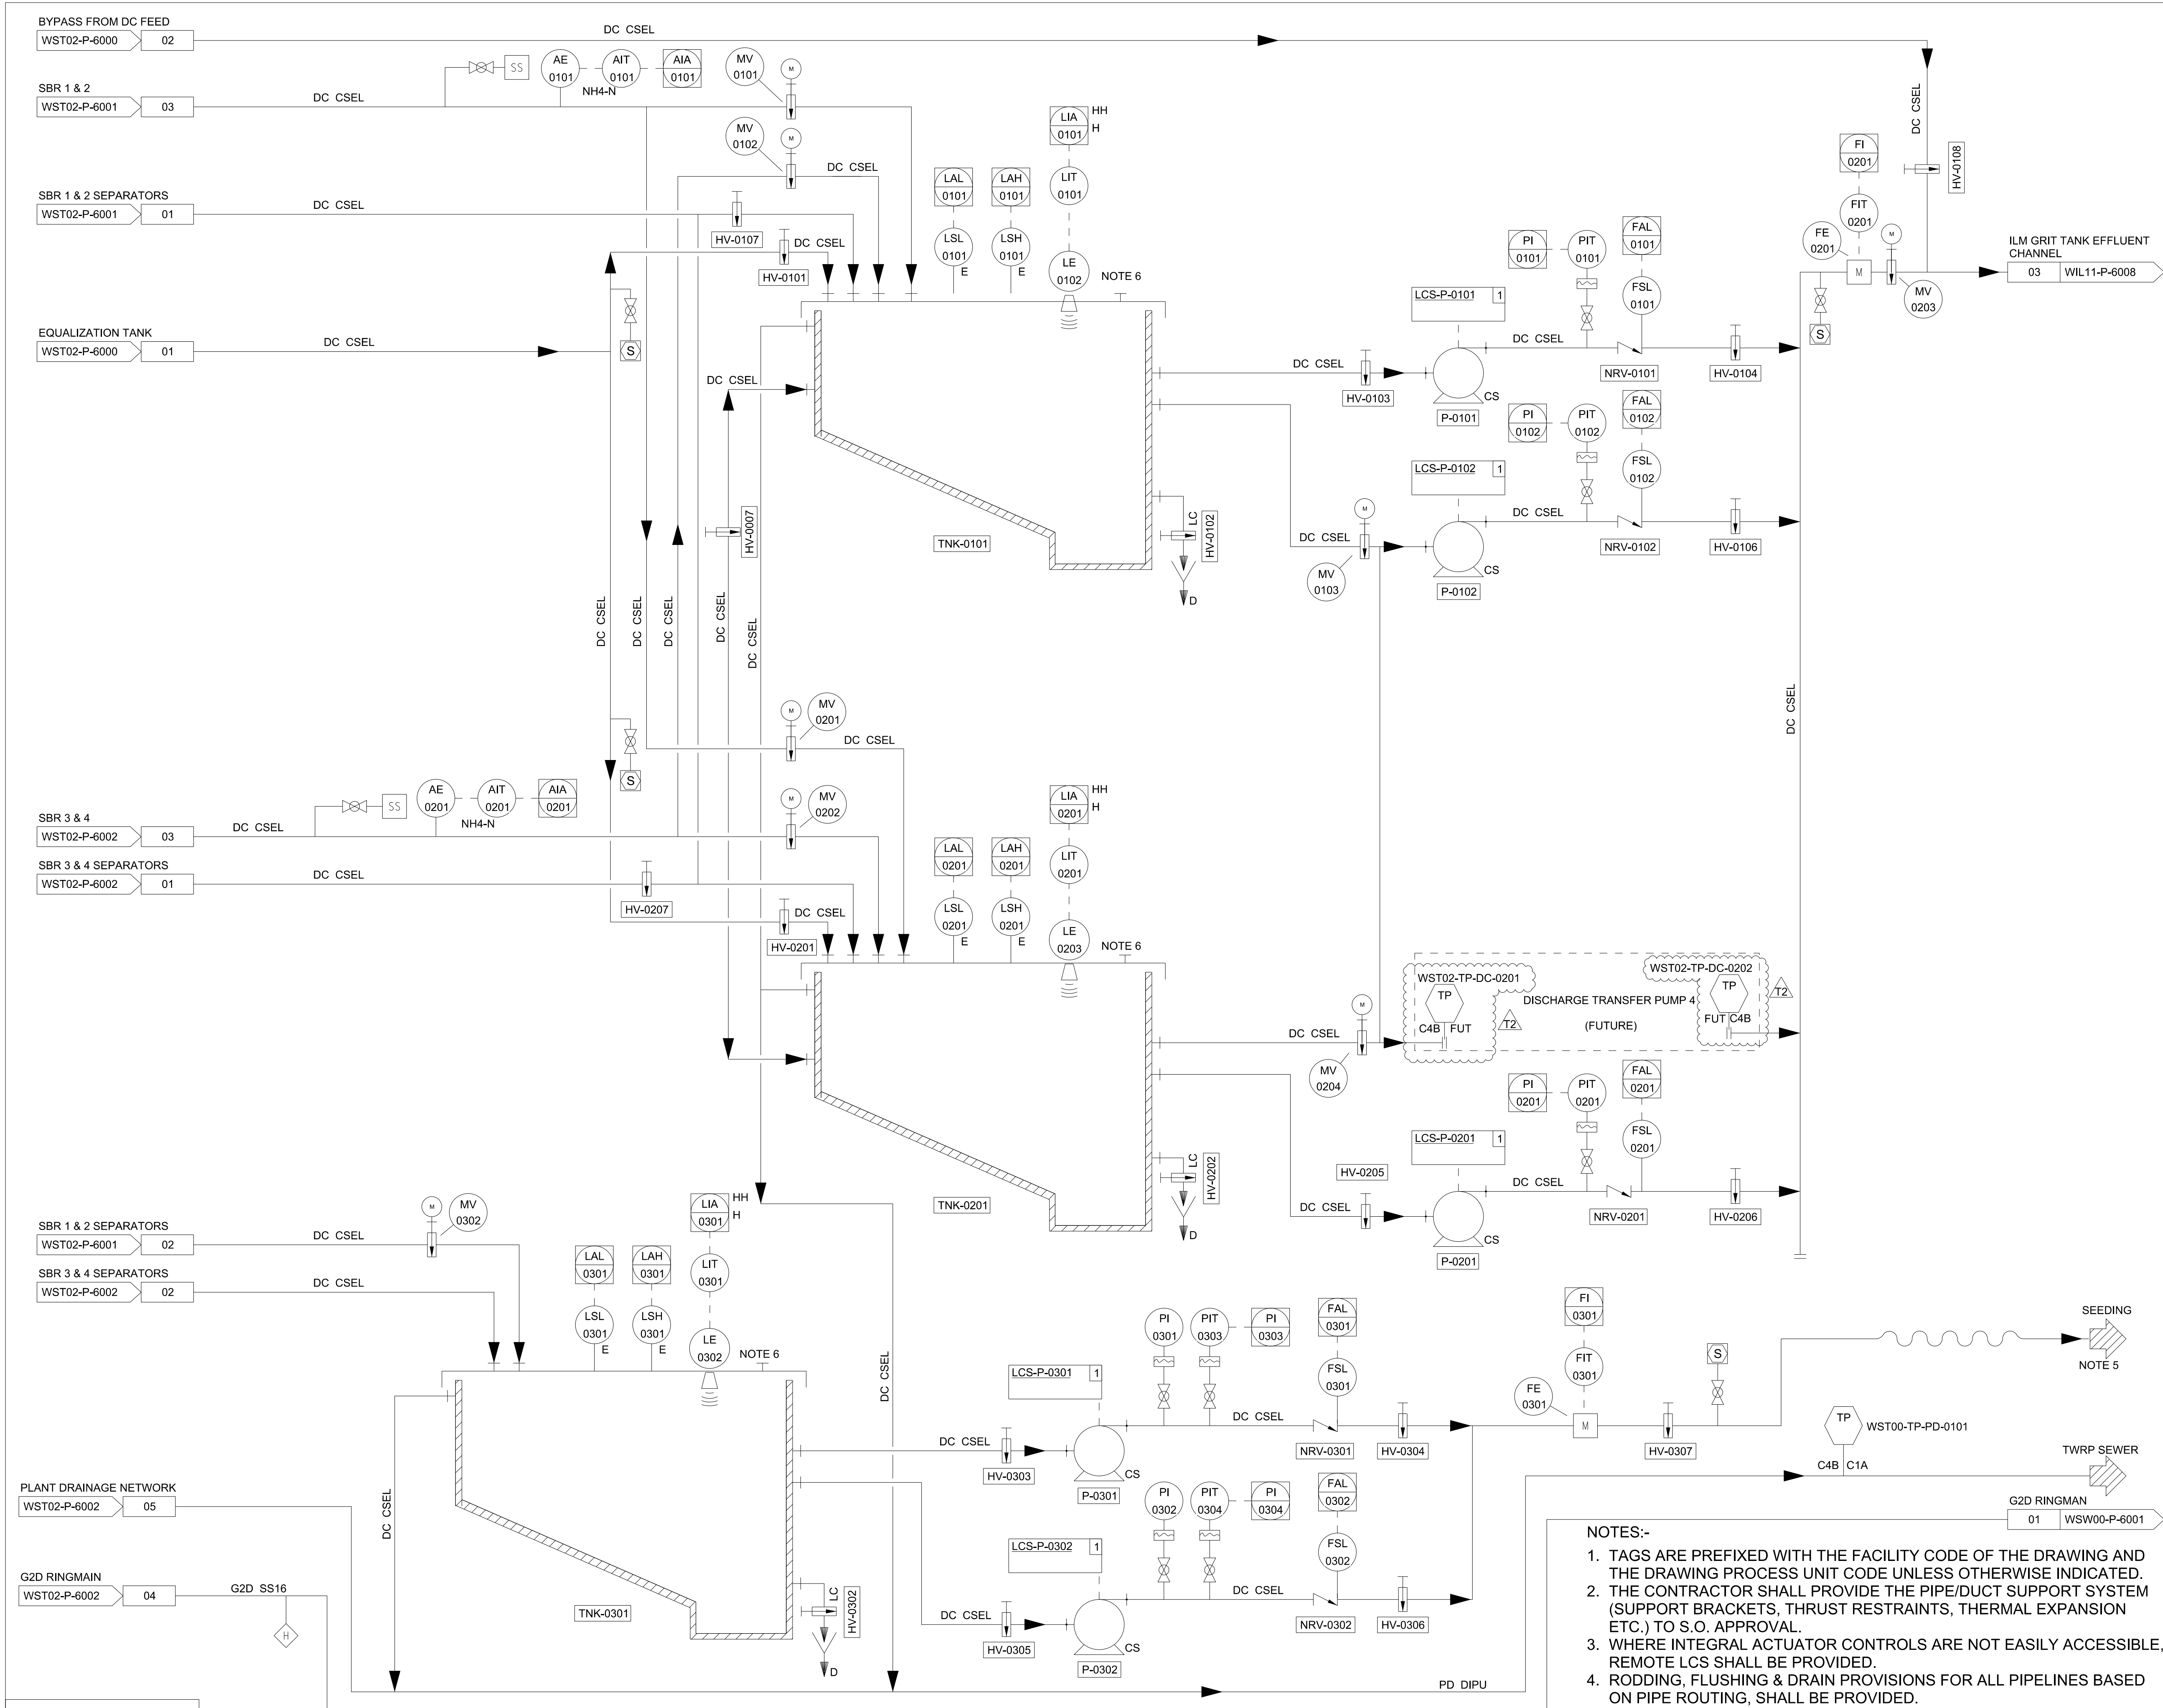

- NOTES:-
1. TAGS ARE PREFIXED WITH THE FACILITY CODE OF THE DRAWING AND THE DRAWING PROCESS UNIT CODE UNLESS OTHERWISE INDICATED.
 2. THE CONTRACTOR SHALL PROVIDE THE PIPE/DUCT SUPPORT SYSTEM (SUPPORT BRACKETS, THRUST RESTRAINTS, THERMAL EXPANSION ETC.) TO S.O. APPROVAL.
 3. WHERE INTEGRAL ACTUATOR CONTROLS ARE NOT EASILY ACCESSIBLE, REMOTE LCS SHALL BE PROVIDED.
 4. RODDING, FLUSHING & DRAIN PROVISIONS FOR ALL PIPELINES BASED ON PIPE ROUTING, SHALL BE PROVIDED.
 5. PROVISION FOR SEEDING TRANSFER THROUGH ROAD TANKER.
 6. DESIGN OF TANK SHALL ALLOW PROVISION FOR INSTALLATION OF FUTURE ODOUR COVERS AND CONNECTION TO FUTURE OCF
 7. ALL DRAINS SHALL BE ROUTED TO THE NEAREST TWRP SEWER MANHOLE.

TENDER

T2	25/11/22	ISSUED FOR TENDER C4B (2ND STAGE)	CN	GOT
T1	20/05/22	ISSUED FOR TENDER C4B	CN	GOT
REV	DATE	DESCRIPTION	REVIEWED	AUTHORISED

CLIENT:



PROGRAMME MANAGER:



PROJECT TITLE:
**TUAS WATER RECLAMATION PLANT (TWRP)
DTSS PHASE 2**

DRAWING TITLE
**P&ID
SIDESTREAM - N REMOVAL DISCHARGE
AND SLUDGE WET WELL
AND TRANSFER PUMPS**

DRAFTED: RSR	DESIGNED: KV	SHEET SIZE: A1
DRAFTING CHECK: ASR	DESIGN CHECK: CN	SCALE: NTS
DATE: 04/07/19	REVIEWED: CN	PBS: 131101
CONTRACT: -	DRAWING NUMBER: PUB-DTSS2-TWRP SHEET NUMBER: WST02-P-6003	REVISION: T2

THIS DRAWING IS COPYRIGHT