




VALVE SYMBOLS

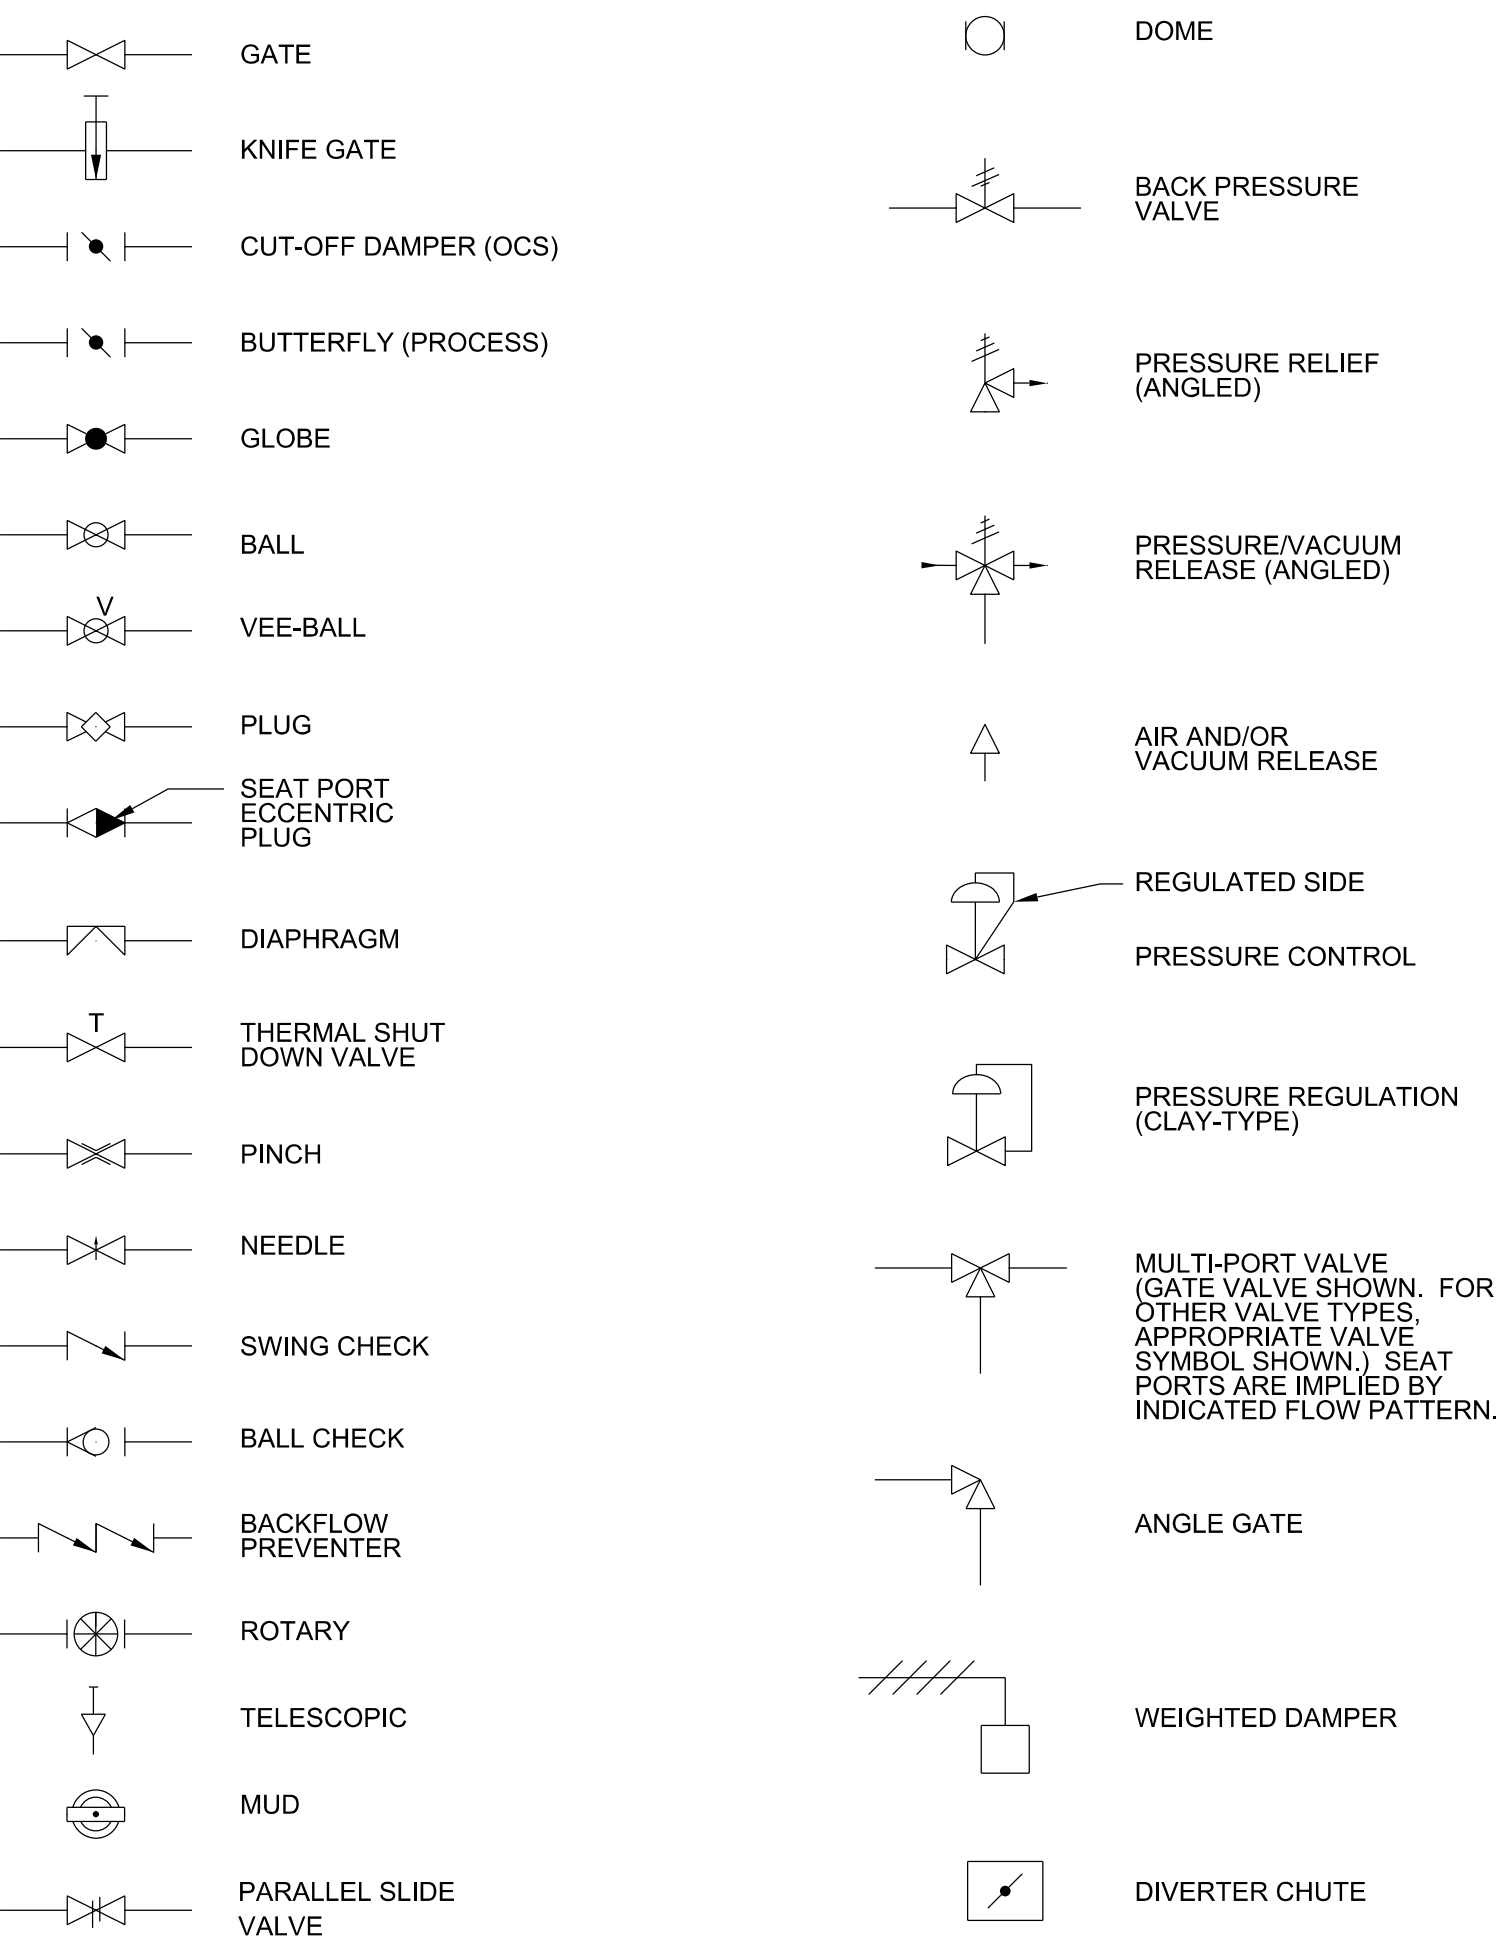

GATE SYMBOLS

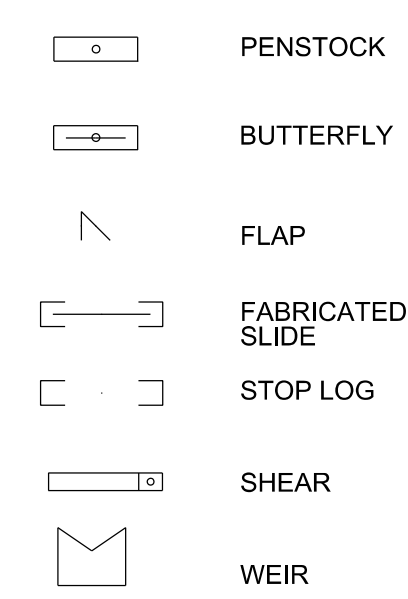


ACTUATOR SYMBOLS

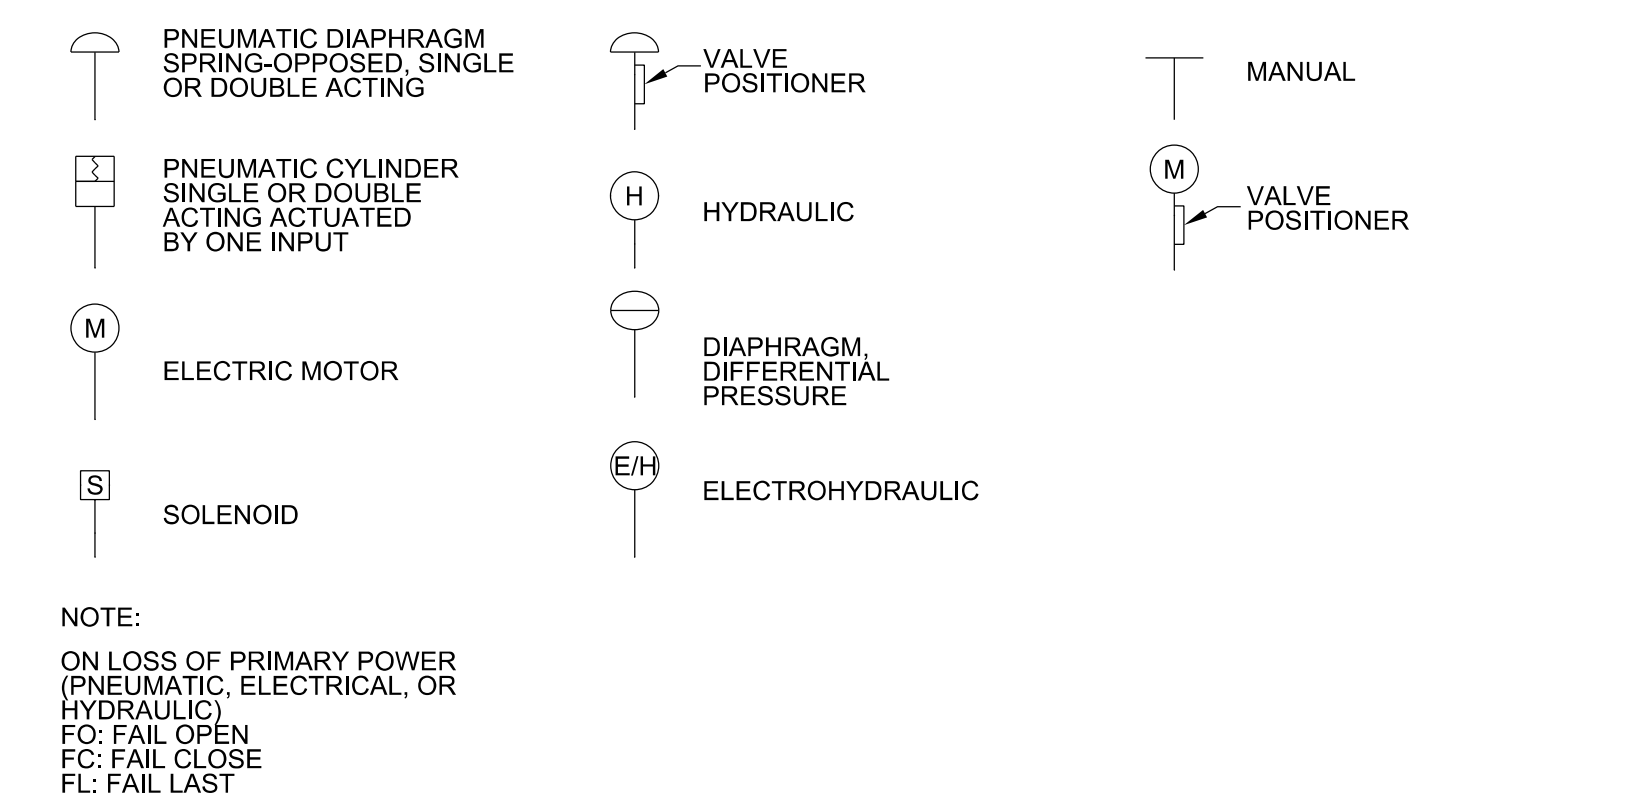


NOTE:
ON LOSS OF PRIMARY POWER (PNEUMATIC, ELECTRICAL, OR HYDRAULIC)
FO: FAIL OPEN
FC: FAIL CLOSE
FL: FAIL LAST

PRIMARY ELEMENT SYMBOLS

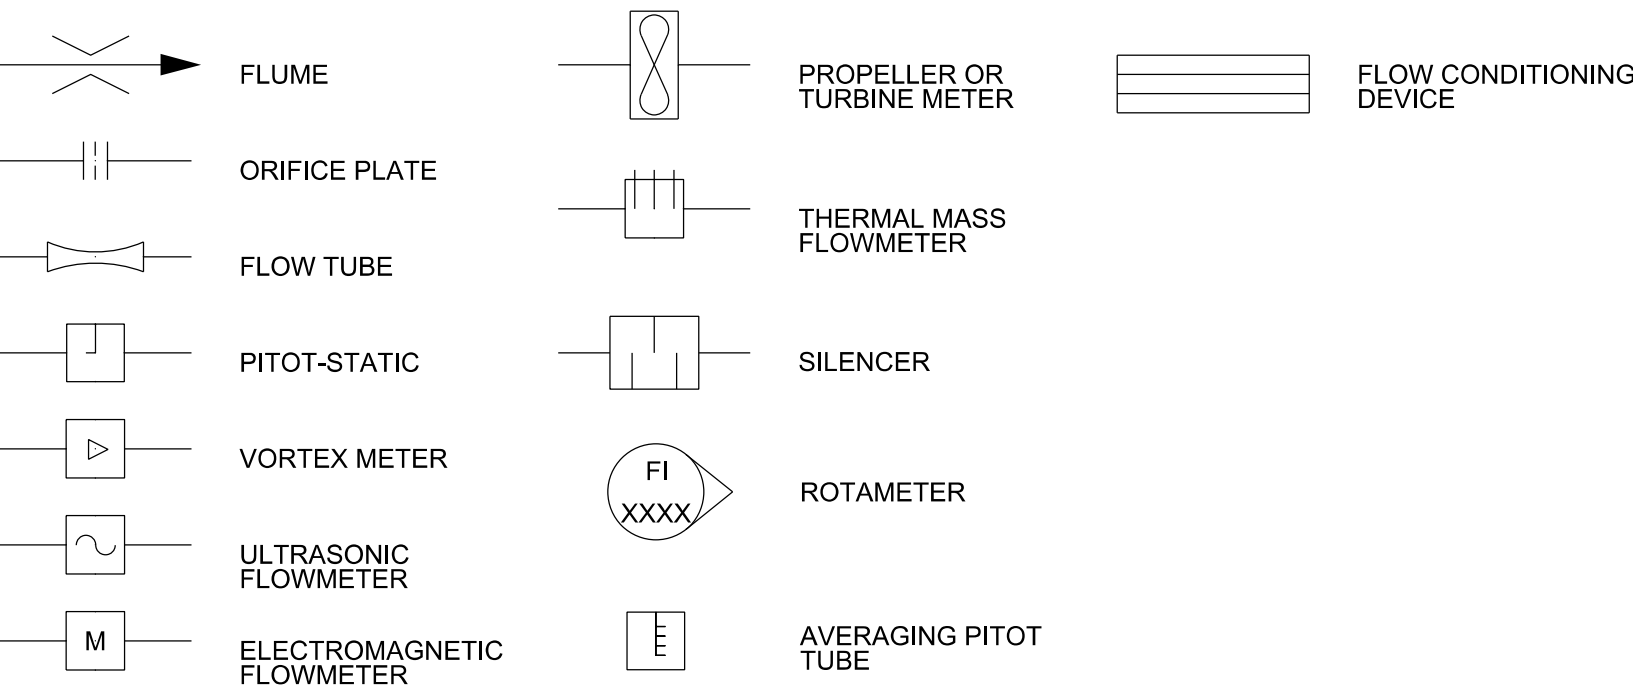

LEVEL INSTRUMENTS

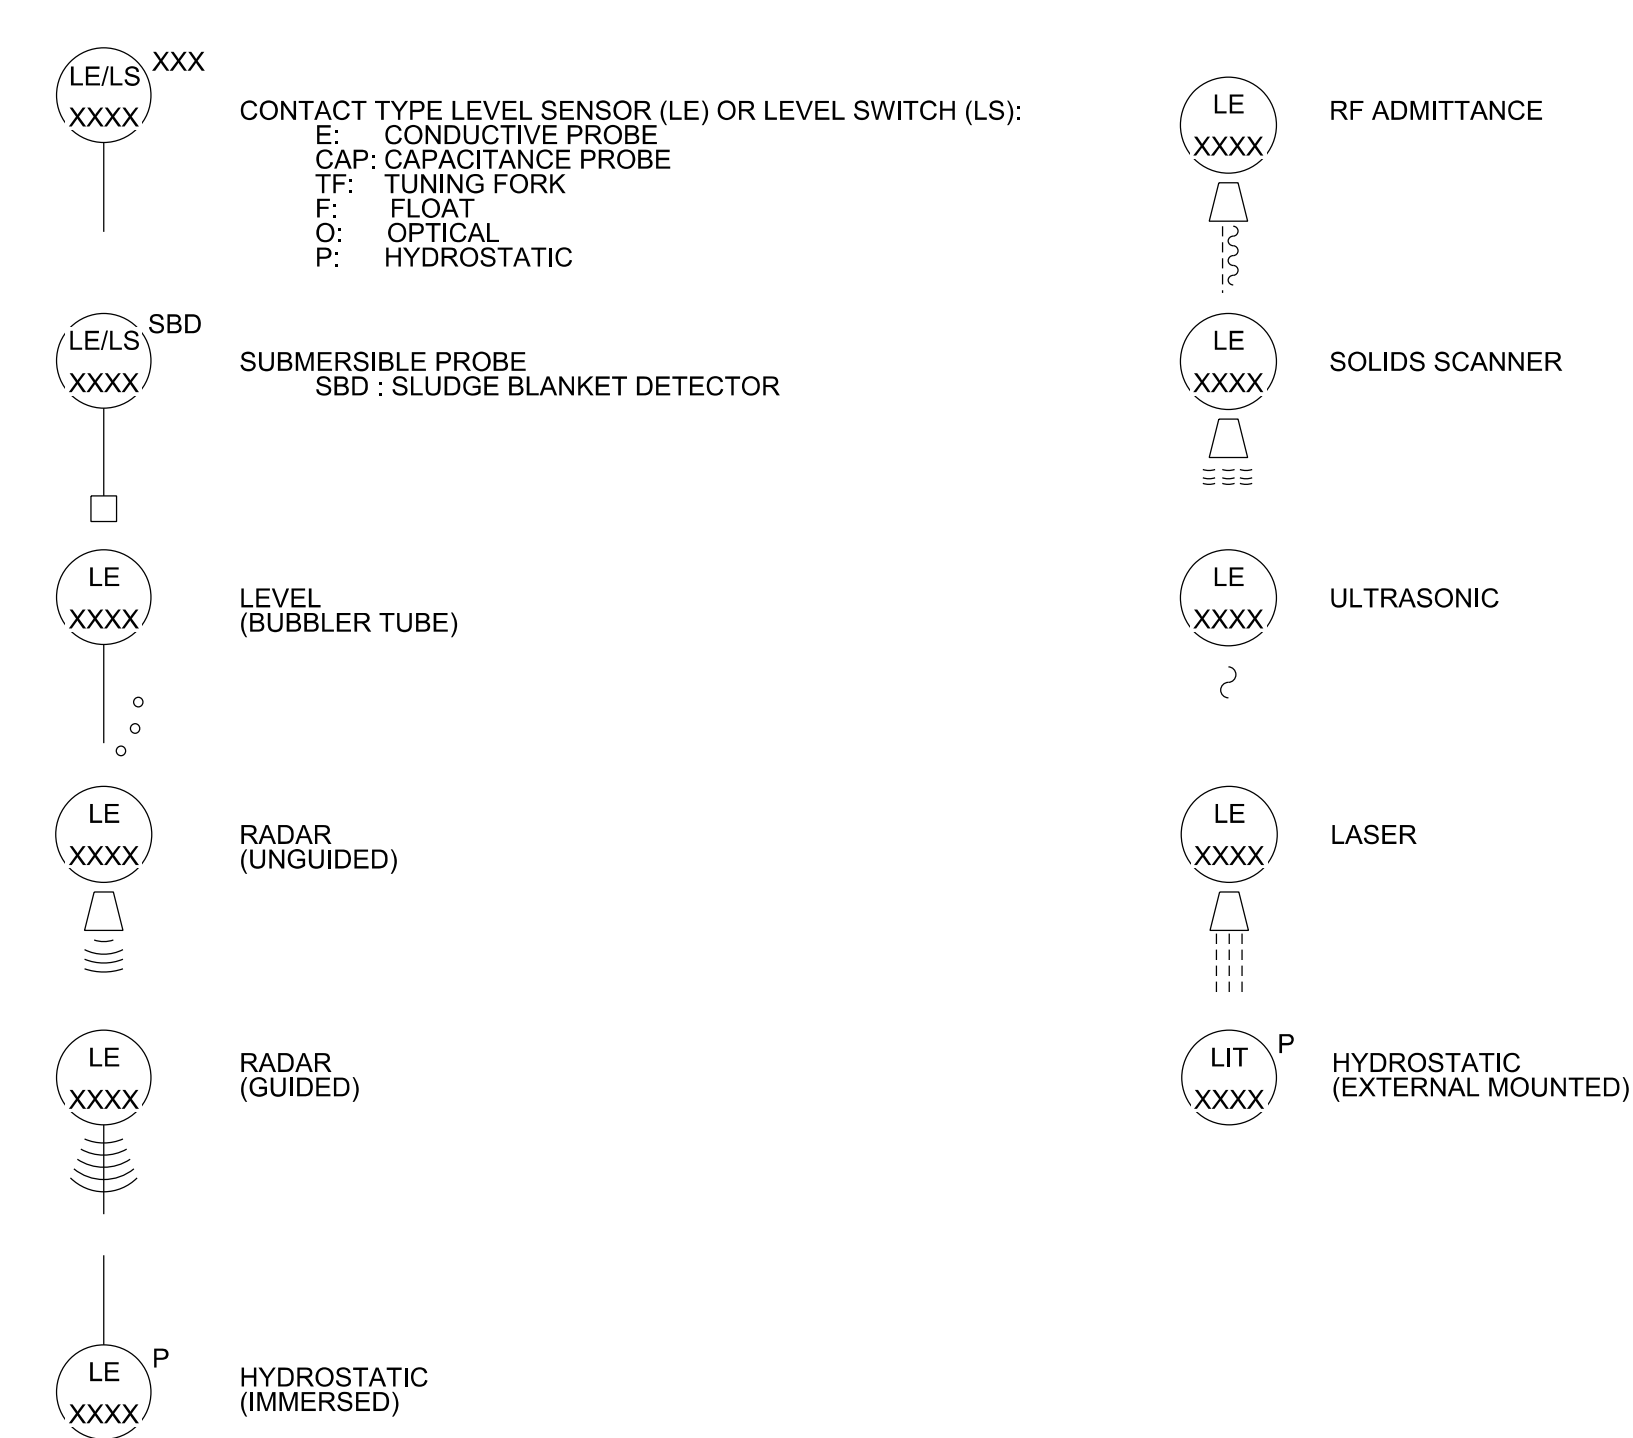

TENDER

T1 20/05/22	ISSUED FOR TENDER C4B	CN	GOT
T1 02/07/21	ISSUED FOR TENDER C3D2	CN	GOT
T1 18/12/20	ISSUED FOR TENDER C3B1	CN	GOT
T1 23/07/20	ISSUED FOR TENDER C2B	CN	GOT
T1 24/04/20	ISSUED FOR TENDER C3A	CN	GOT
T1 08/04/20	ISSUED FOR TENDER C3D1	CN	GOT
REV	DATE	DESCRIPTION	REVIEWED /AUTHORISED

CLIENT:

 **PUB**

SINGAPORE'S NATIONAL WATER AGENCY

PROGRAMME MANAGER:

 **binnies AECOM**

A JOINT VENTURE DELIVERING THE DTSS2 PROJECT

CONSULTANT:

 **Jacobs**

CH2M HILL Singapore Pte Ltd

PROJECT TITLE:

TUAS WATER RECLAMATION PLANT (TWRP)
DTSS PHASE 2

DRAWING TITLE

P&ID LEGEND SYMBOLS
SHEET 1 OF 2

DRAFTED: MW	DESIGNED: SYC	SHEET SIZE: A1
DRAFTING CHECK: DW	DESIGN CHECK: JL	SCALE: NTS
DATE: 29/11/17	REVIEWED: CN	PBS: 131101
CONTRACT:	DRAWING NUMBER: PUB-DTSS2-TWRP	
-	SHEET NUMBER: WSW00-P-0005	REVISION: T1

THIS DRAWING IS COPYRIGHT