



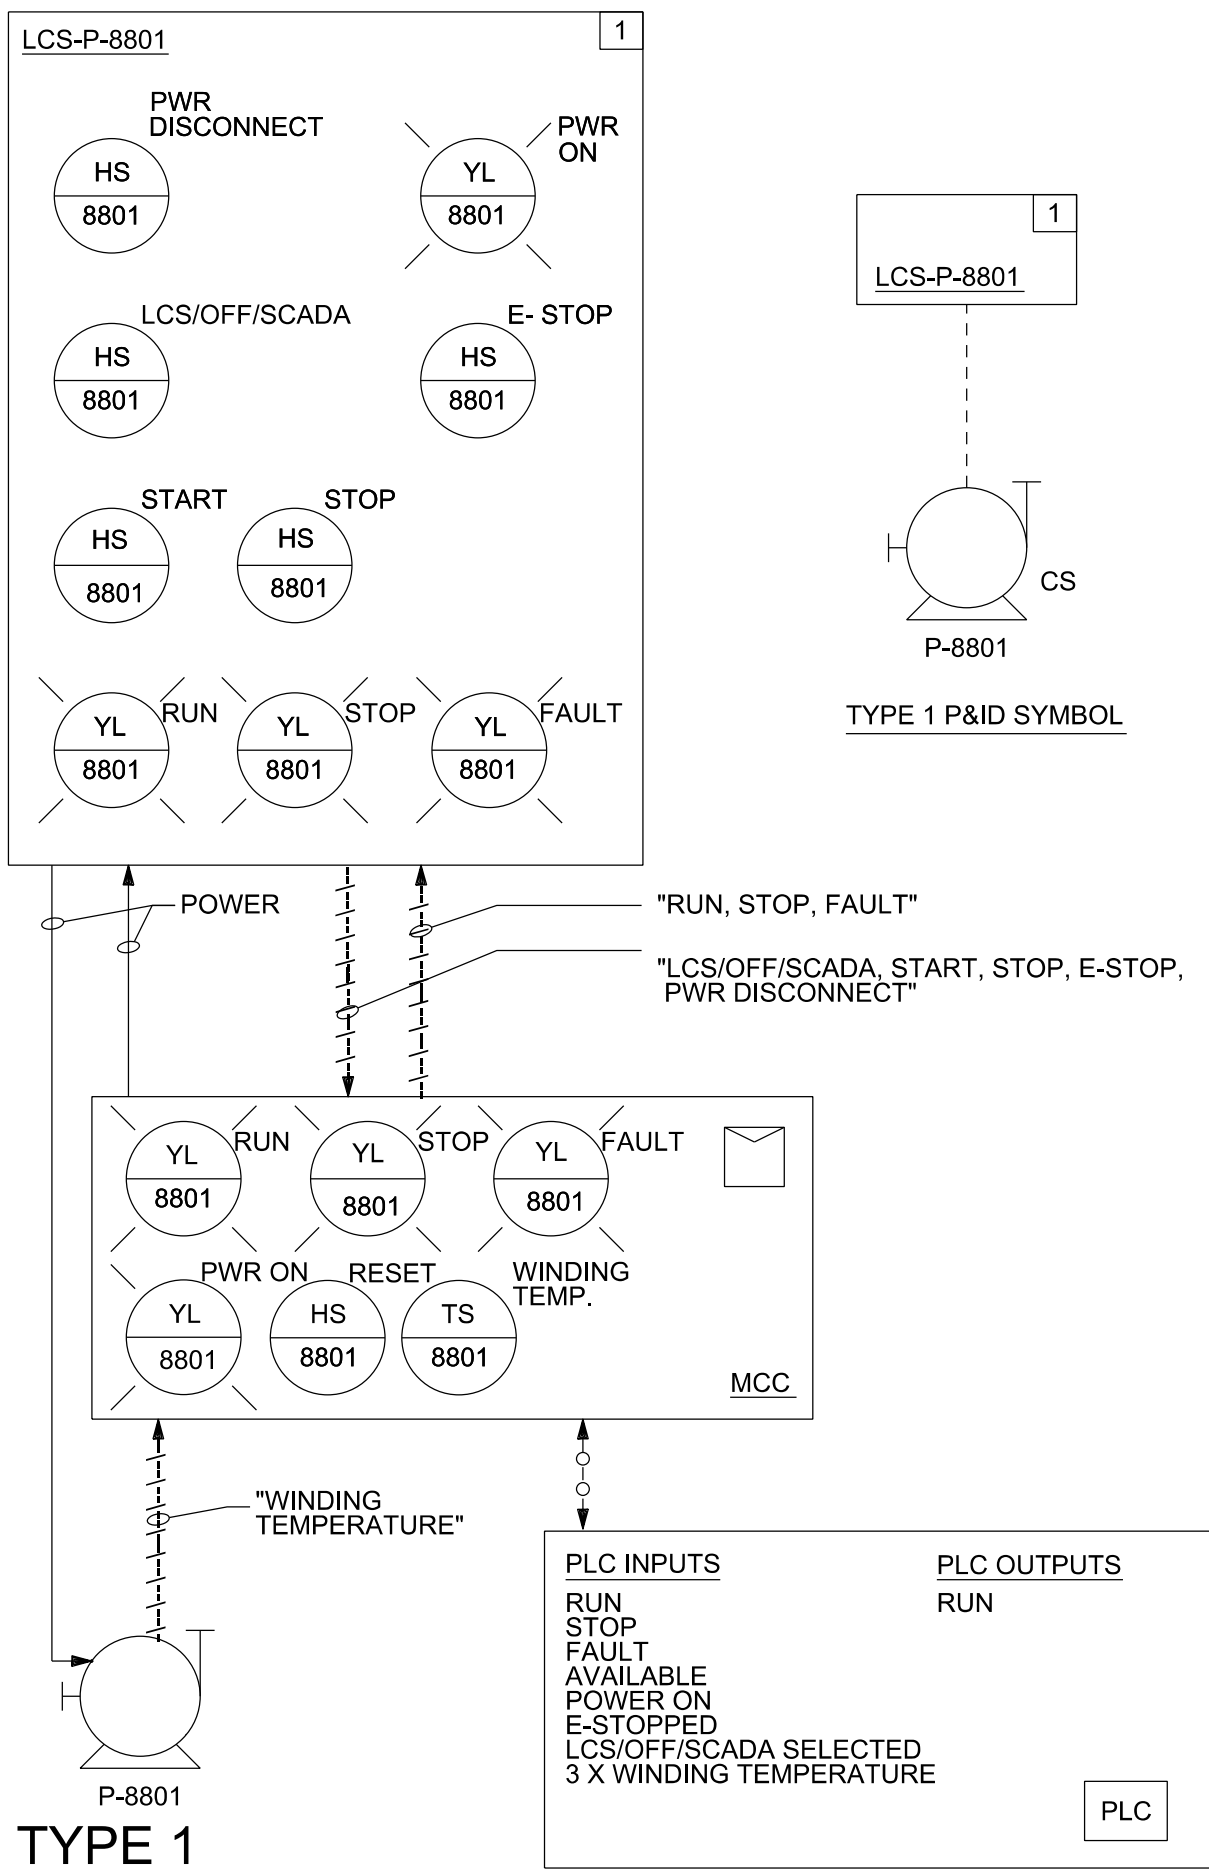


TYPE 1

FIXED SPEED (DOL / Y-Δ) WITH WINDING TEMPERATURE LV MOTOR CONTROL, FOR MOTORS ≤ 75 kW

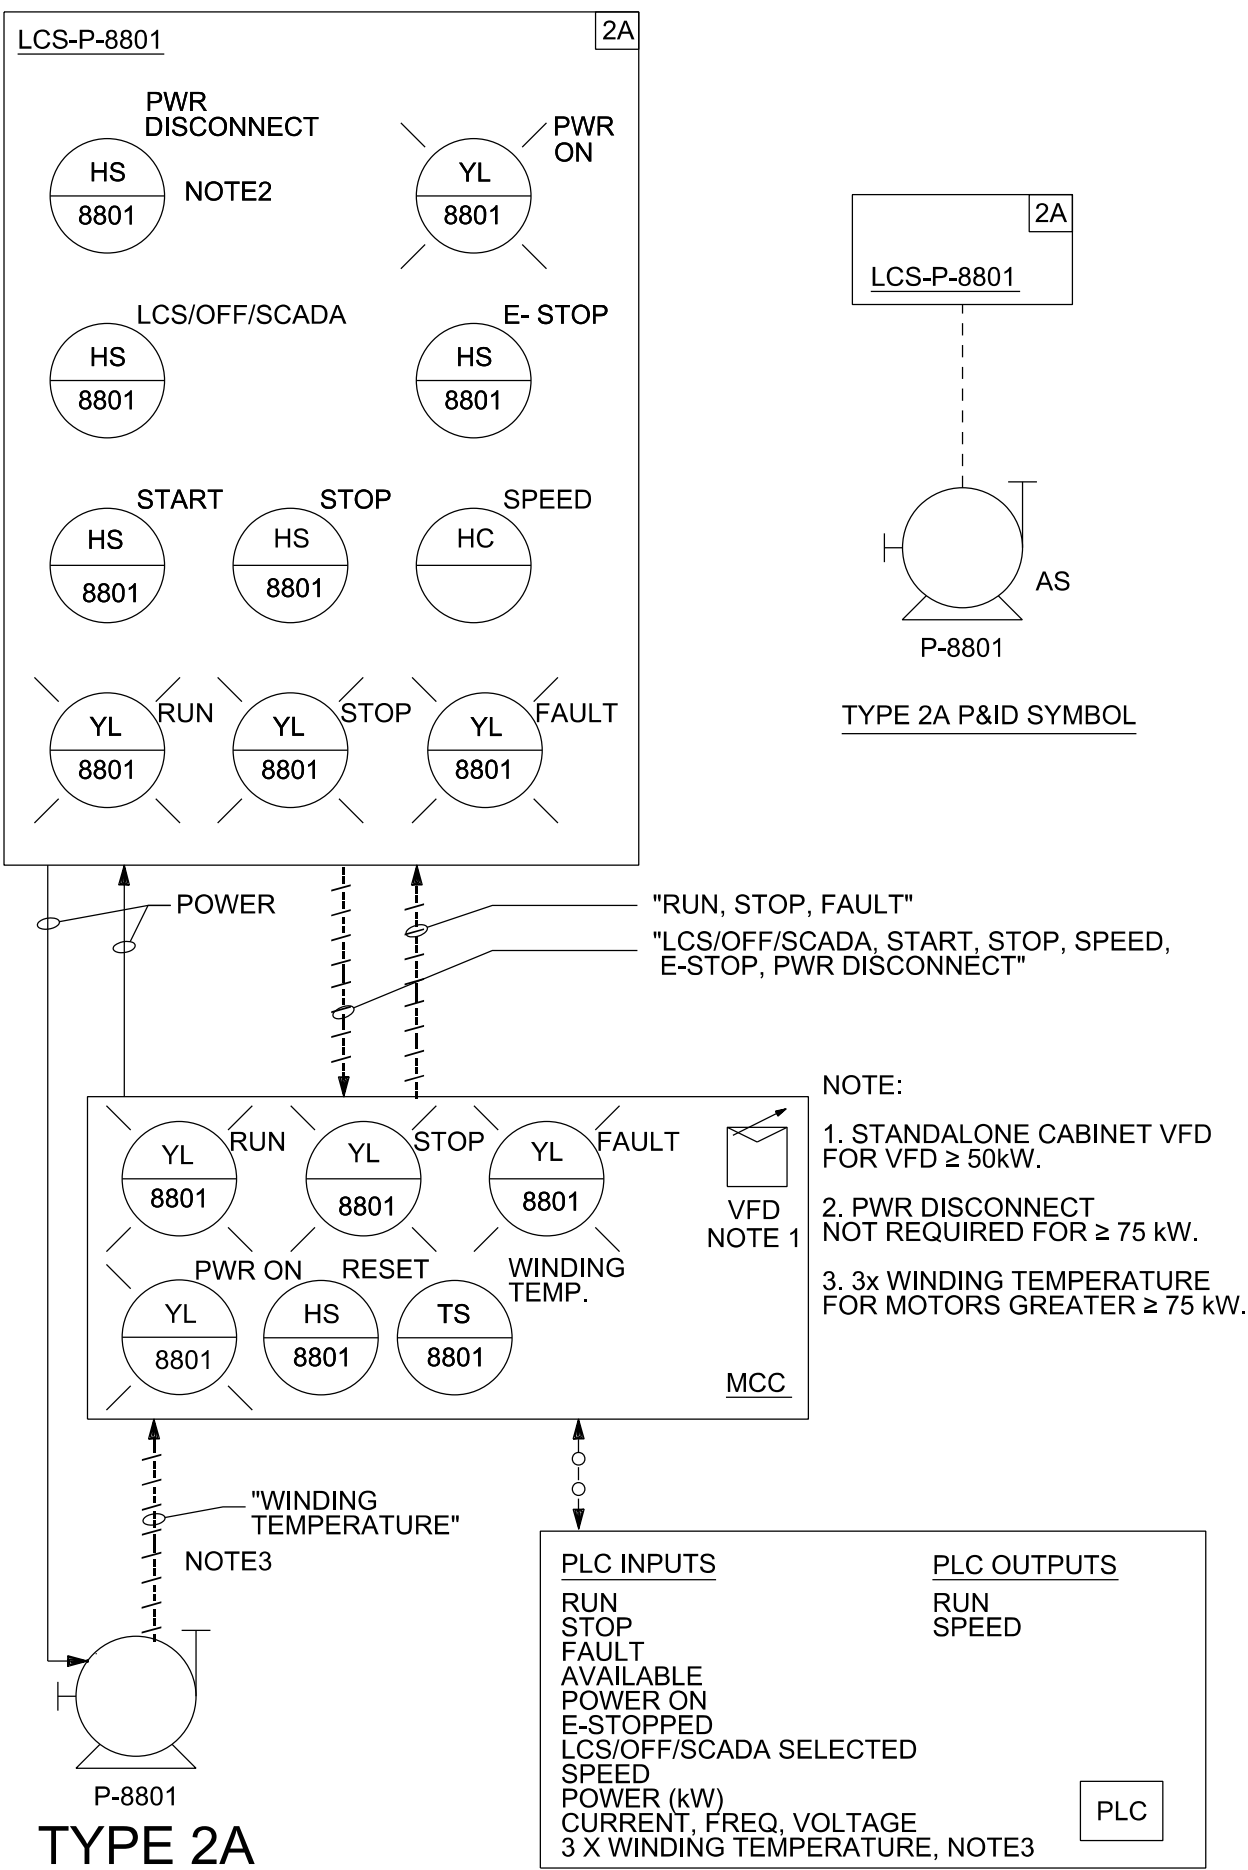


TYPE 2A

ADJUSTABLE SPEED (VFD) WITH WINDING TEMPERATURE LV MOTOR CONTROL, FOR MOTORS ≤ 75 kW

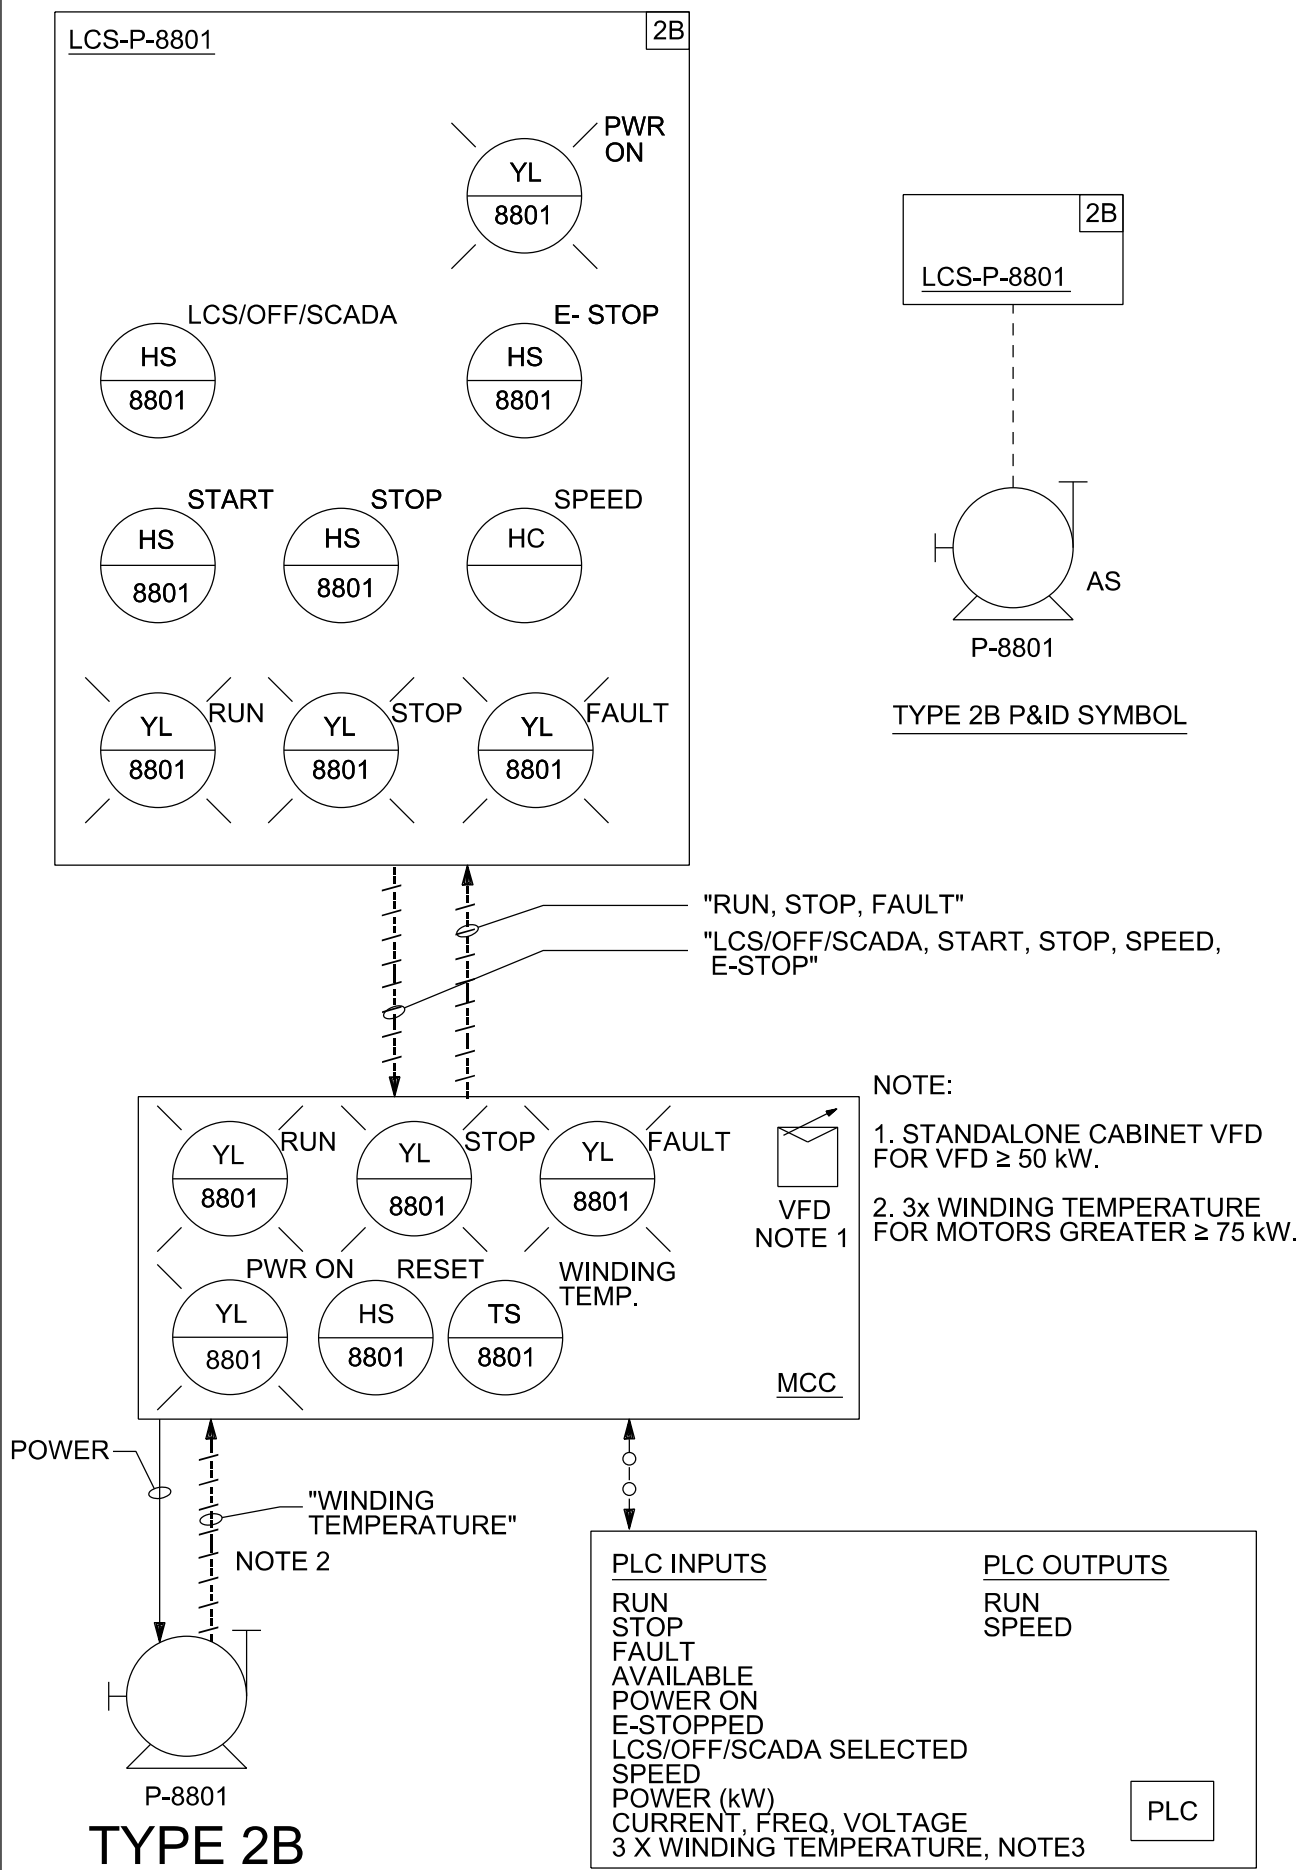


TYPE 2B

ADJUSTABLE SPEED (VFD) WITH WINDING TEMPERATURE LV MOTOR CONTROL, FOR MOTORS > 75 kW AND ≤ 200 kW

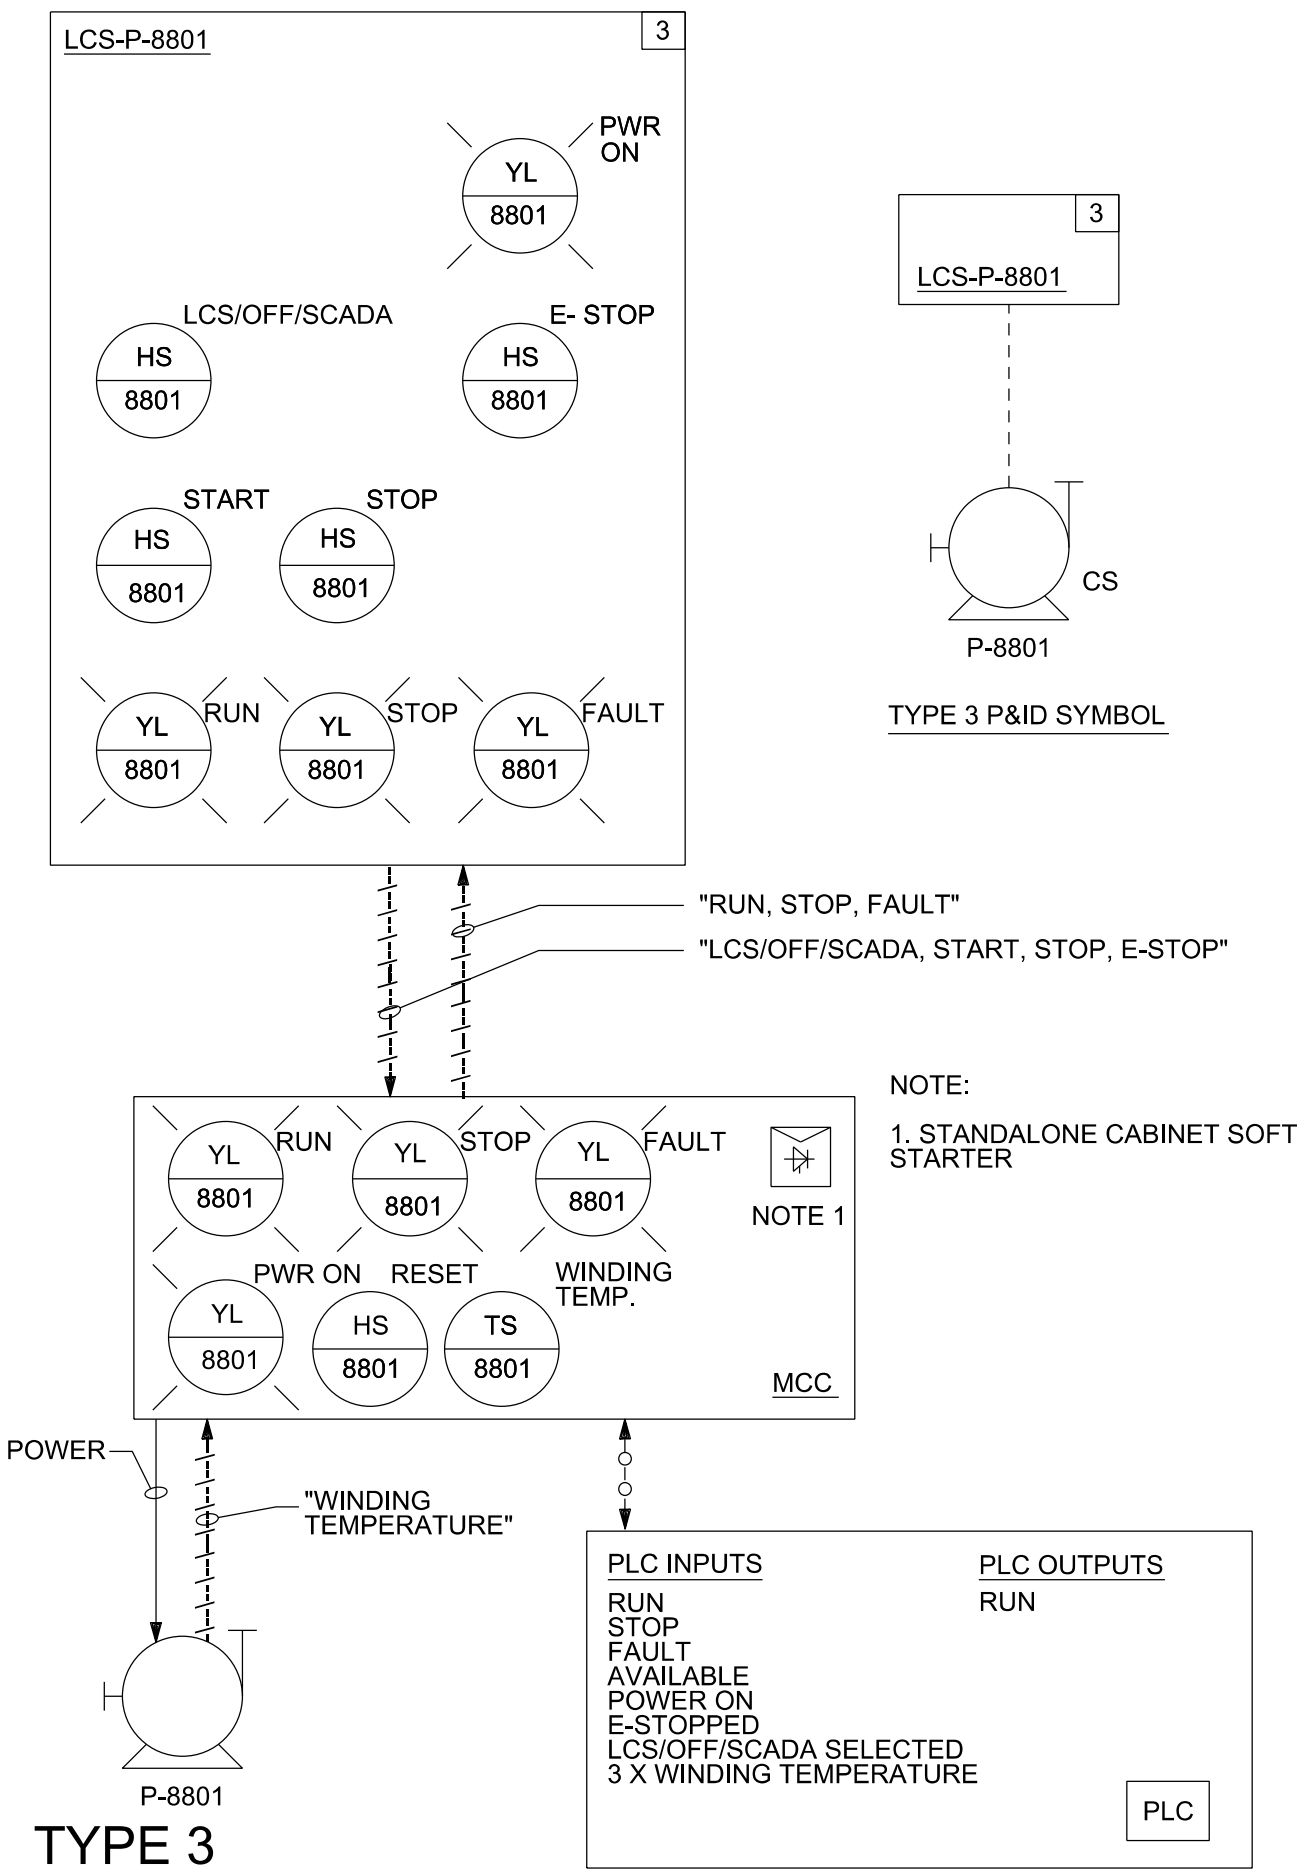


TYPE 3

FIXED SPEED (SOFT STARTER) WITH WINDING TEMPERATURE LV MOTOR CONTROL FOR MOTORS ≤ 200 kW

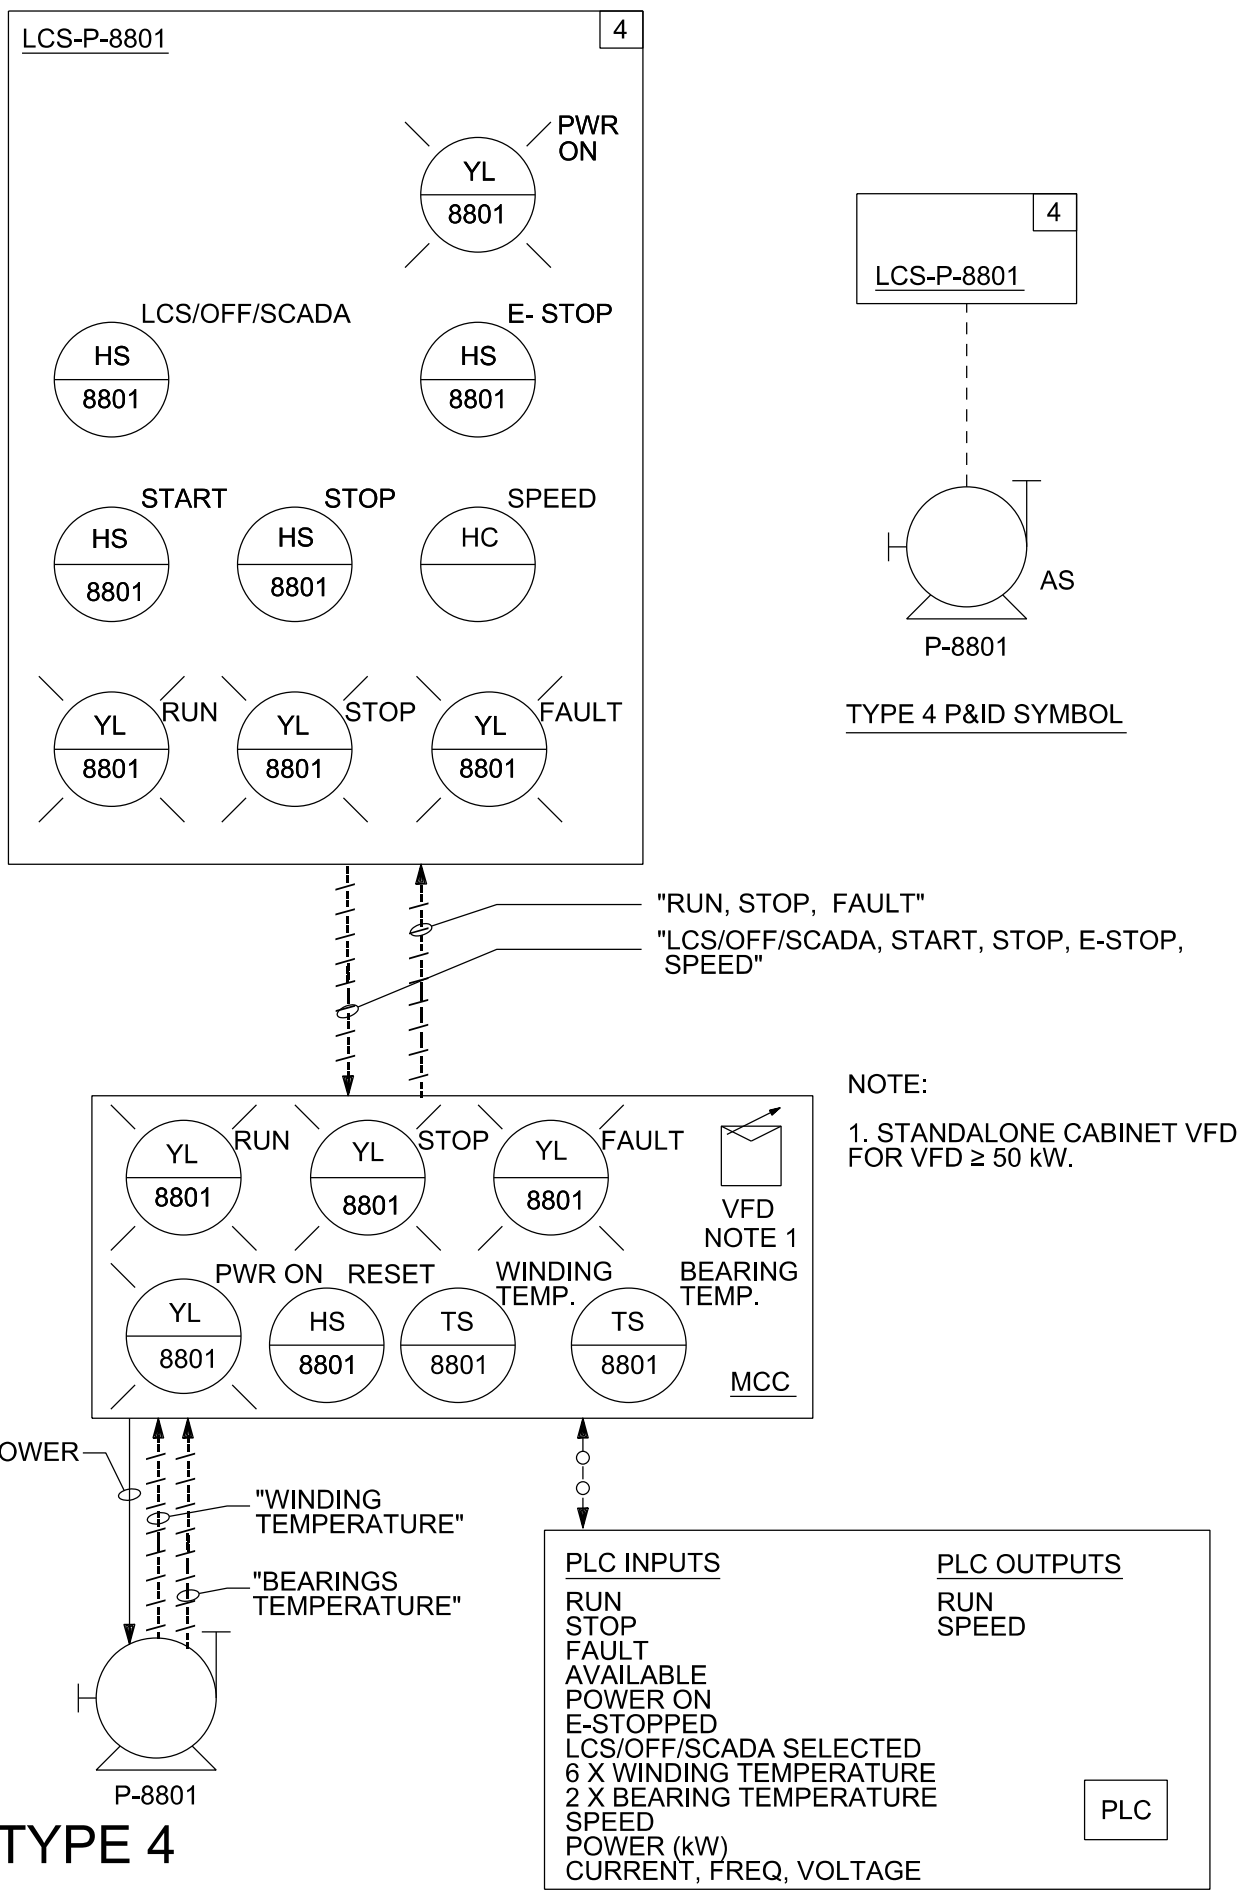


TYPE 4

ADJUSTABLE SPEED (VFD) WITH WINDING/ BEARING TEMPERATURE LV MOTOR CONTROL FOR MOTORS > 200 kW AND ≤ 450 kW

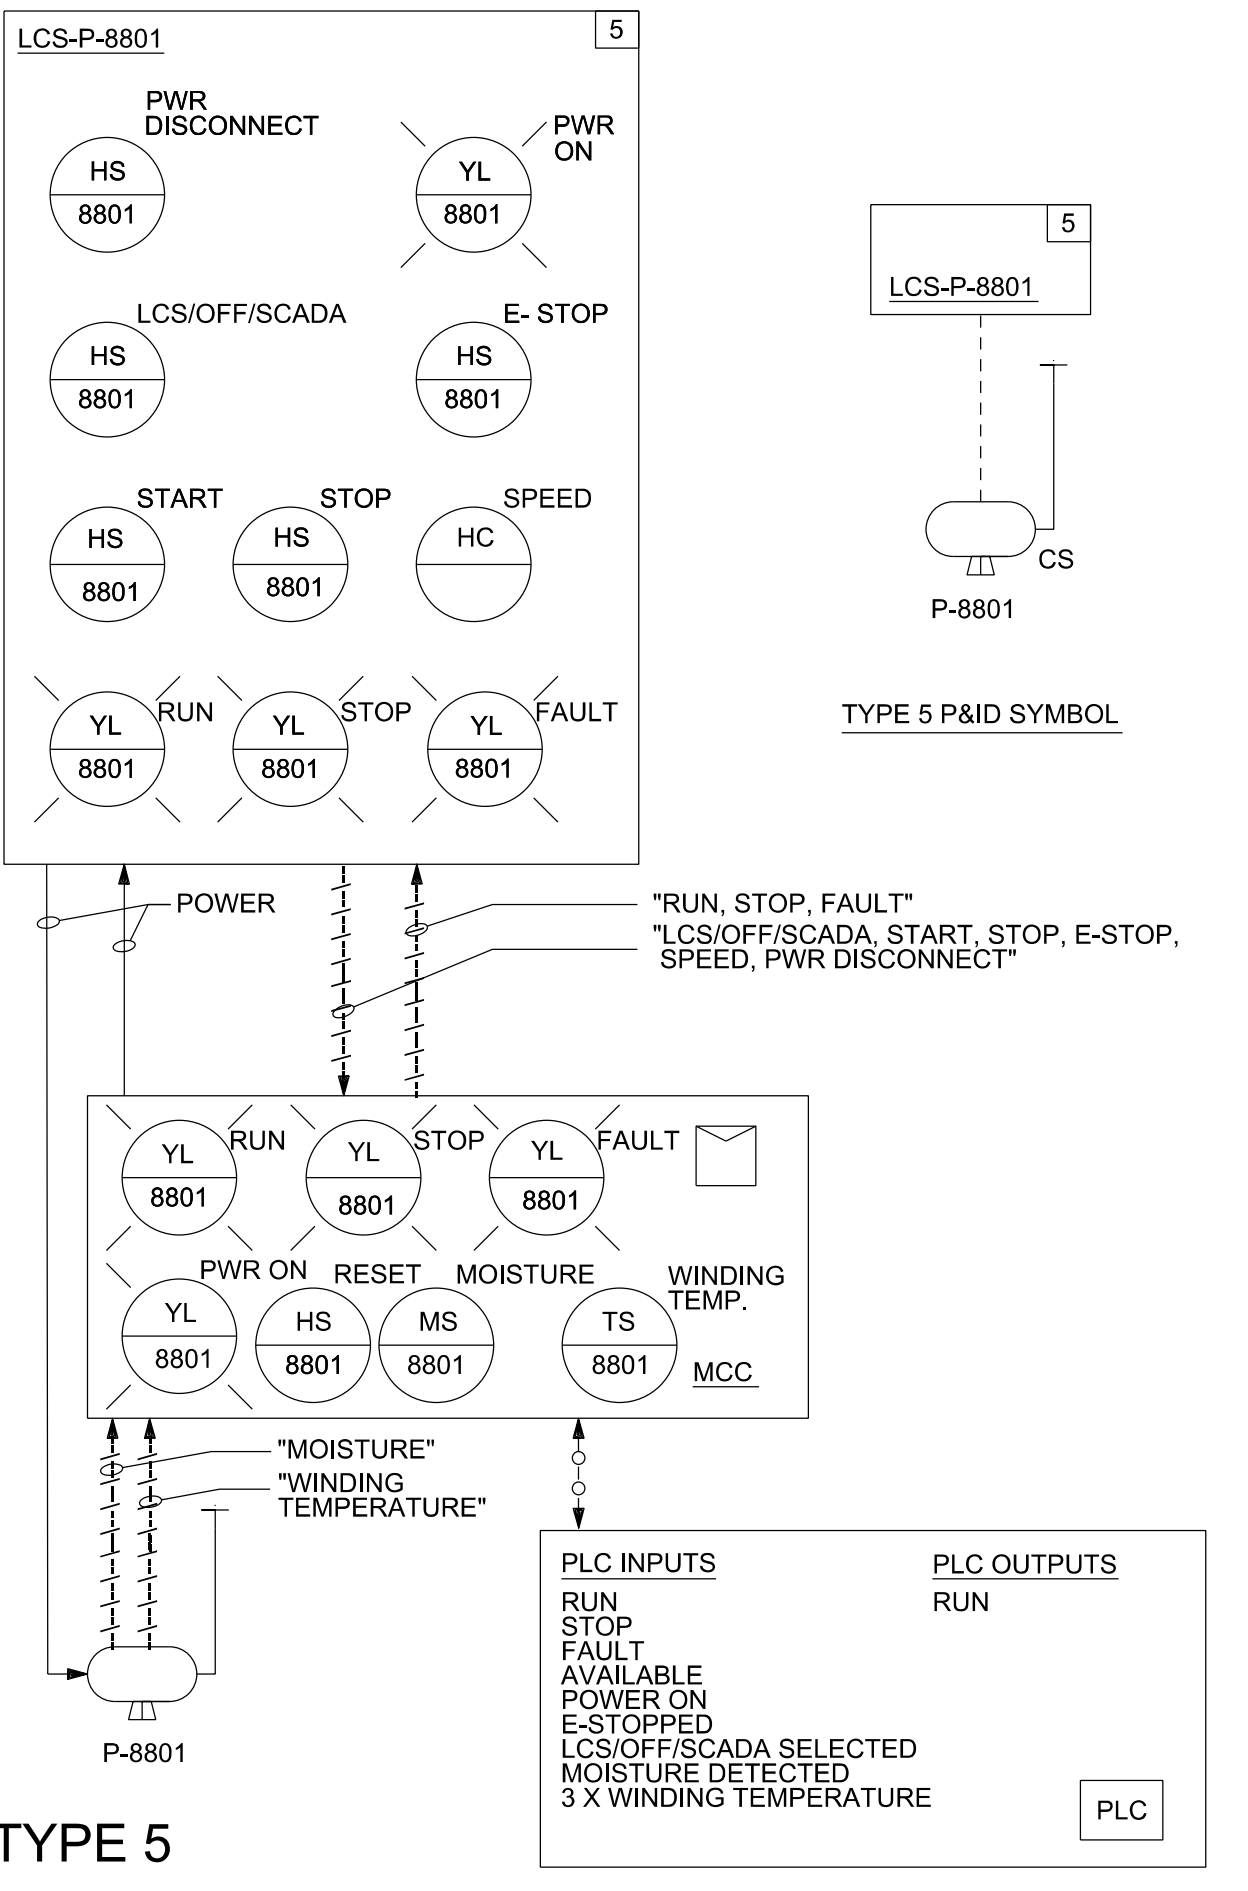


TYPE 5

SUBMERSIBLE FIXED SPEED (DOL/Y-D) WITH WINDING TEMPERATURE LV MOTOR CONTROL, FOR MOTORS ≤ 75 kW

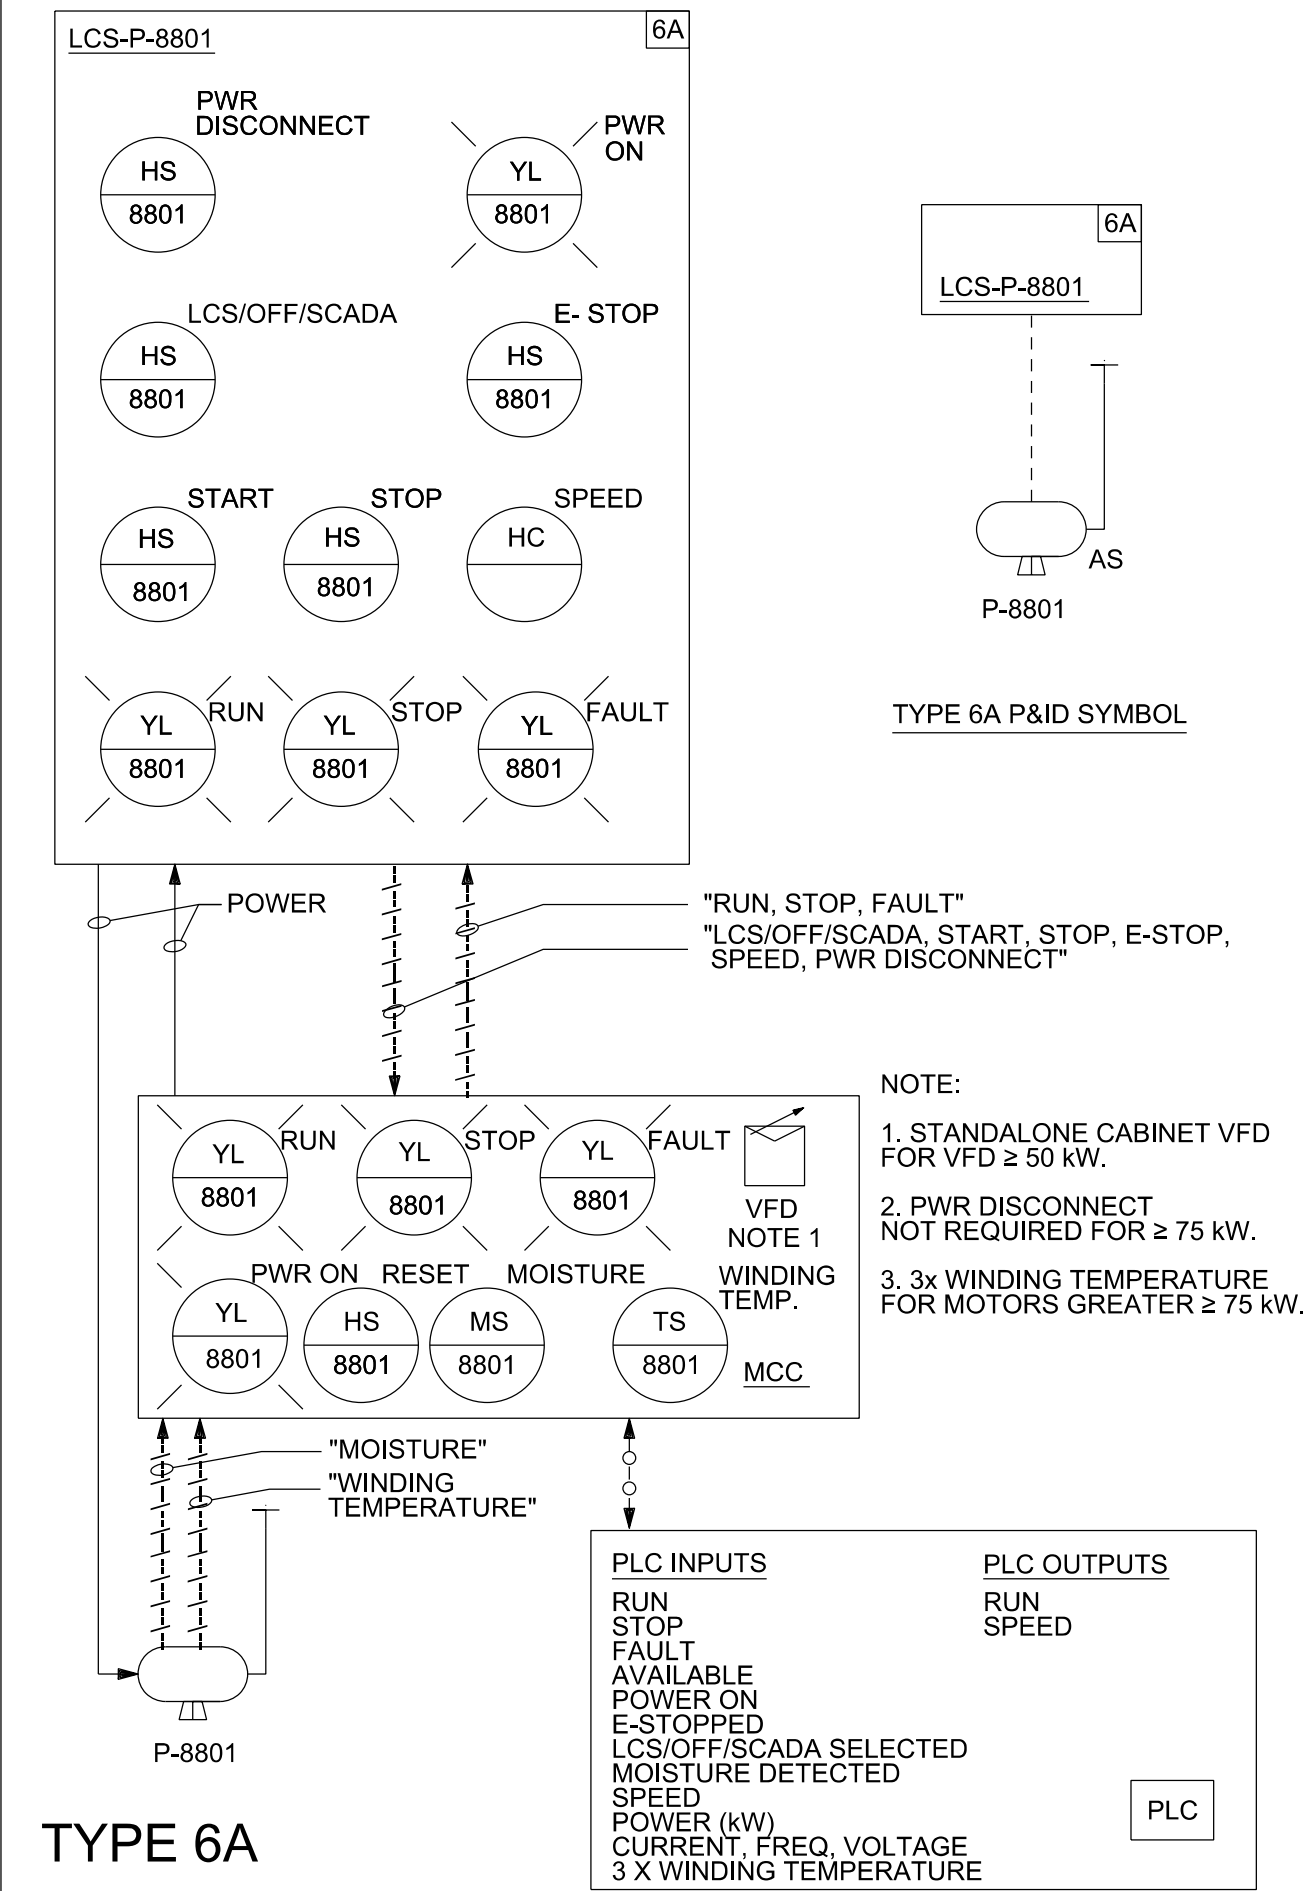

TYPE 6A

SUBMERSIBLE ADJUSTABLE SPEED WITH WINDING TEMPERATURE LV MOTOR CONTROL, FOR MOTORS ≤ 75 kW

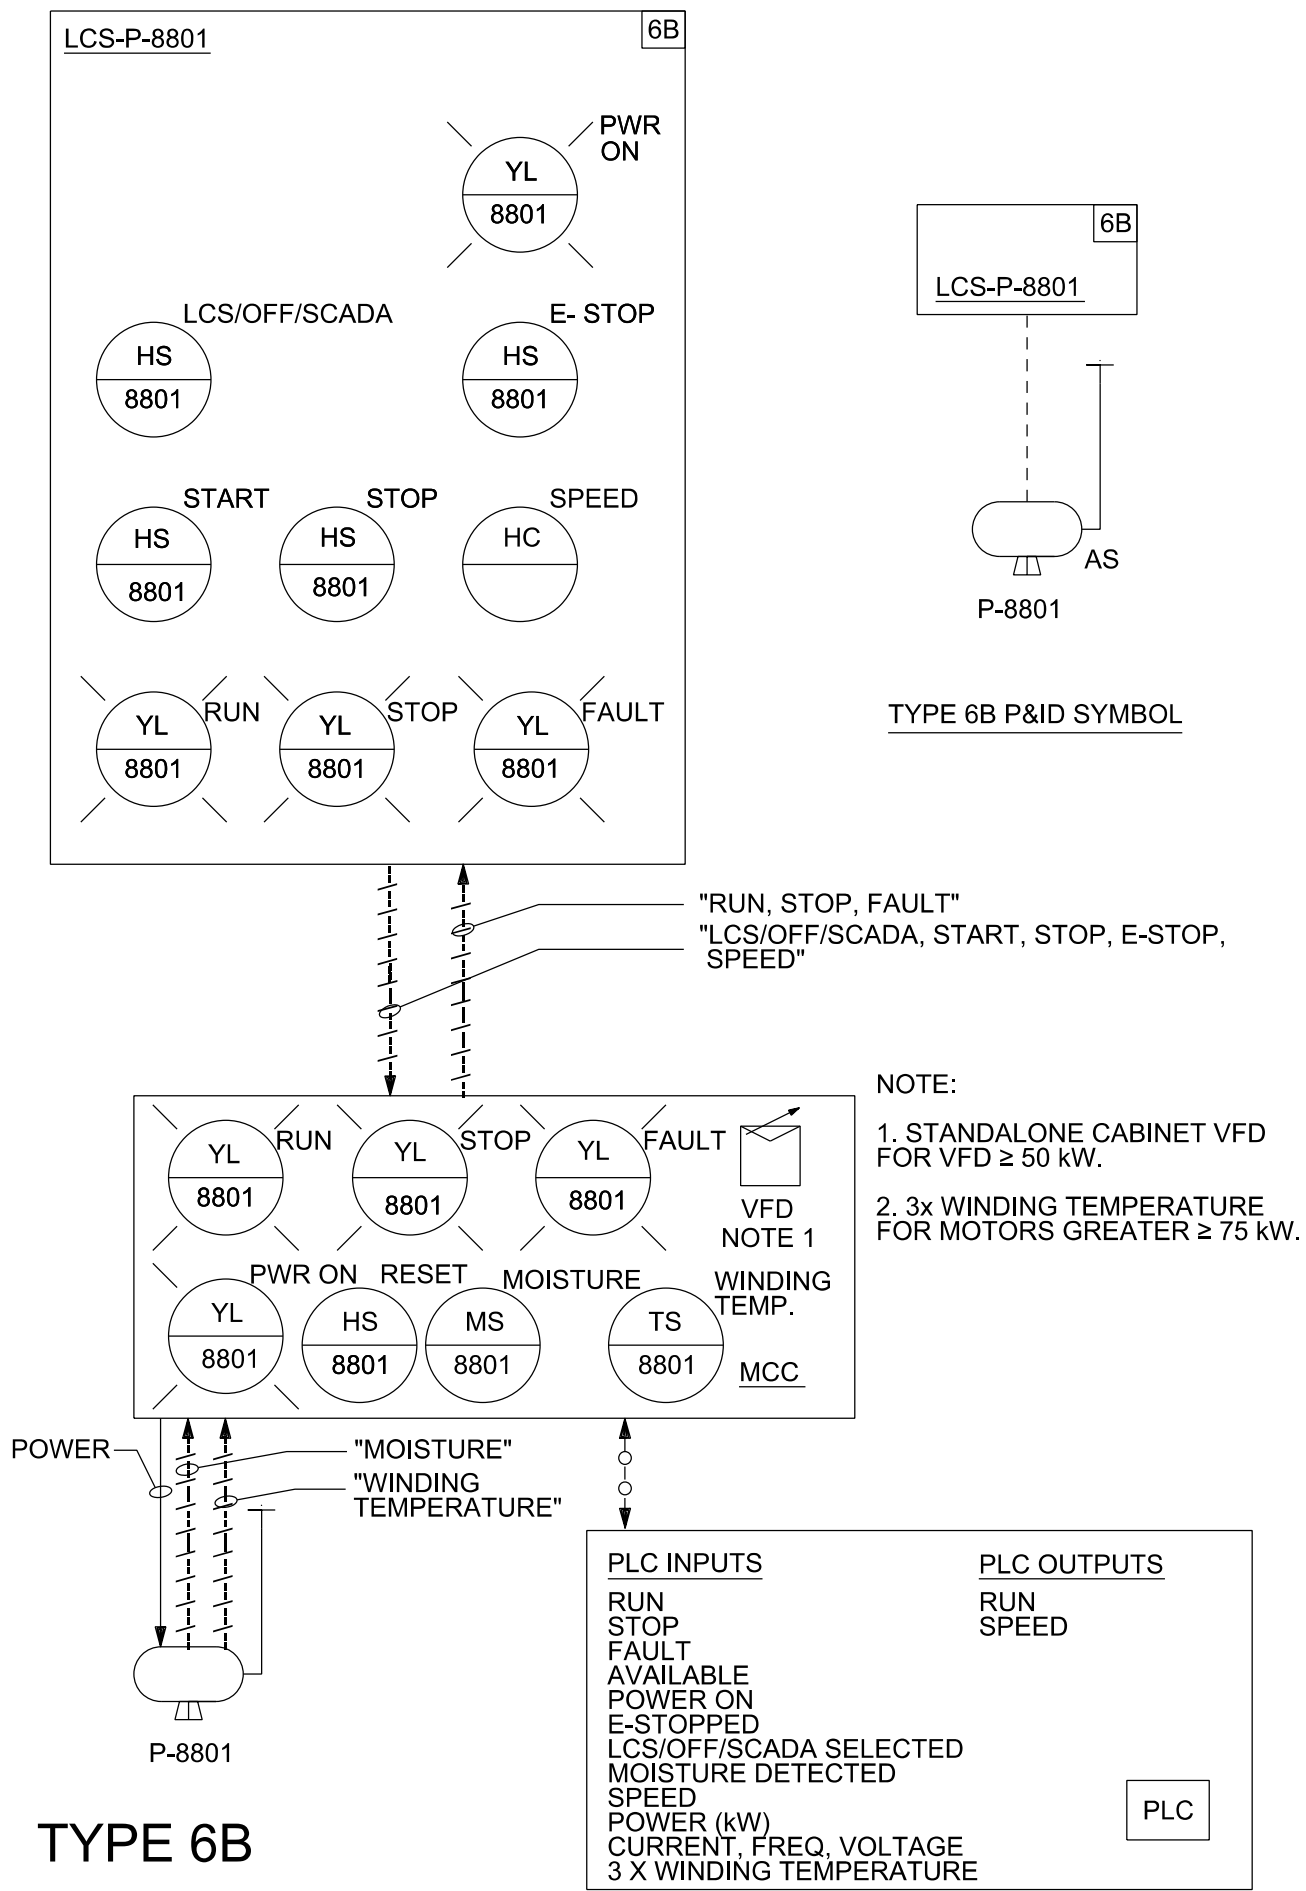

TYPE 6B

SUBMERSIBLE ADJUSTABLE SPEED WITH WINDING TEMPERATURE LV MOTOR CONTROL, FOR MOTORS > 75 kW AND ≤ 200 kW

NOTES:

1. STANDARD LCS TYPICAL, MAY BE USED FOR ANY EQUIPMENT. PUMP SYMBOL INDICATIVE ONLY.

TENDER

T1 20/05/22	ISSUED FOR TENDER C4B	CN	GOT
T1 02/07/21	ISSUED FOR TENDER C3D2	CN	GOT
T1 18/12/20	ISSUED FOR TENDER C3B1	CN	GOT
T1 23/07/20	ISSUED FOR TENDER C2B	CN	GOT
T1 24/04/20	ISSUED FOR TENDER C3A	CN	GOT
T1 08/04/20	ISSUED FOR TENDER C3D1	CN	GOT
REV	DATE	DESCRIPTION	REVIEWED / AUTHORISED

CLIENT:



PROGRAMME MANAGER:



A JOINT VENTURE DELIVERING THE DTSS2 PROJECT

CONSULTANT:



CH2M HILL Singapore Pte Ltd

PROJECT TITLE:

TUAS WATER RECLAMATION PLANT (TWRP)
DTSS PHASE 2

DRAWING TITLE

P&ID LEGEND
LOCAL CONTROL STATION
SHEET 1 OF 4

DRAFTED: LL	DESIGNED: JL	SHEET SIZE: A1
DRAFTING CHECK: DW	DESIGN CHECK: JL	SCALE: NTS
DATE: 29/11/17	REVIEWED: CN	PBS: 131101
CONTRACT: -	DRAWING NUMBER: PUB-DTSS2-TWRP WSW00-P-0014	REVISION: T1

THIS DRAWING IS COPYRIGHT