



TYPE 21

MOTORIZED VALVE

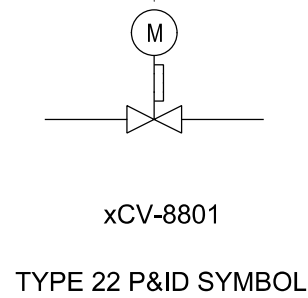


TYPE 22

MOTORIZED CONTROL VALVE WITH
POSITIONER

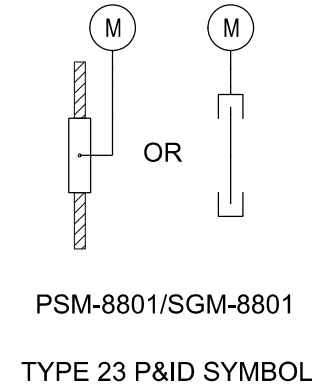

TYPE 23


MOTORIZED PENSTOCK/ SLIDE GATE

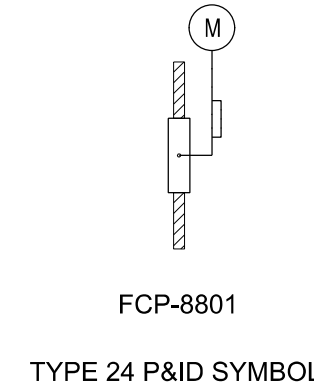

TYPE 24


MOTORIZED
PENSTOCK/ SLIDE GATE WITH POSITIONER

- NOTES:
1. LOCAL CONTROLS FOR ACTUATOR SHALL BE INTEGRAL TO ACTUATOR UNLESS INACCESSIBLE.
 2. PROVIDE STAND ALONE LCS FOR EACH INACCESSIBLE ACTUATOR. ISOLATOR SHALL BE PROVIDED ON THE LCS.
 3. THERE COULD BE MORE THAN ONE VALVE CONNECTED TO A HPU/LCP. OPEN AND CLOSE BUTT AND INDICATION LIGHTS SHALL BE PROVIDED ACCORDING TO NUMBER OF VALVES CONNECTED.
 4. LCS/OFF/SCADA SELECTOR SWITCH SHALL BE KEY OPERATED.

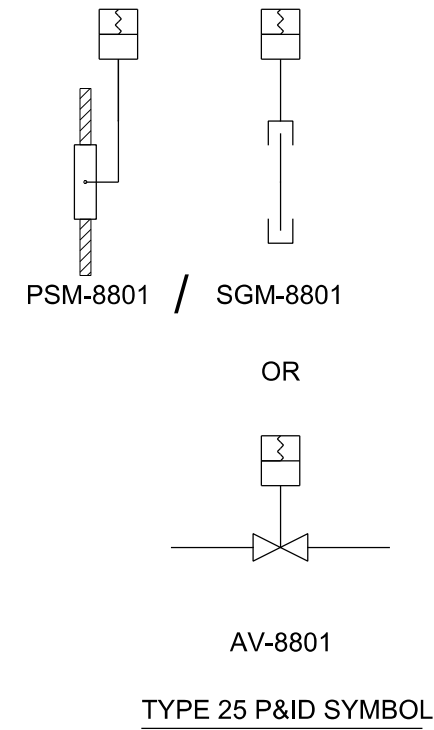


TYPE 25

PNEUMATIC ACTUATED VALVE/SLIDE GATE/
PENSTOCK

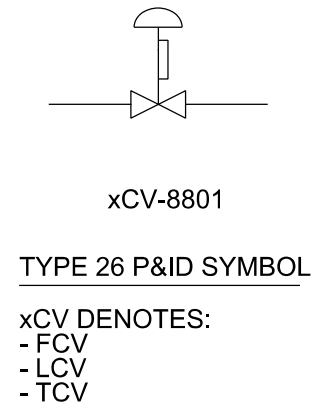


TYPE 26

PNEUMATIC ACTUATED VALVE WITH
POSITIONER

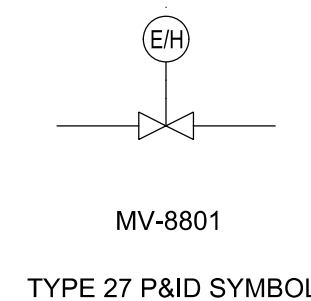


TYPE 27

ELECTROHYDRAULIC ACTUATED VALVE

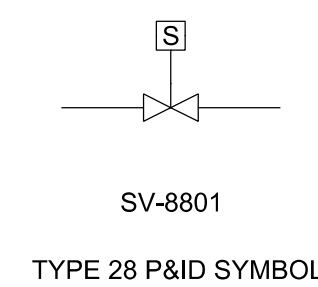

TYPE 28

SOLENOID VALVE

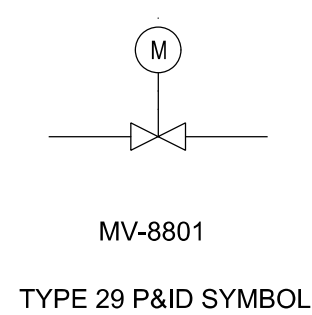

TYPE 29

SINGLE PHASE MOTORISED VALVE

TENDER			
T1	20/05/22	ISSUED FOR TENDER C4B	CN GOT
T1	02/07/21	ISSUED FOR TENDER C3D2	CN GOT
T1	18/12/20	ISSUED FOR TENDER C3B1	CN GOT
T1	23/07/20	ISSUED FOR TENDER C2B	CN GOT
T1	24/04/20	ISSUED FOR TENDER C3A	CN GOT
T1	08/04/20	ISSUED FOR TENDER C3D1	CN GOT
REV	DATE	DESCRIPTION	REVIEWED / AUTHORISED
CLIENT: SINGAPORE'S NATIONAL WATER AGENCY			
PROGRAMME MANAGER: A JOINT VENTURE DELIVERING THE DTSS2 PROJECT			
CONSULTANT: CH2M HILL Singapore Pte Ltd			
PROJECT TITLE: TUAS WATER RECLAMATION PLANT (TWRP) DTSS PHASE 2			
DRAWING TITLE P&ID LEGEND LOCAL CONTROL STATION SHEET 3 OF 4			
DRAFTED: JMJ	DESIGNED: JL	SHEET SIZE: A1	
DRAFTING CHECK: DW	DESIGN CHECK: JL	SCALE: NTS	
DATE: 29/11/17	REVIEWED: CN	PBS: 131101	
CONTRACT: DRAWING NUMBER: PUB-DTSS2-TWRP REVISION: T1			
THIS DRAWING IS COPYRIGHT			