

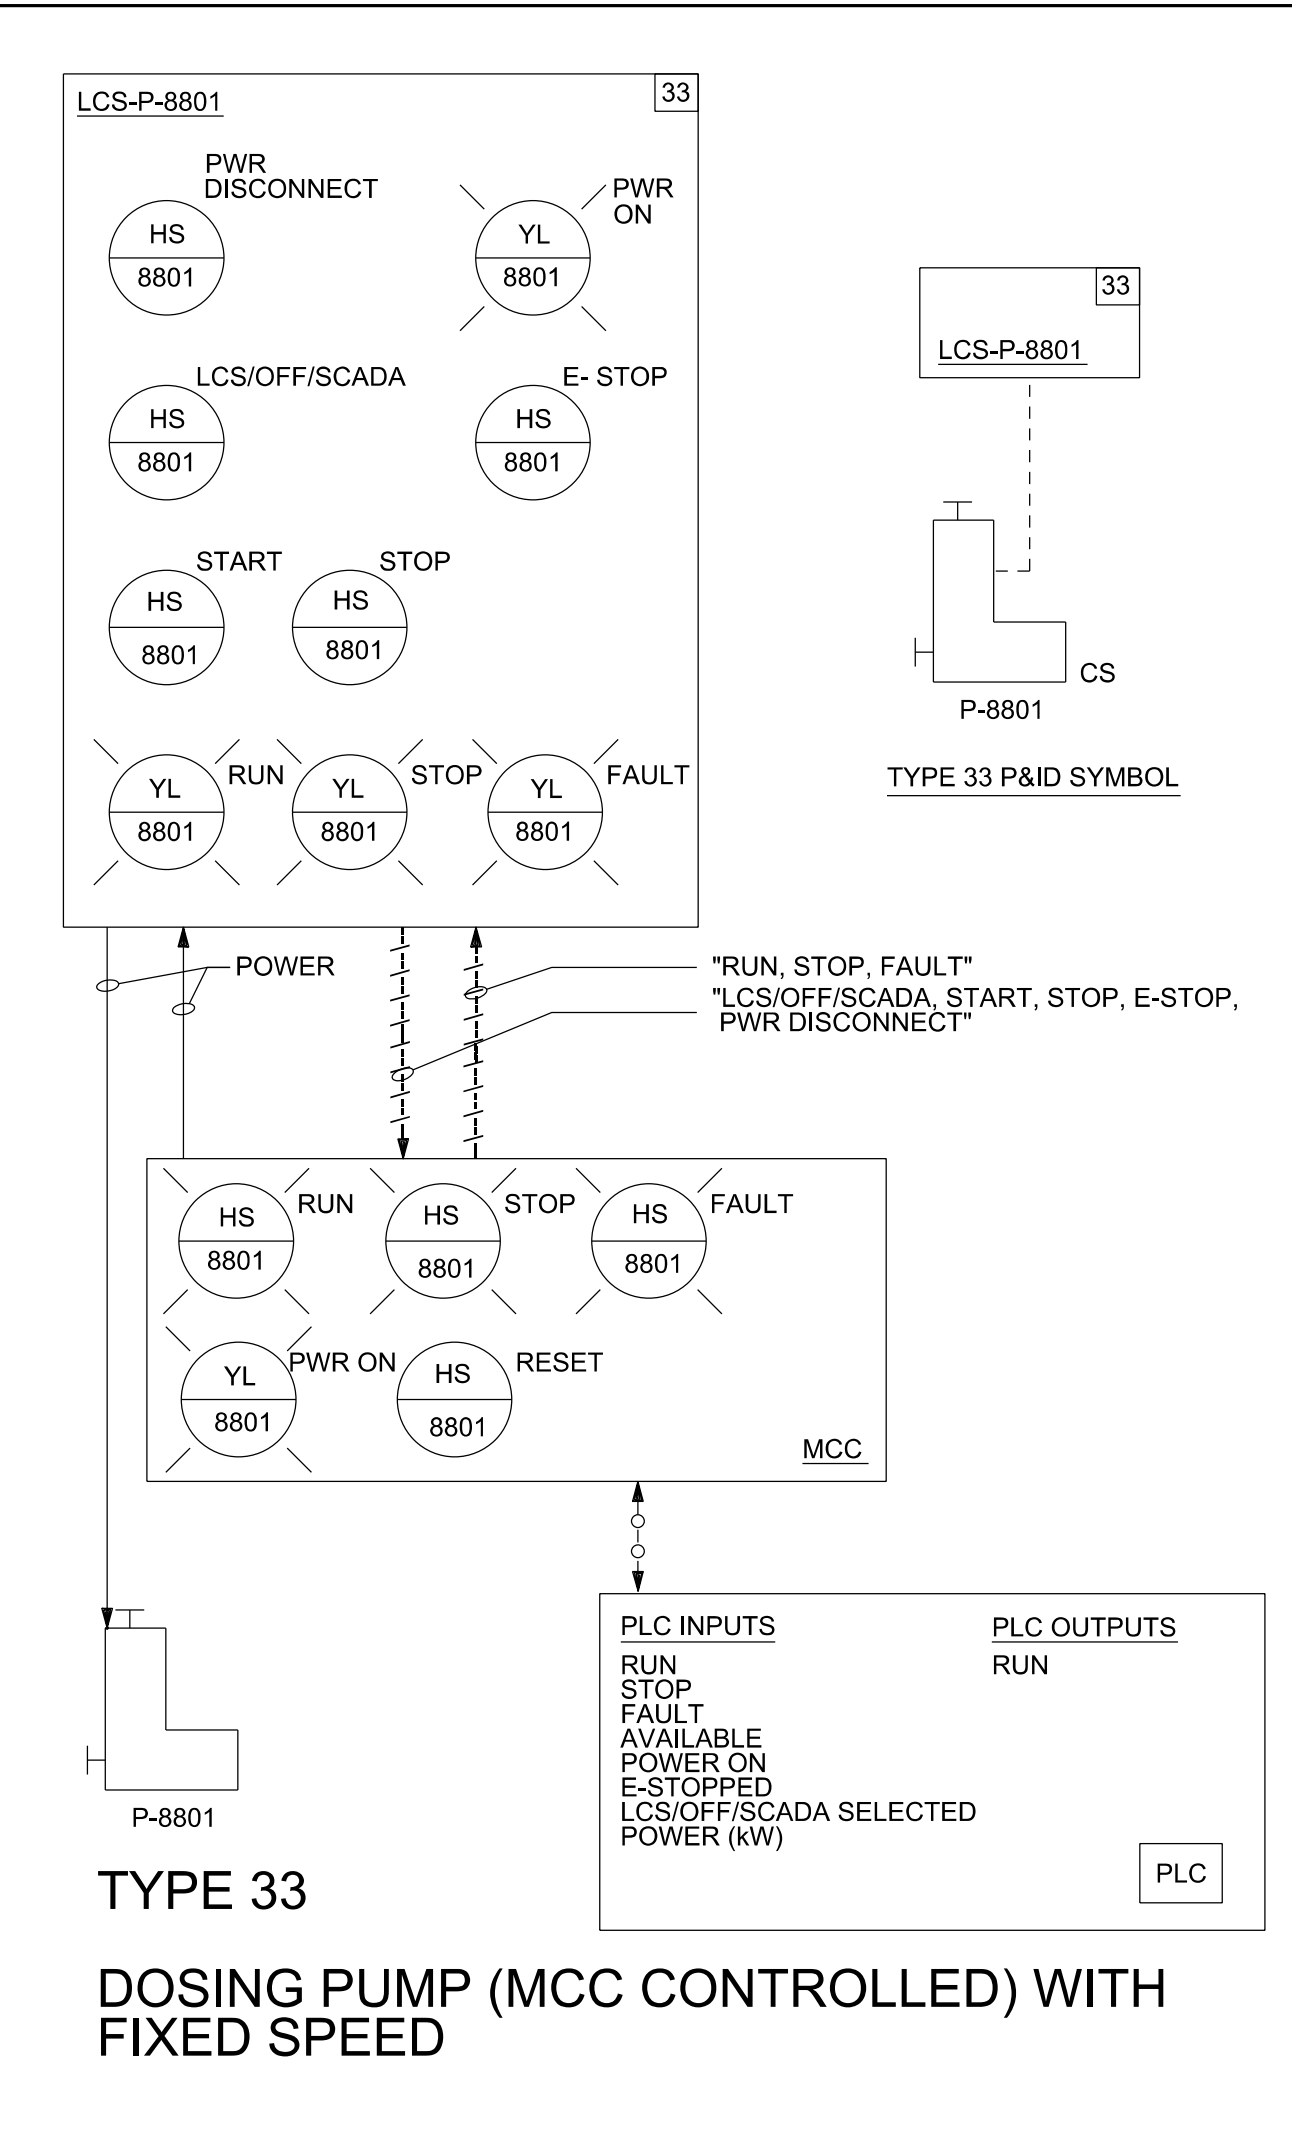
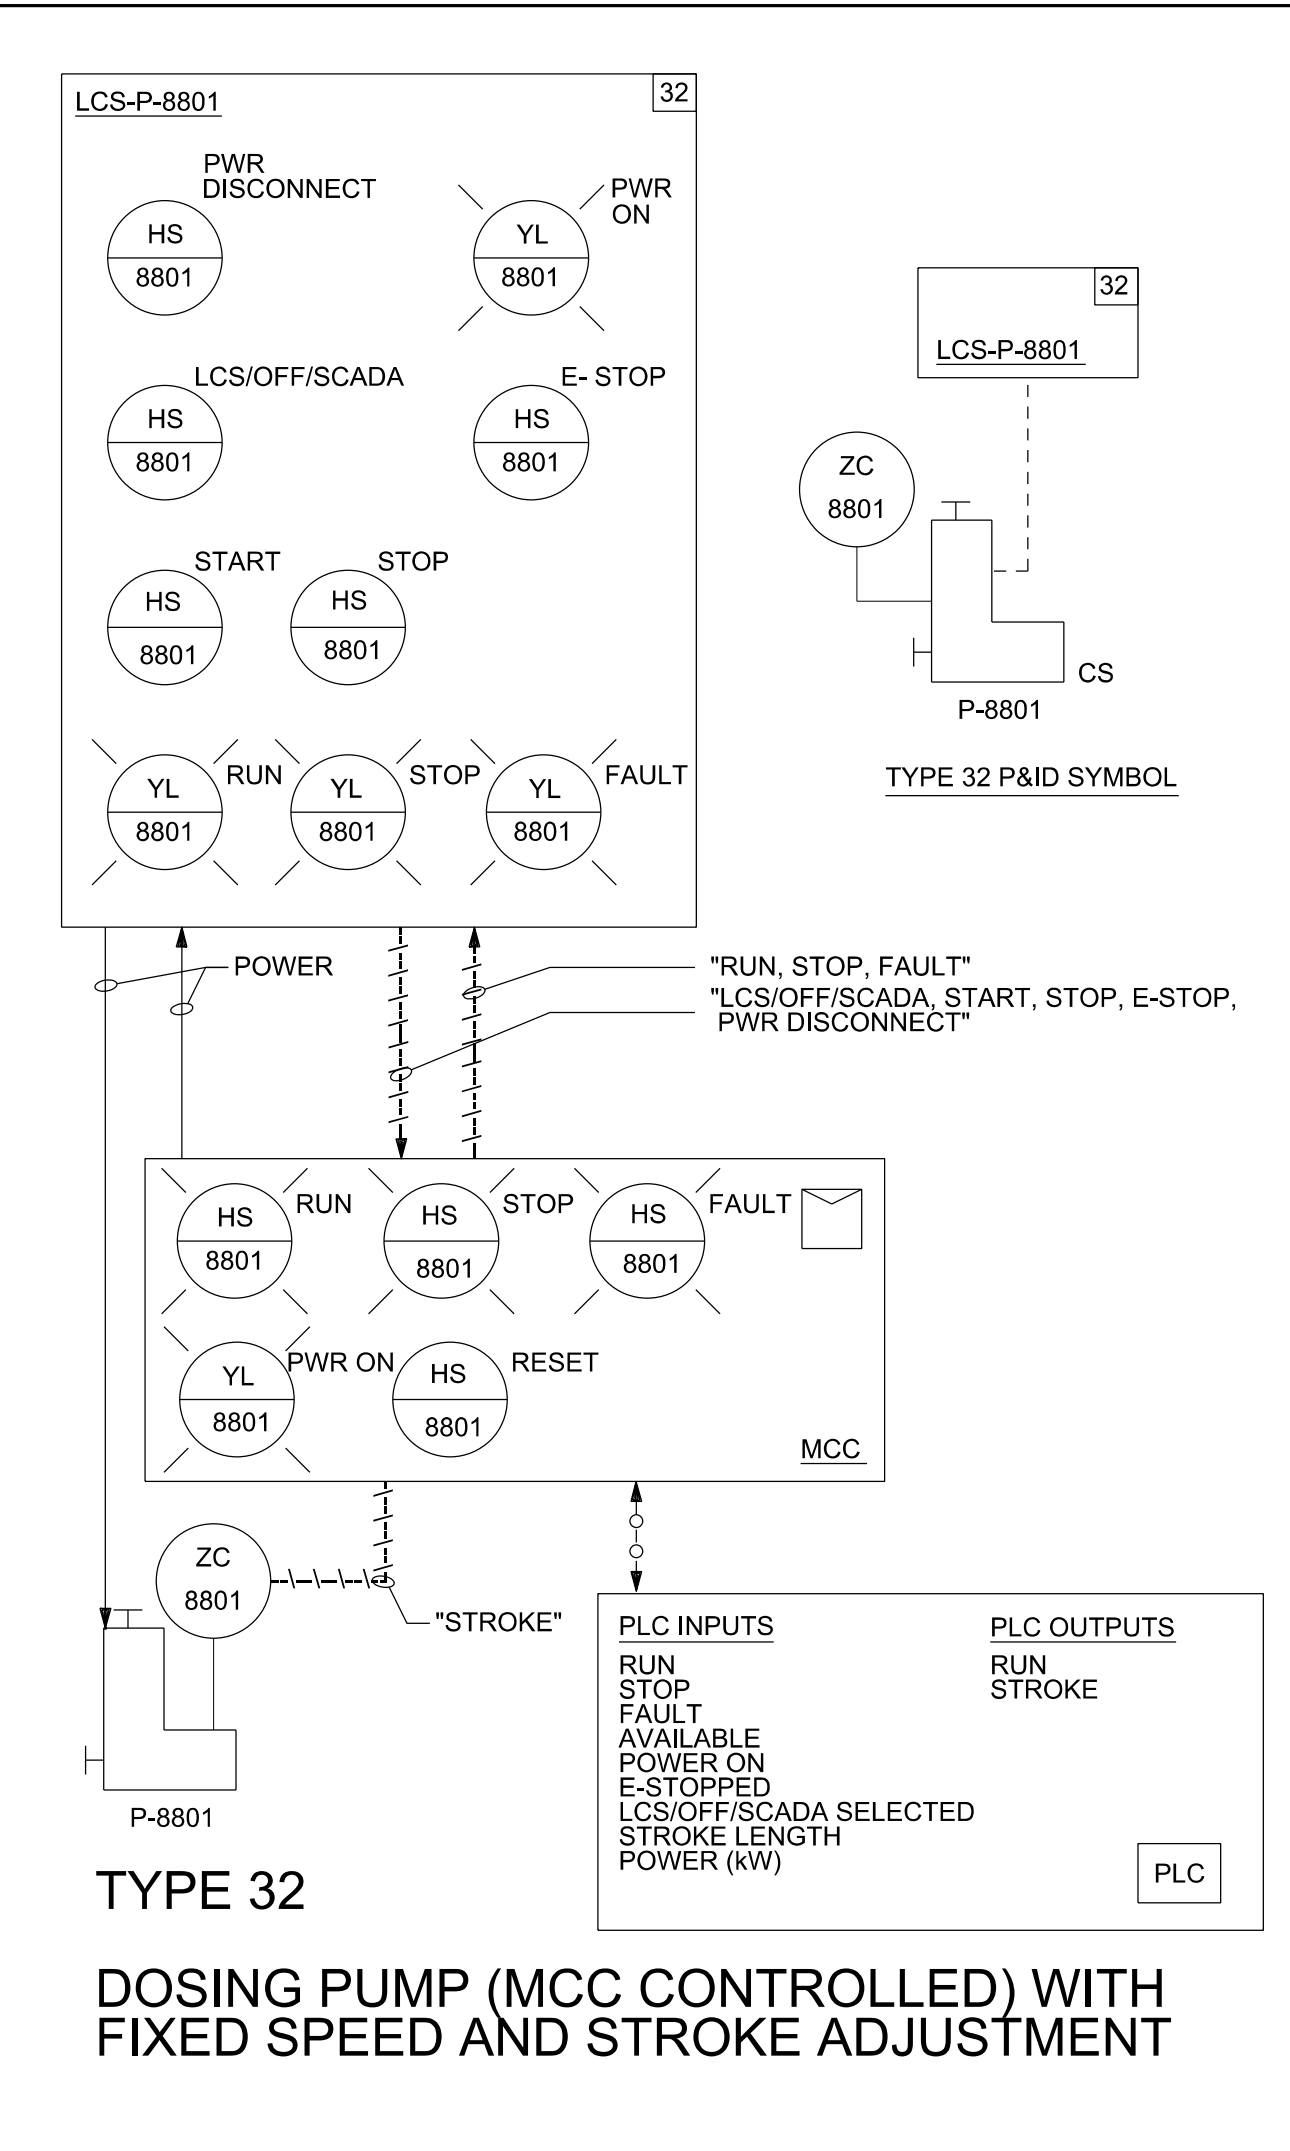
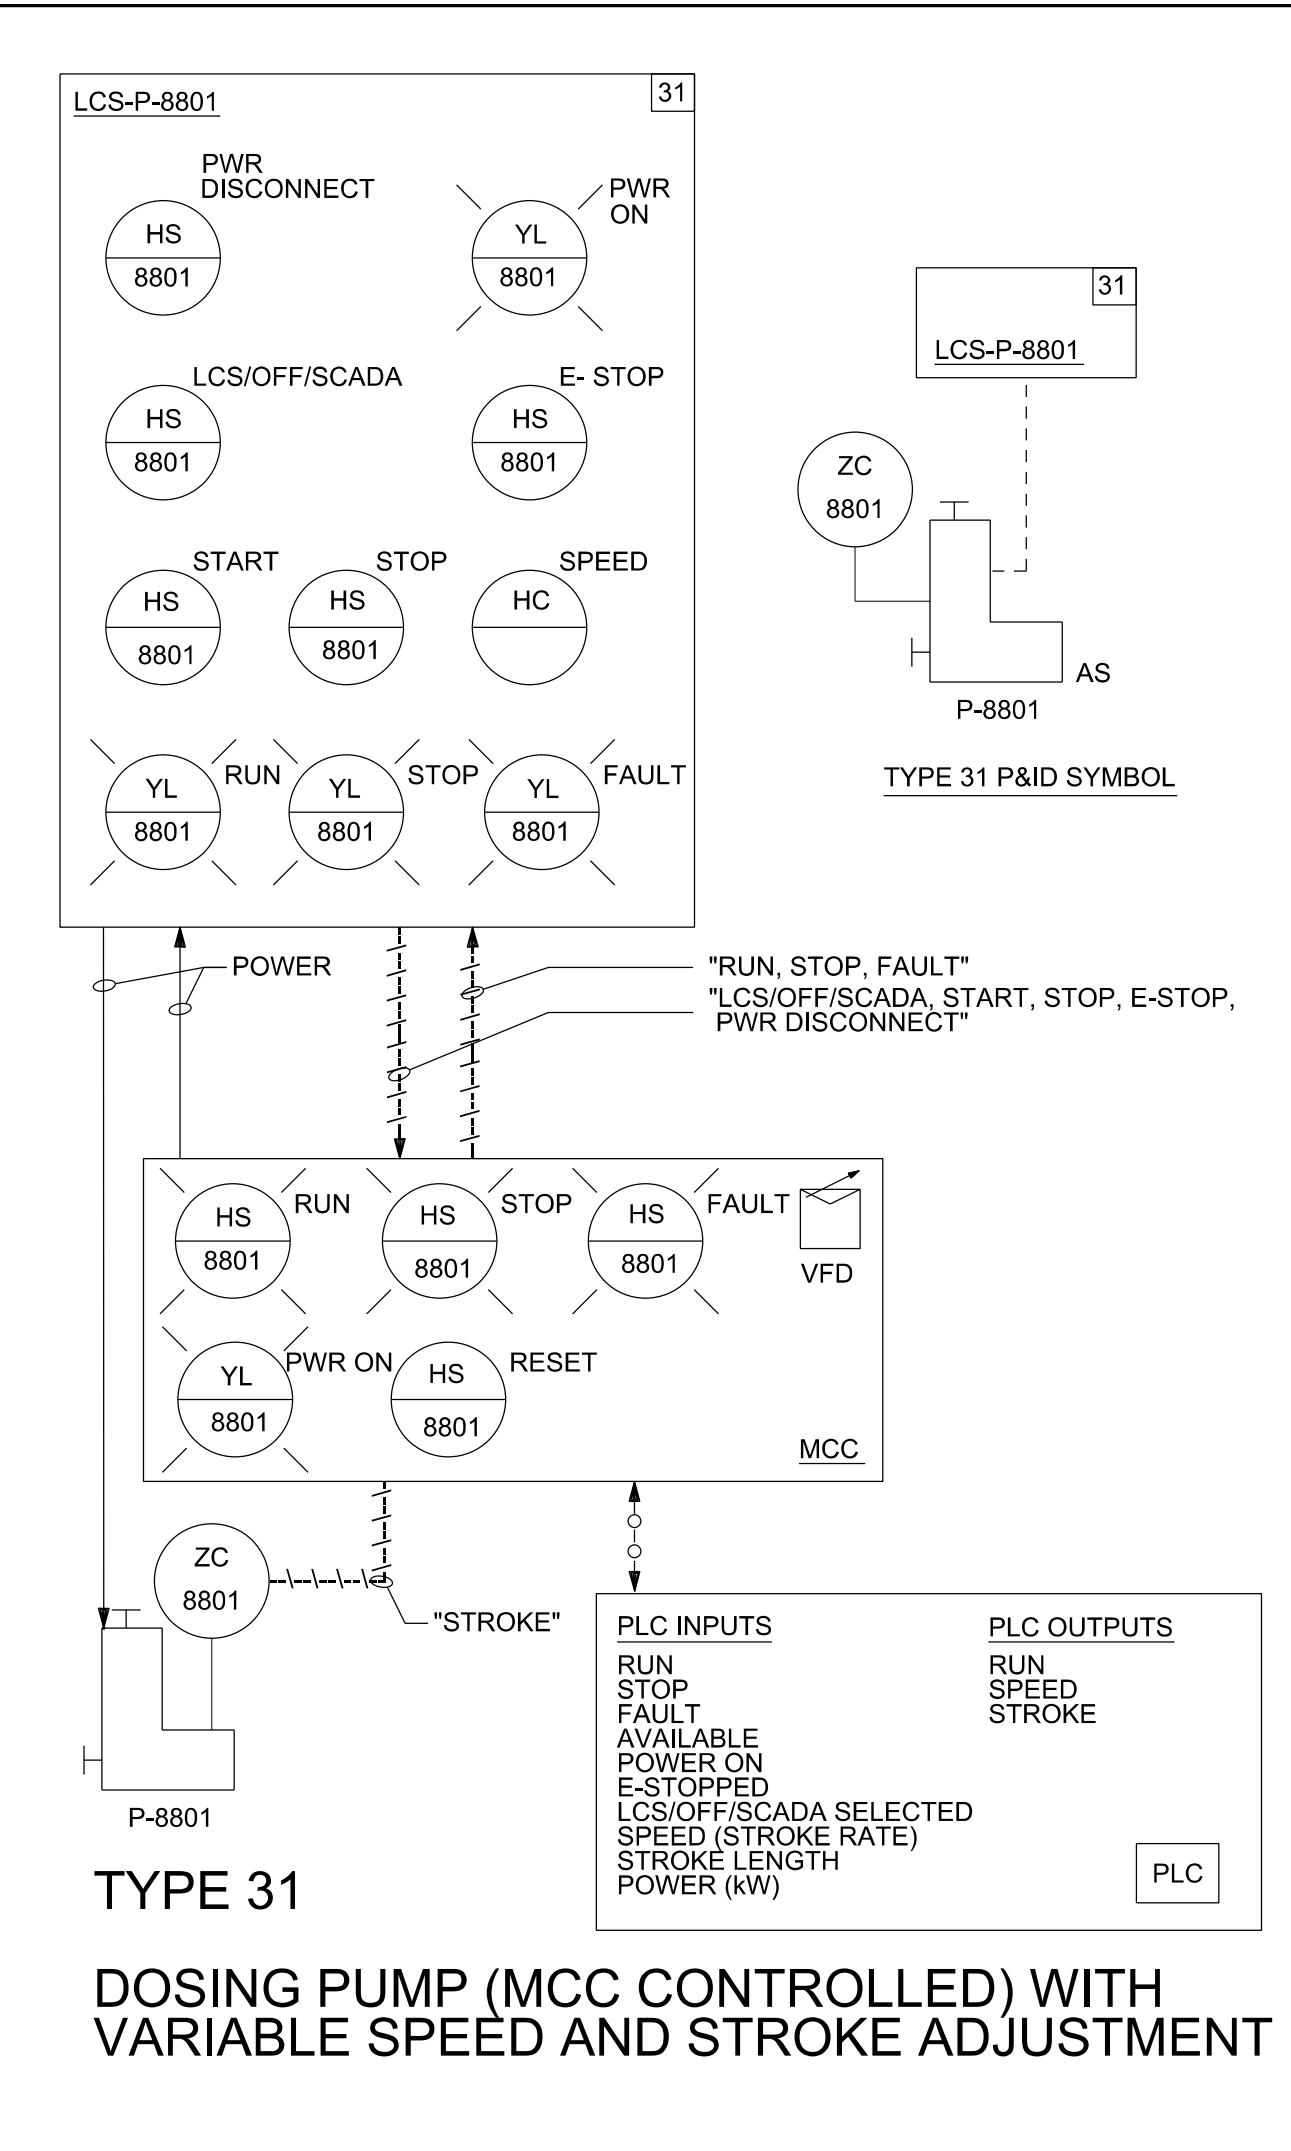
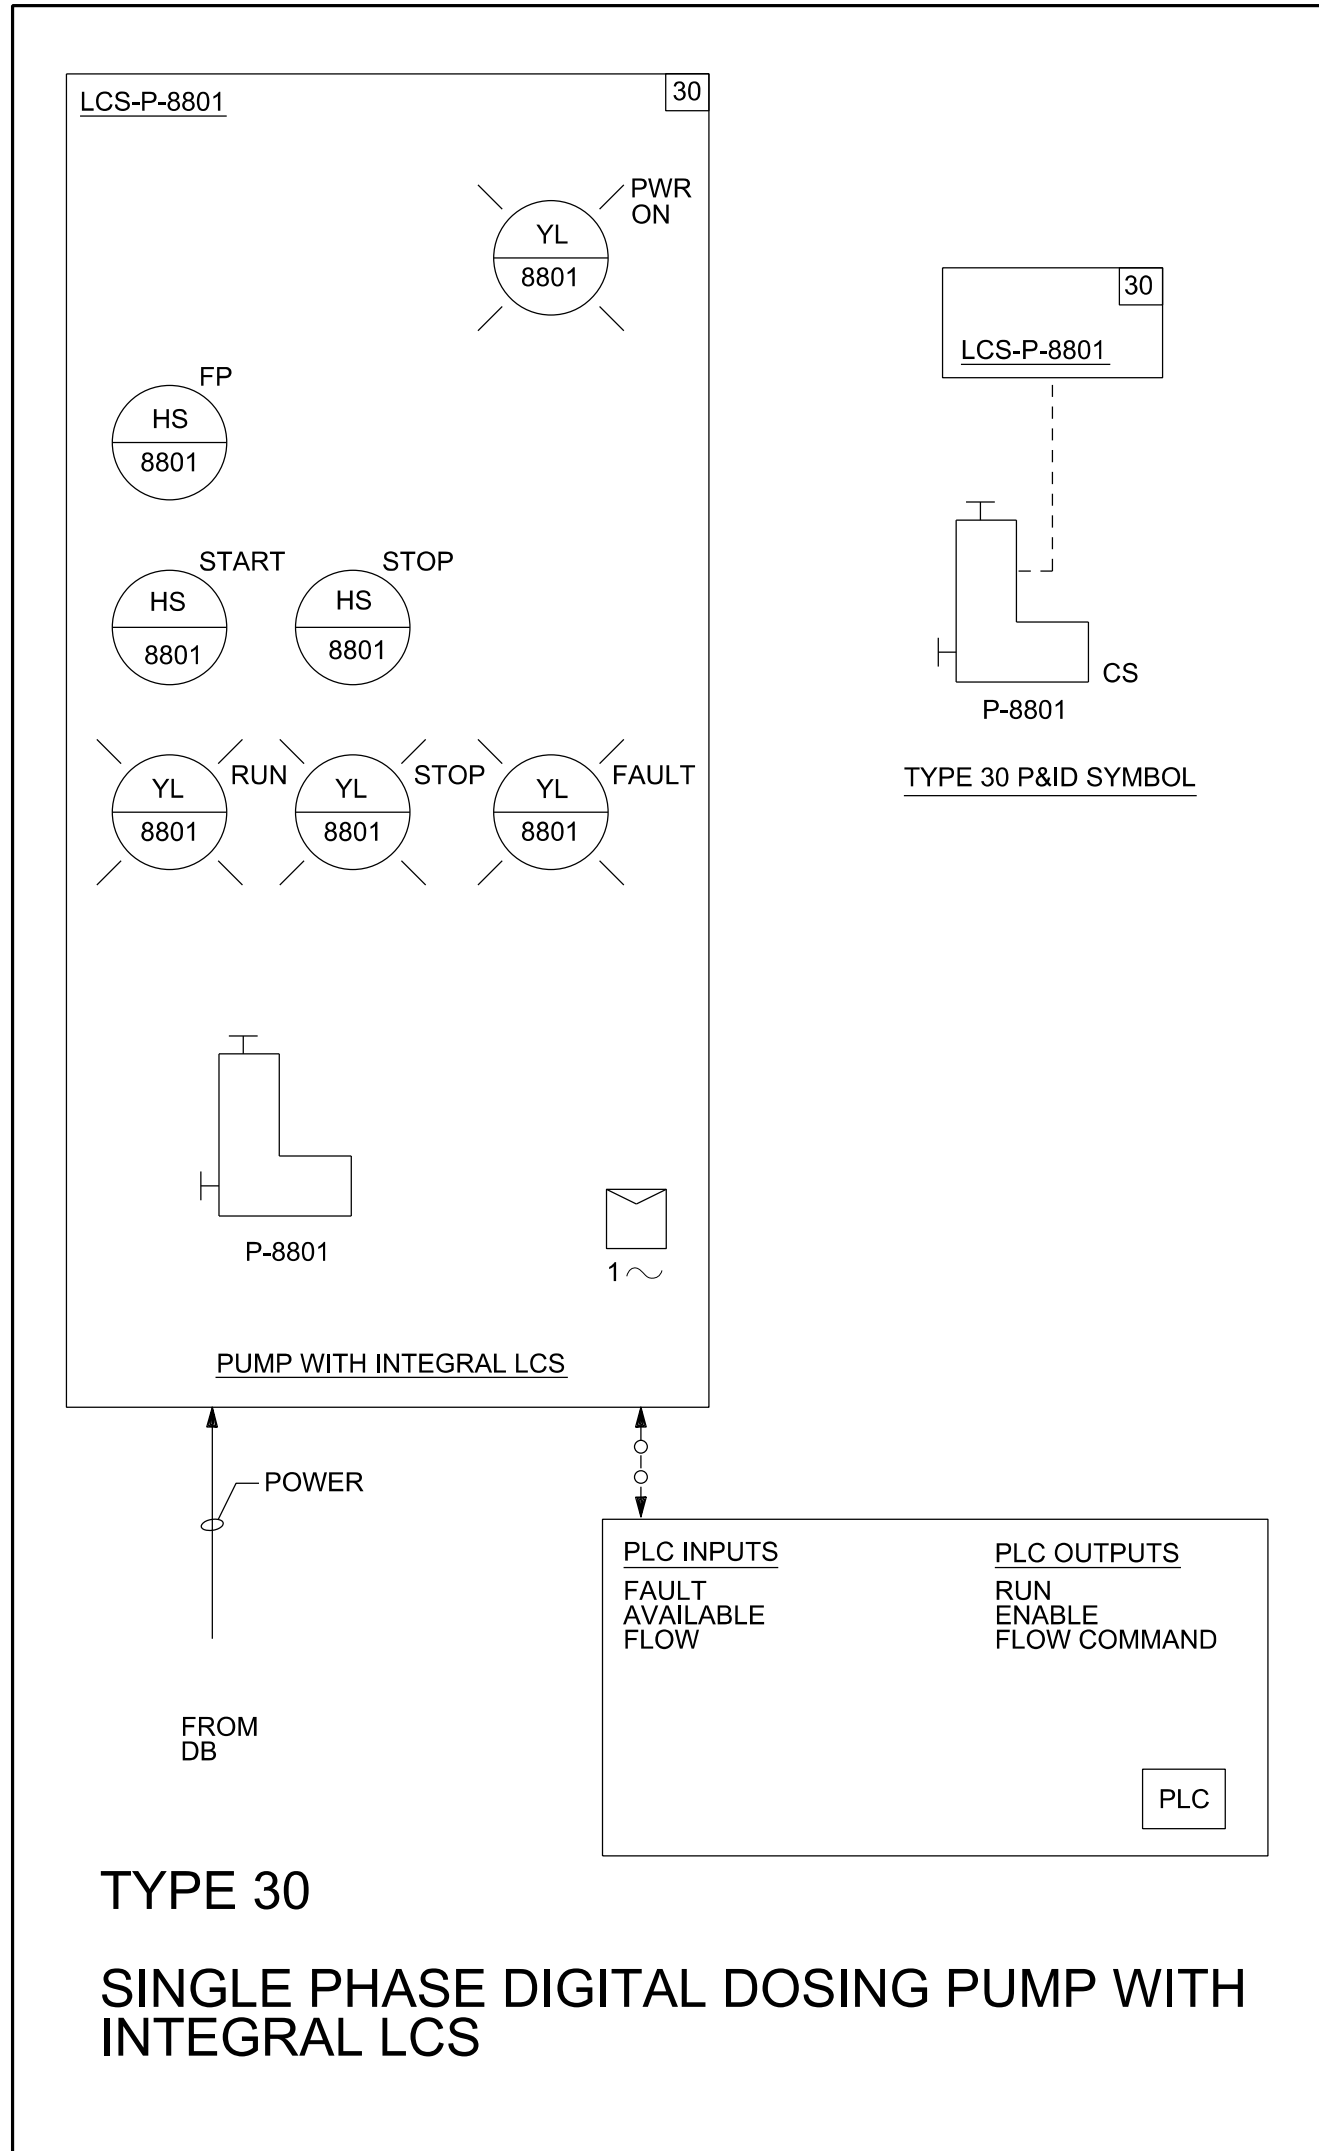
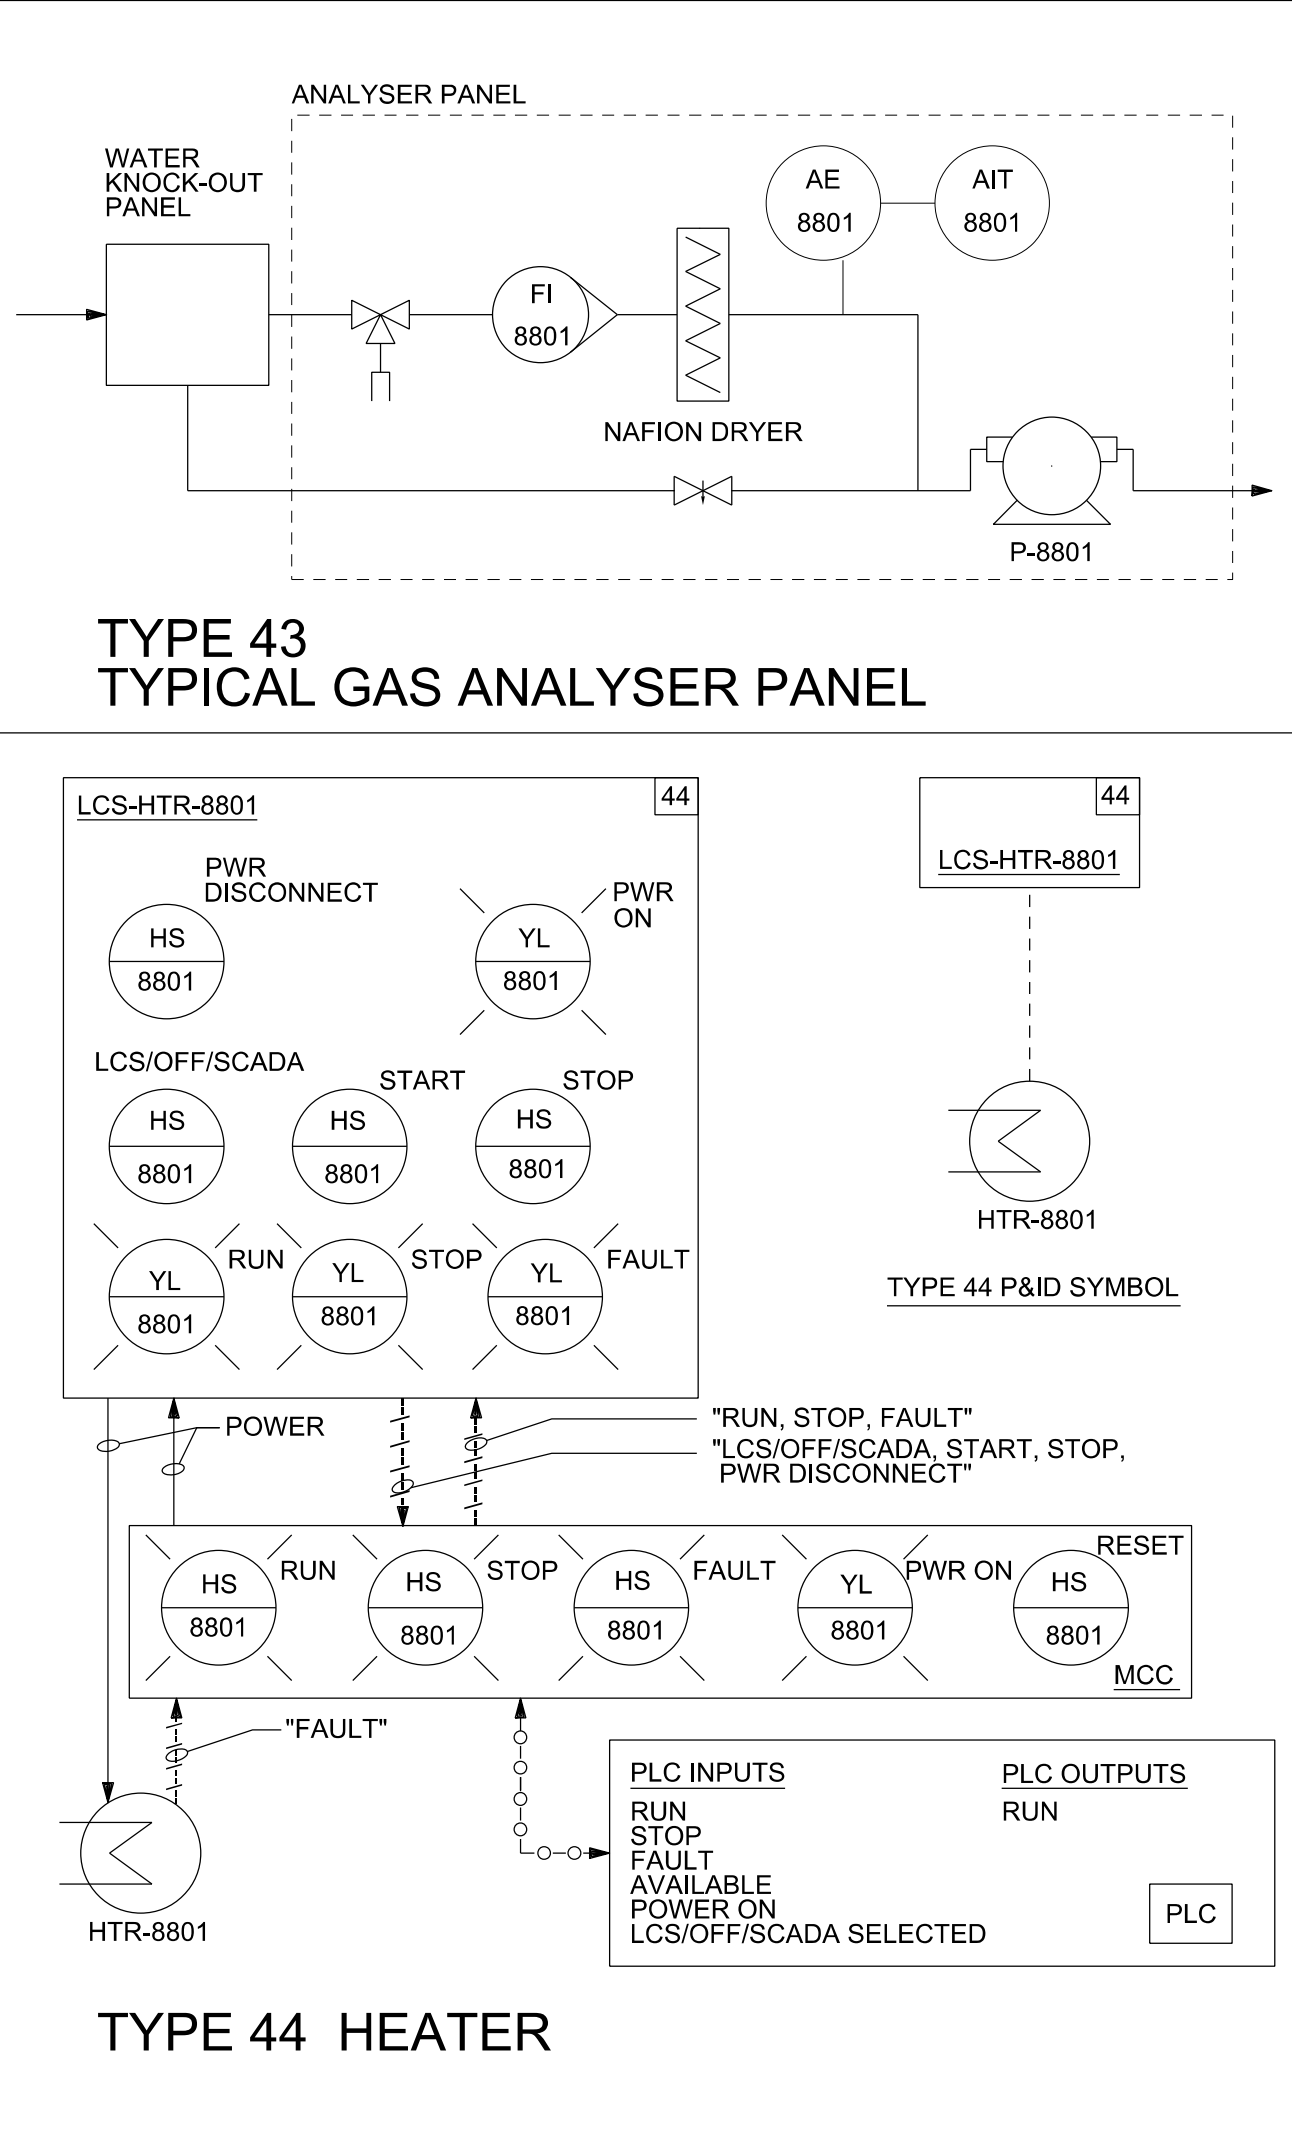


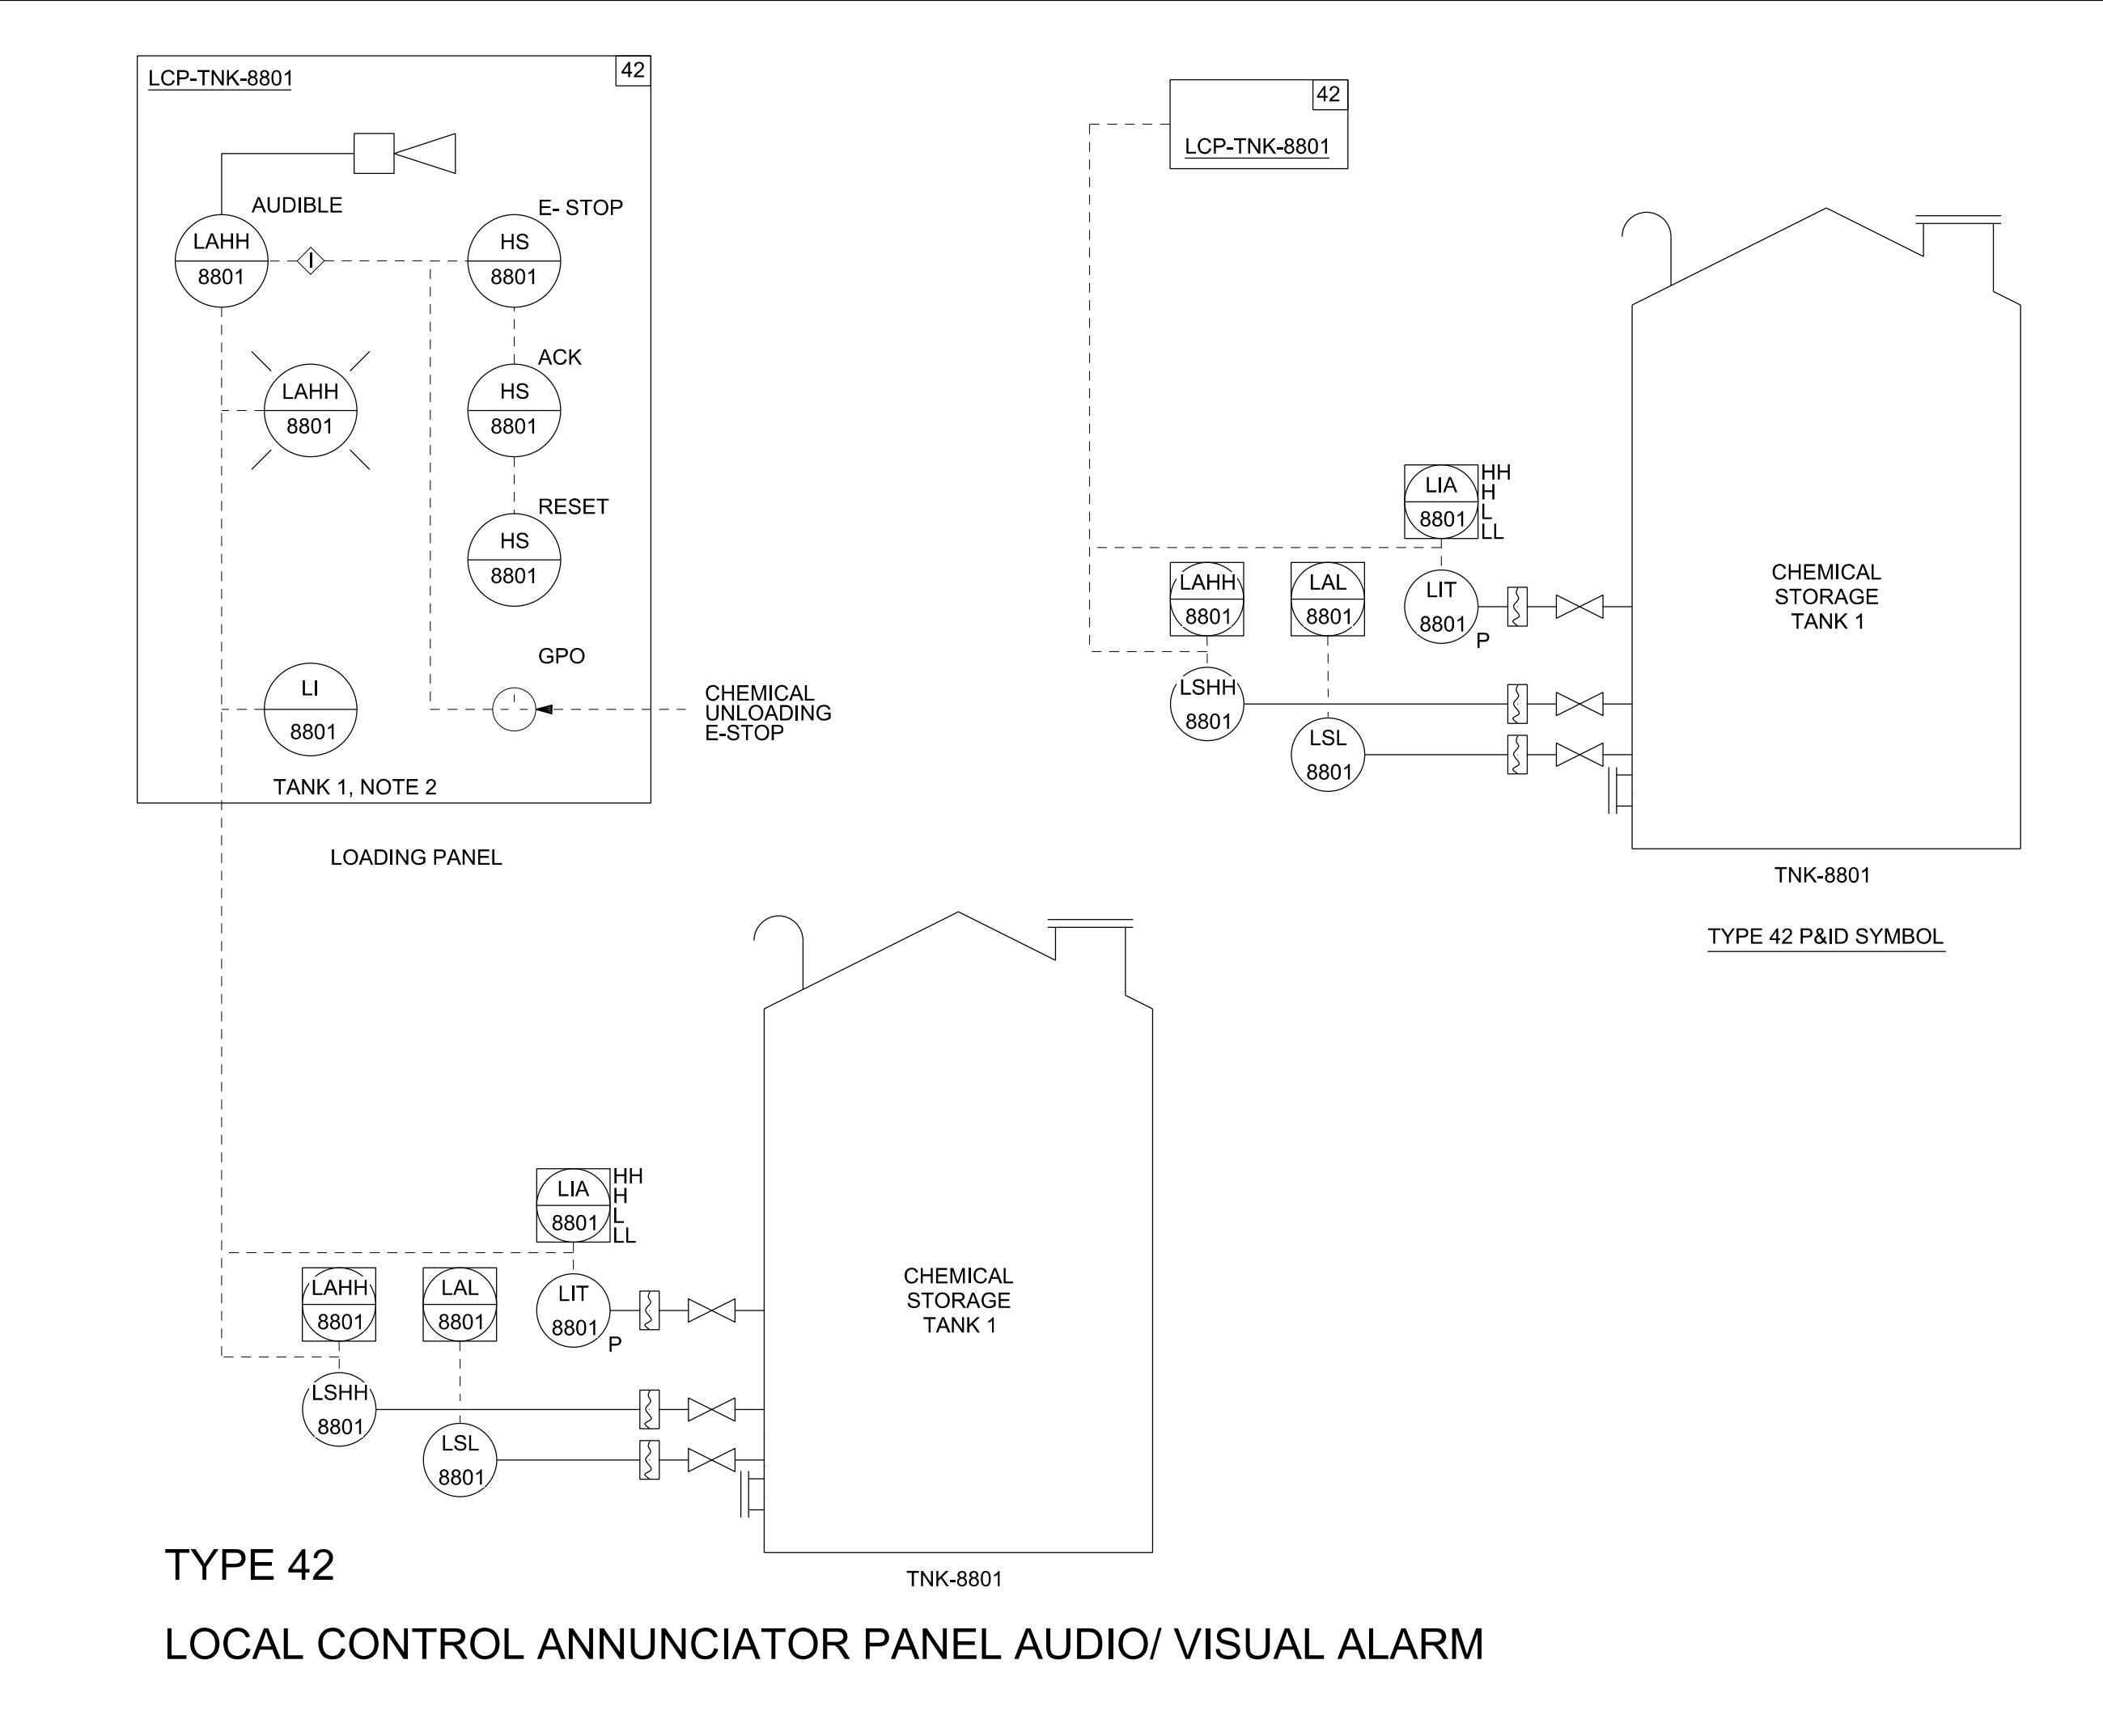

NOTES:

1. STANDARD LCS TYPICAL, MAY BE USED FOR ANY EQUIPMENT. PUMP SYMBOL INDICATIVE ONLY.
2. IF RELEVANT ADD LI, LAH AND LAHH FOR OTHER TANKS.

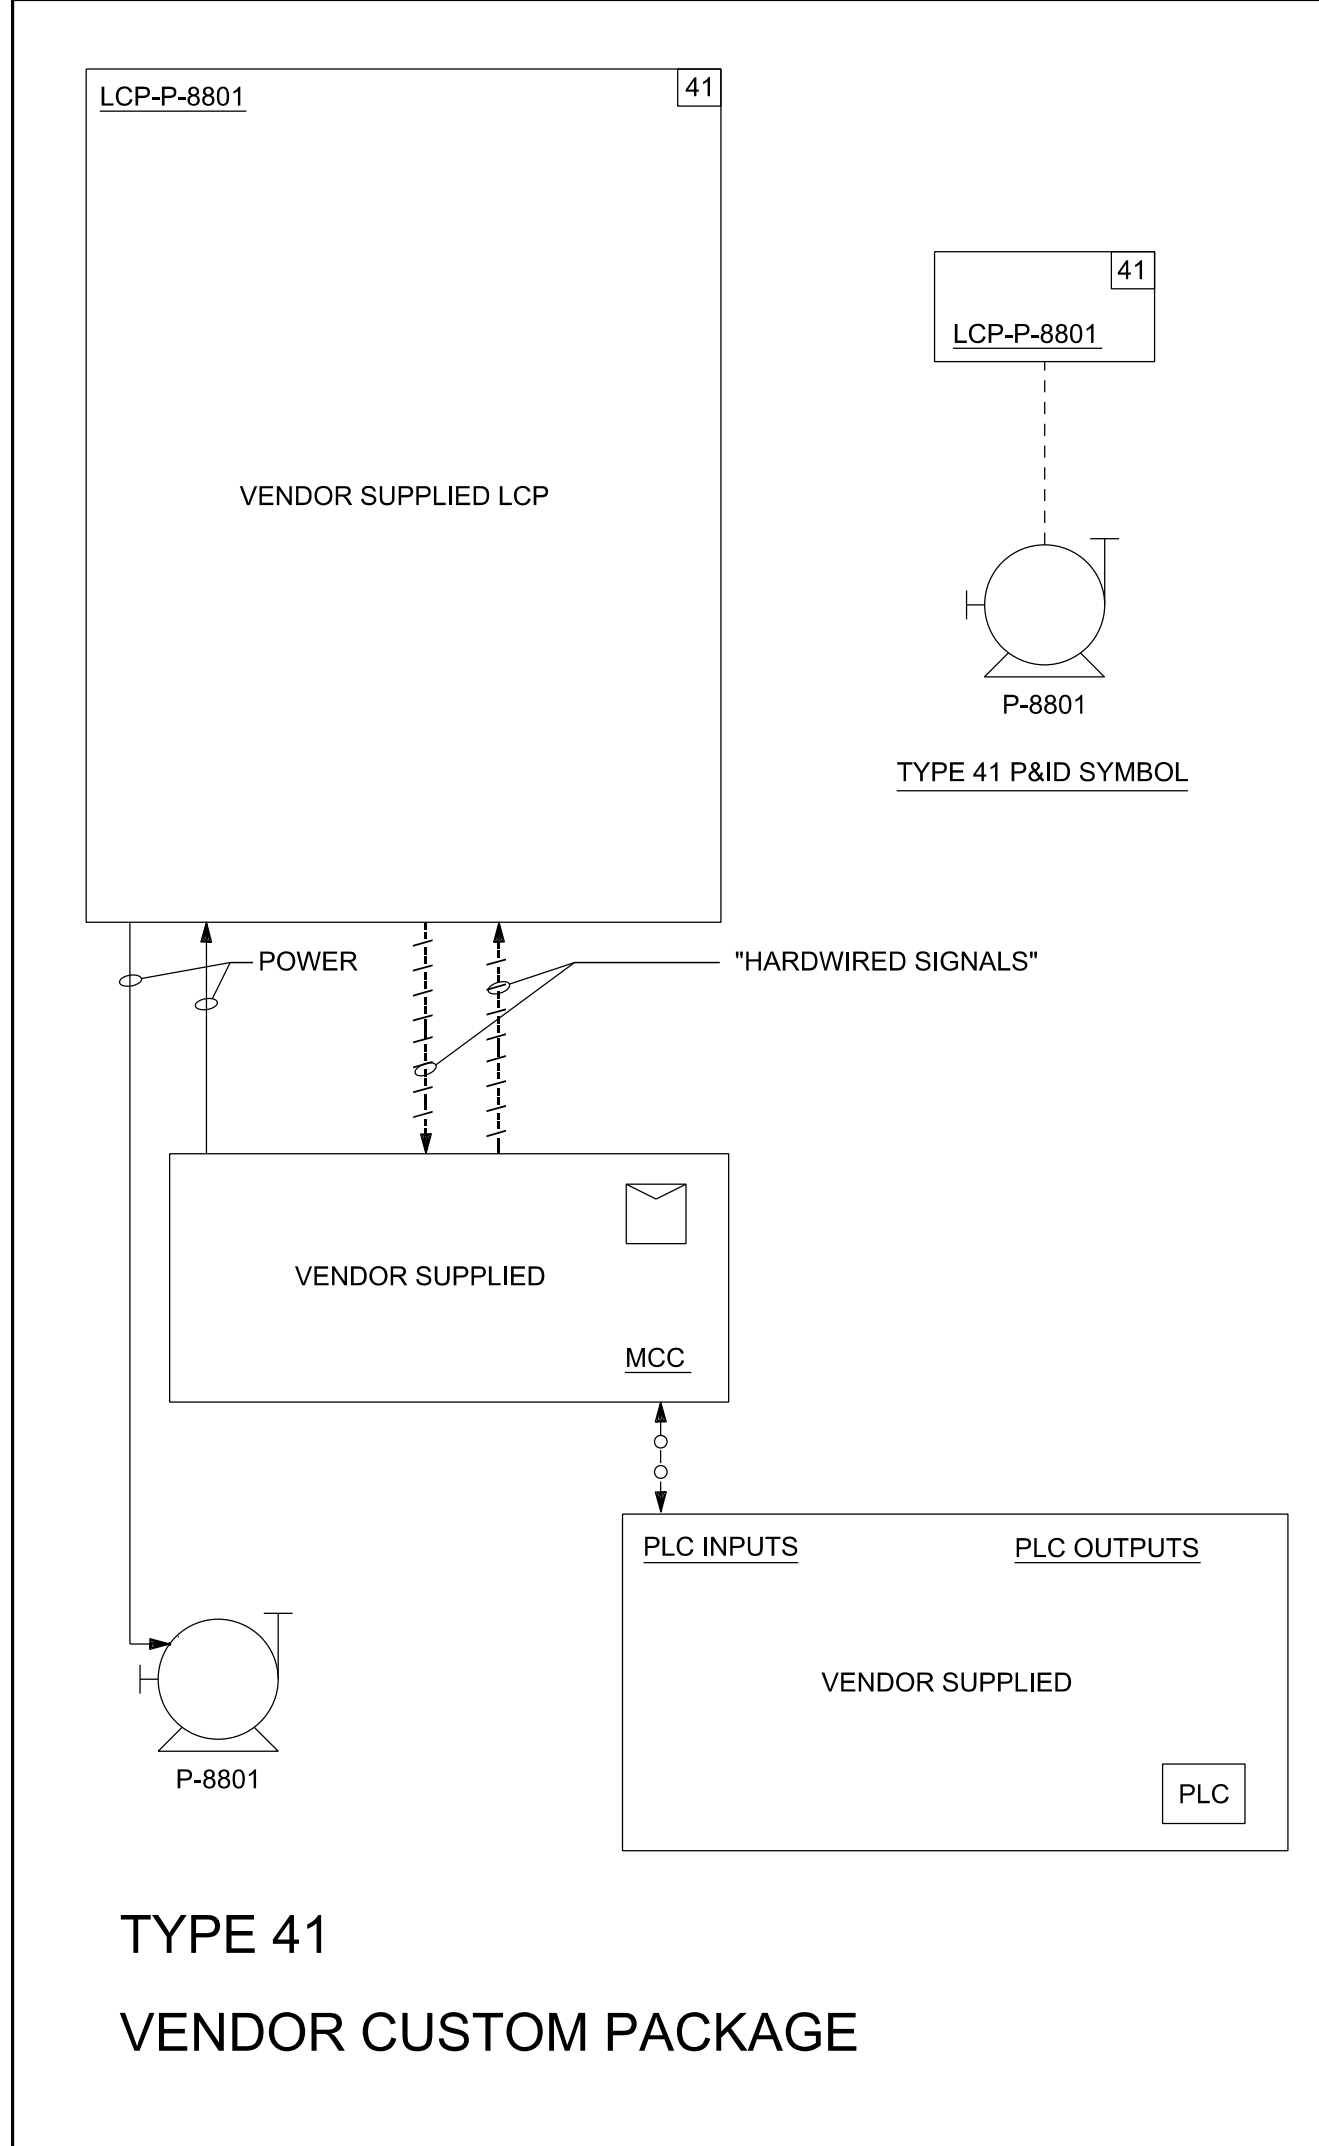

TENDER			
T1 20/05/22	ISSUED FOR TENDER C4B	CN	GOT
T1 02/07/21	ISSUED FOR TENDER C3D2	CN	GOT
T1 18/12/20	ISSUED FOR TENDER C3B1	CN	GOT
T1 23/07/20	ISSUED FOR TENDER C2B	CN	GOT
T1 24/04/20	ISSUED FOR TENDER C3A	CN	GOT
T1 08/04/20	ISSUED FOR TENDER C3D1	CN	GOT
REV	DATE	DESCRIPTION	REVIEWED / AUTHORISED
CLIENT:			
PROGRAMME MANAGER:			
CONSULTANT:			
PROJECT TITLE:			
DRAWING TITLE:			
DRAFTED:			
DESIGNED:			
SHEET SIZE:			
DRAFTING CHECK:			
DESIGN CHECK:			
SCALE:			
DATE:			
REVIEWED:			
PBS:			
CONTRACT:			
DRAWING NUMBER:			
SHEET NUMBER:			
REVISION:			
THIS DRAWING IS COPYRIGHT			