




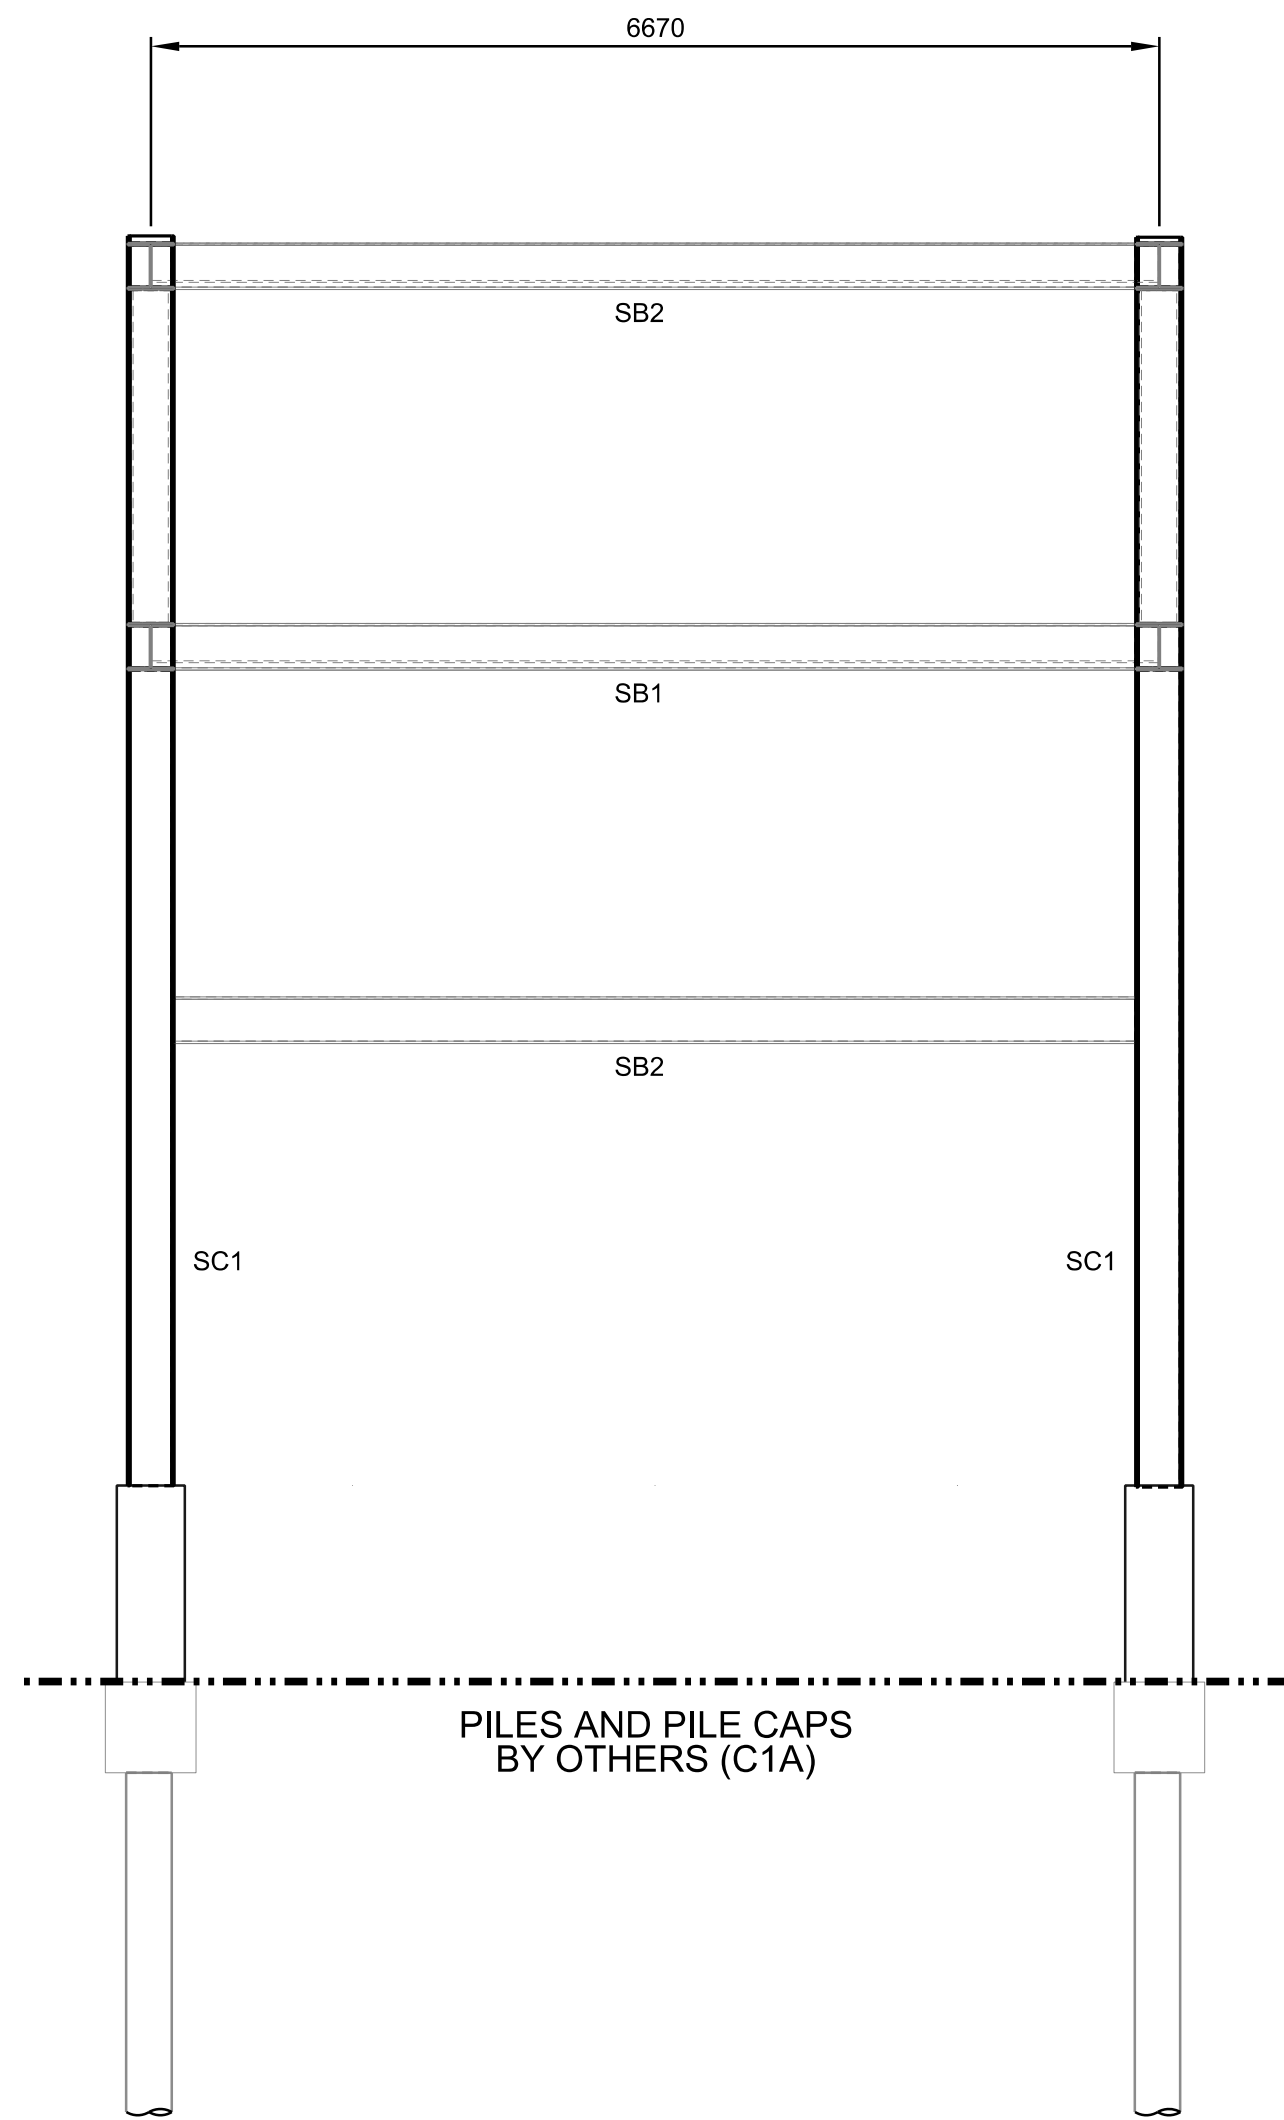


SECTION A - A
SCALE 1:50

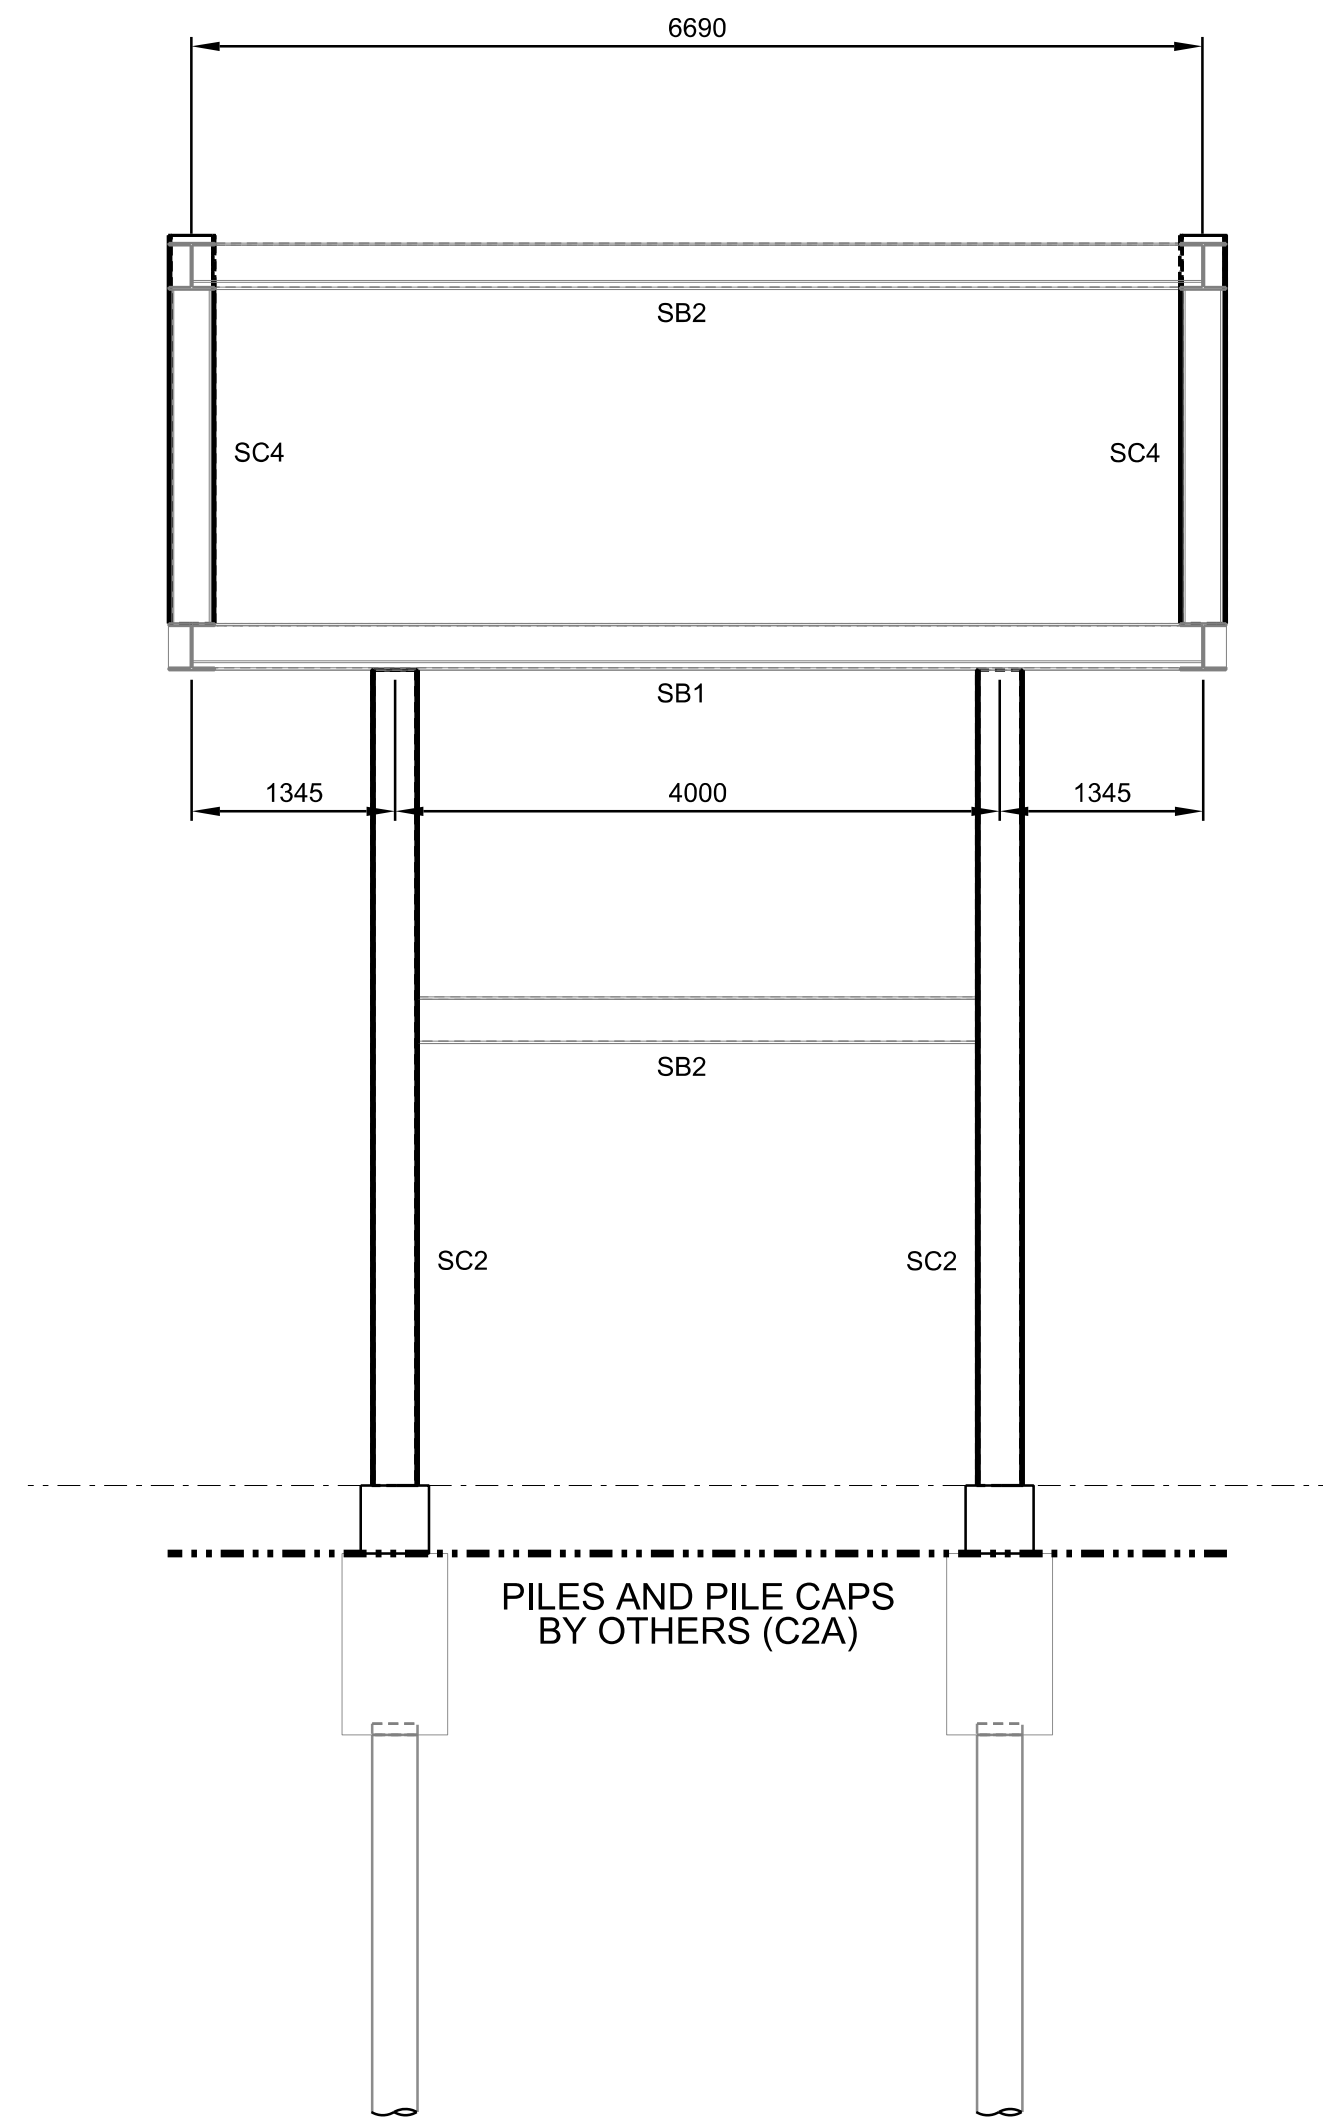


SECTION B - B
SCALE 1:50

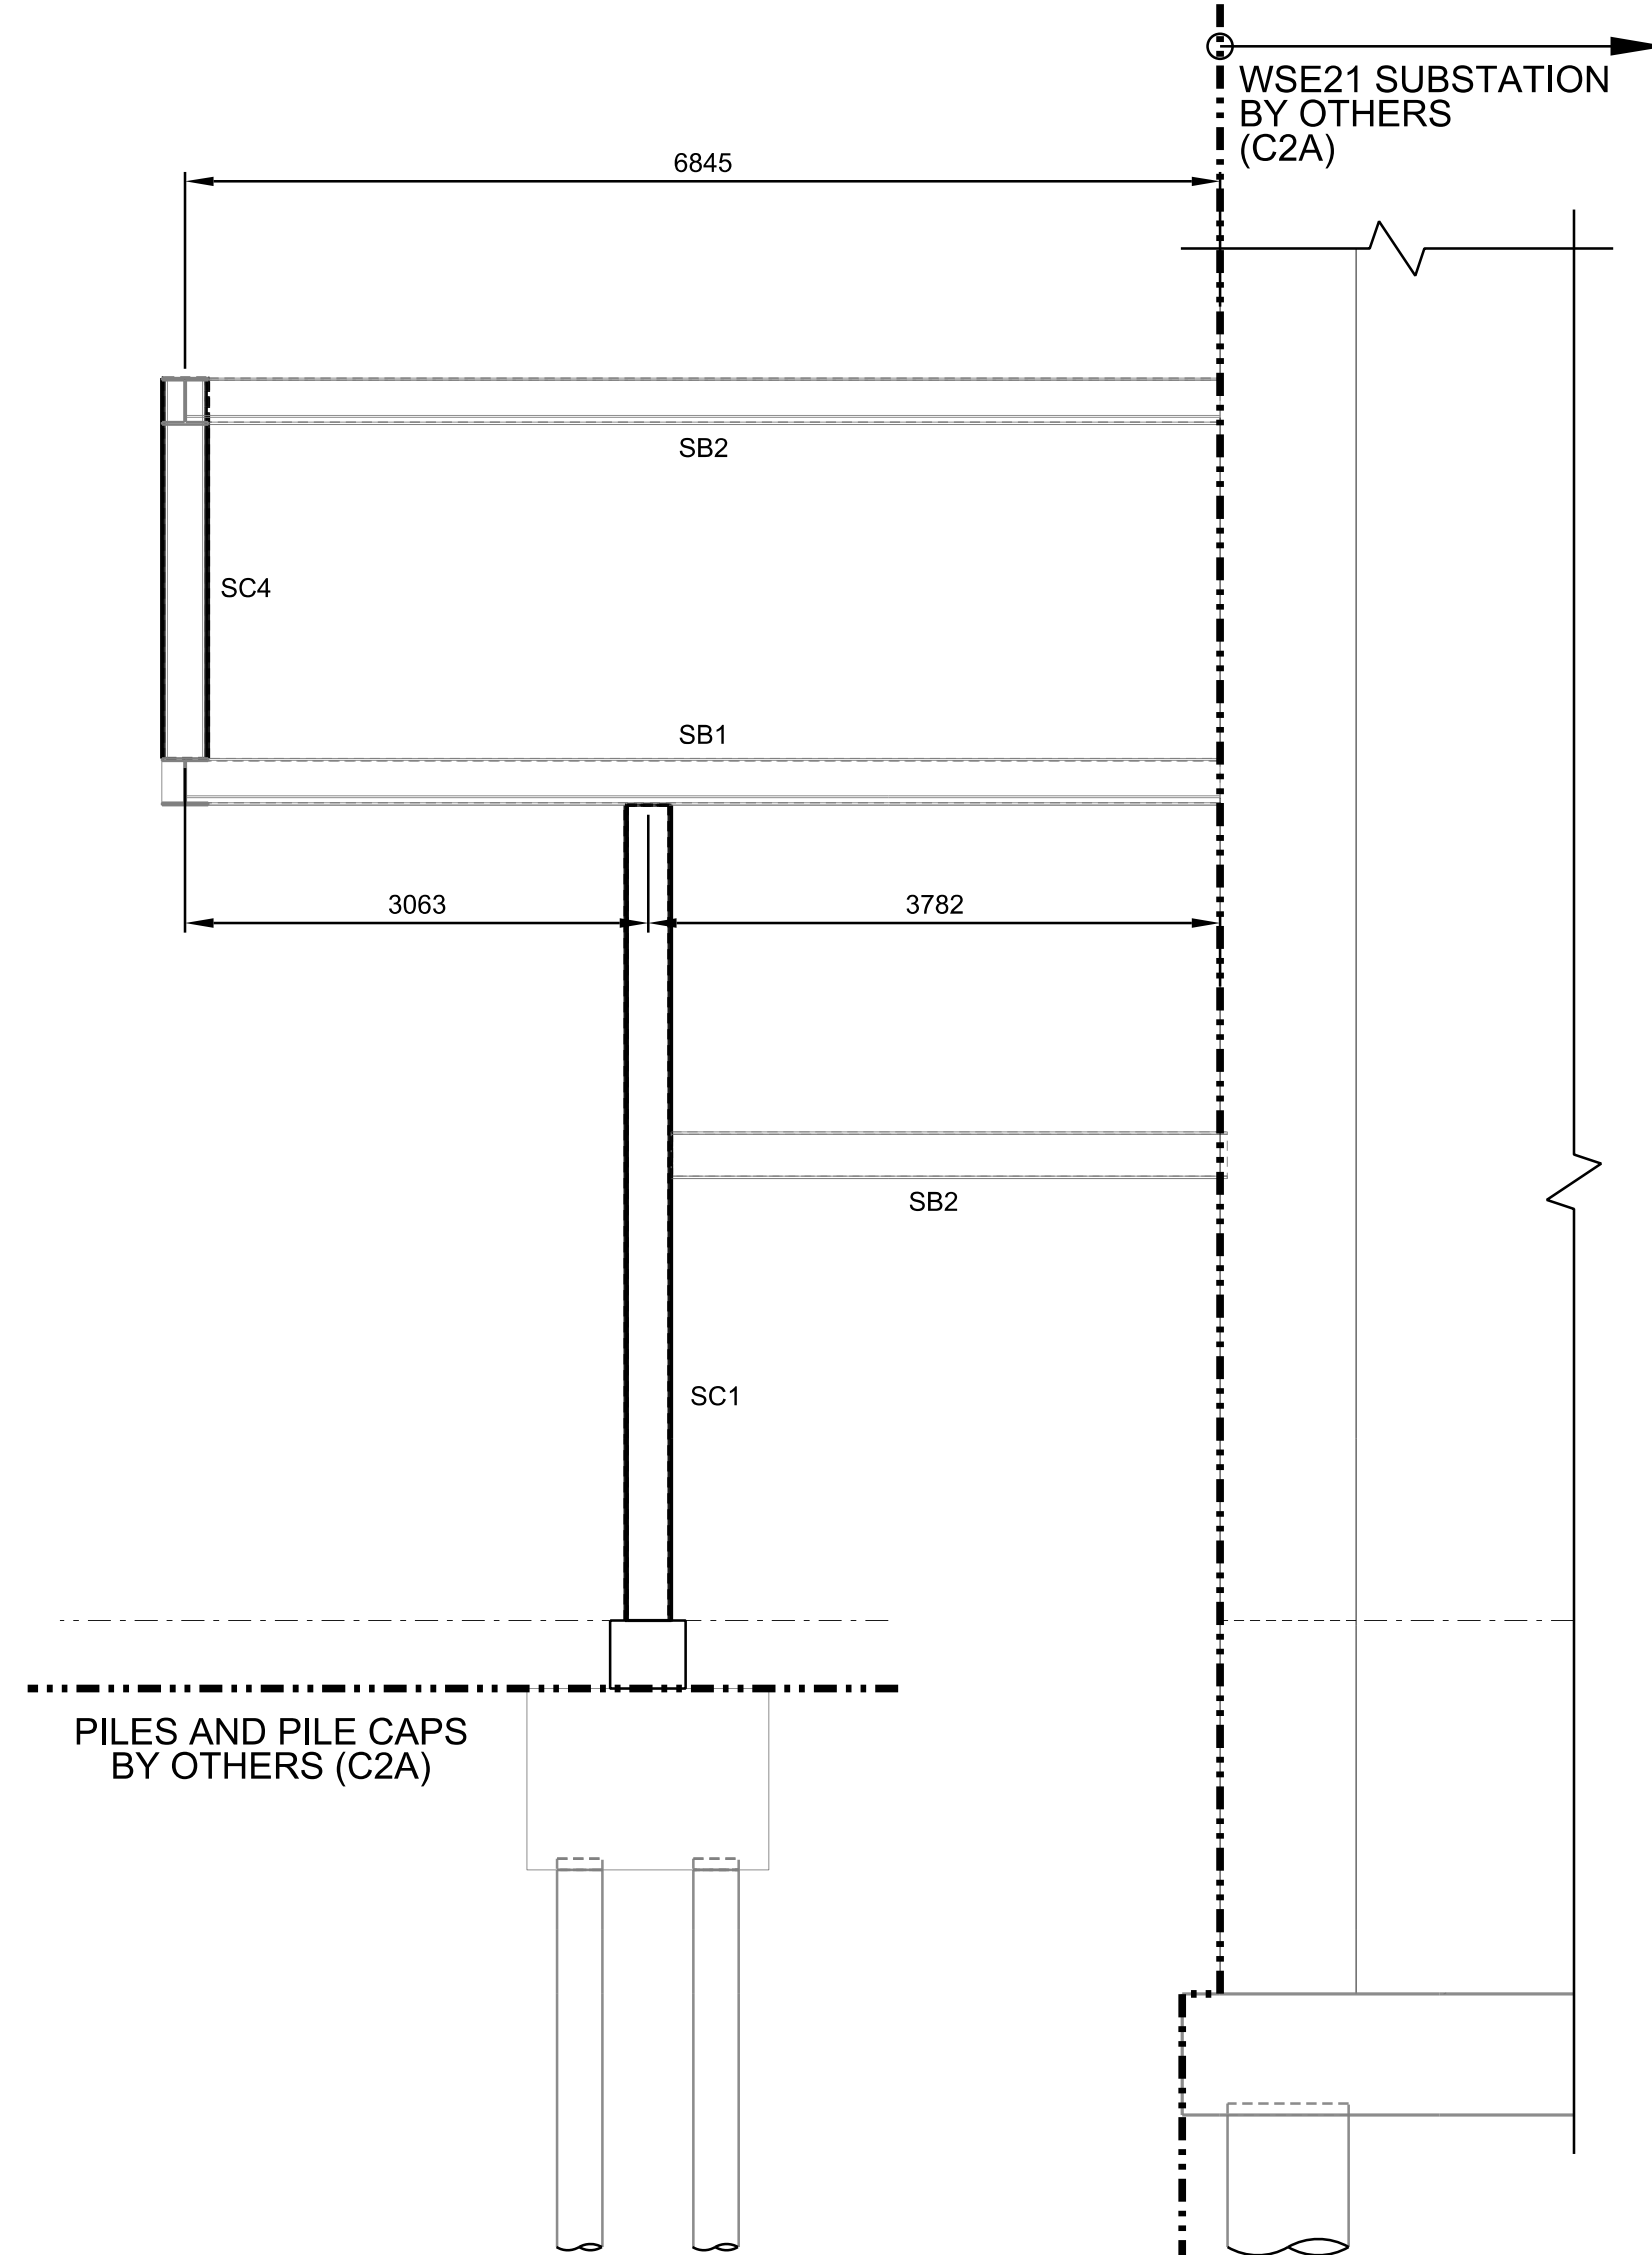

SECTION C - C
SCALE 1:50

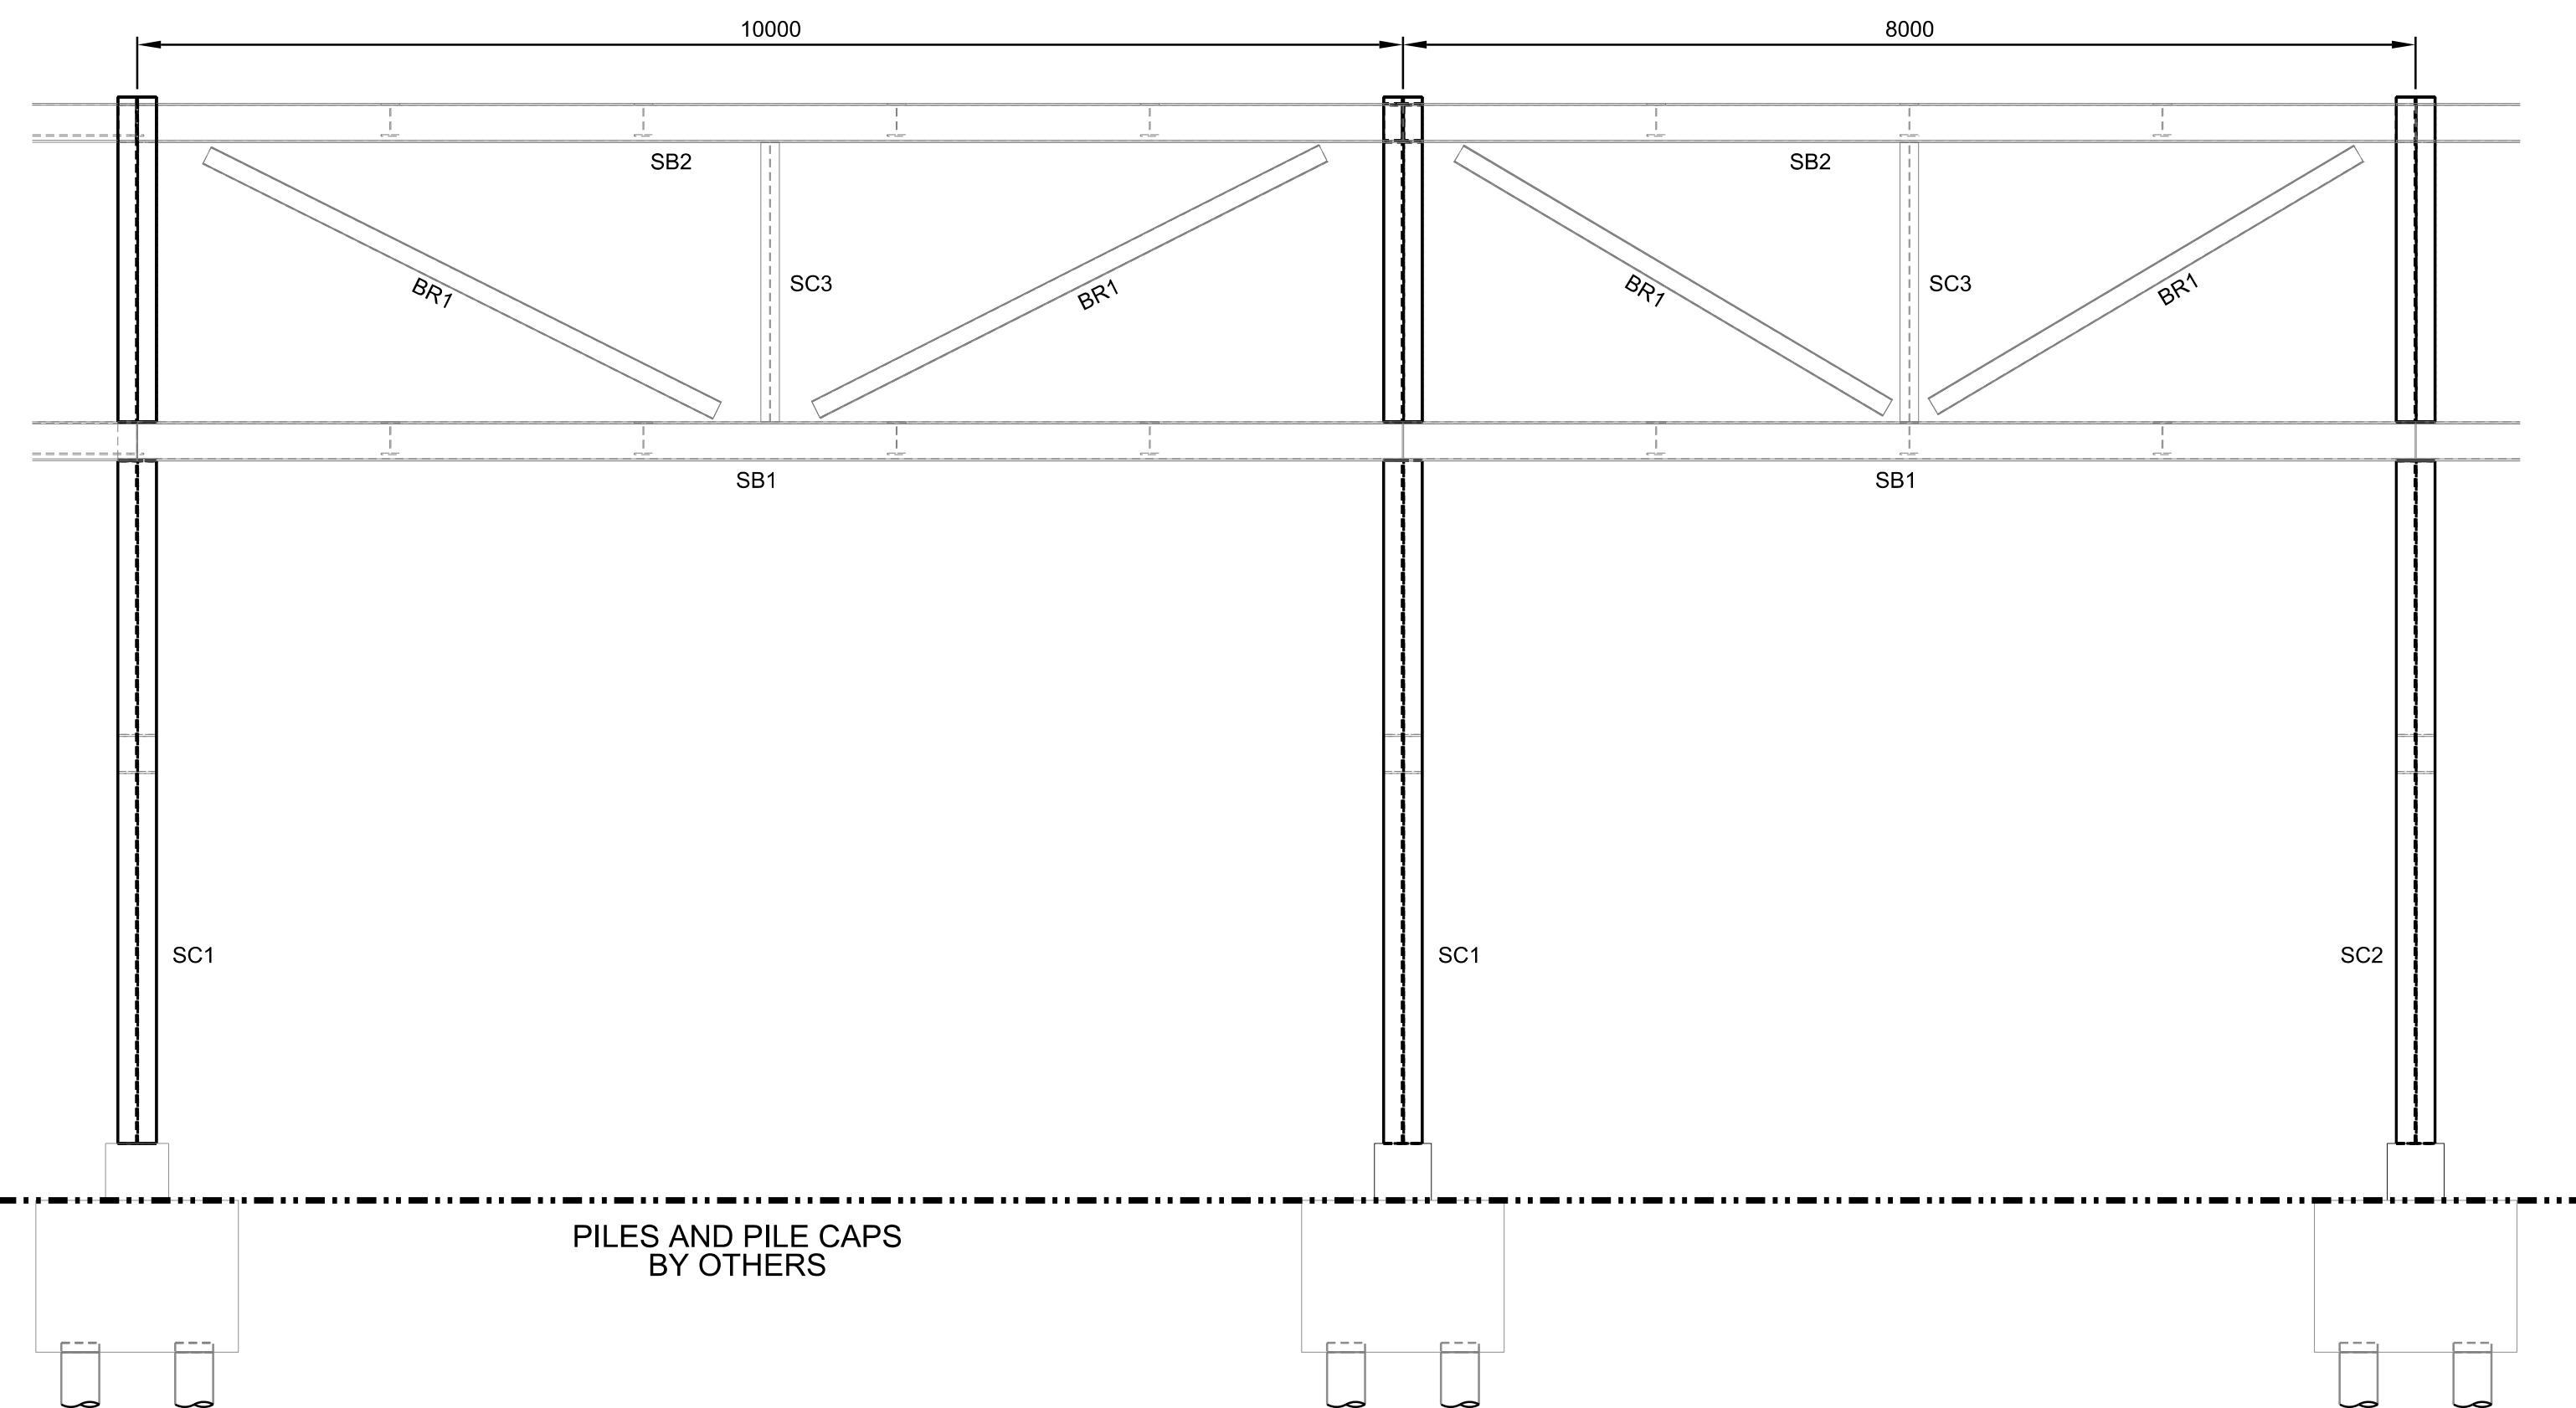


TYPICAL ELEVATION
SCALE 1:50

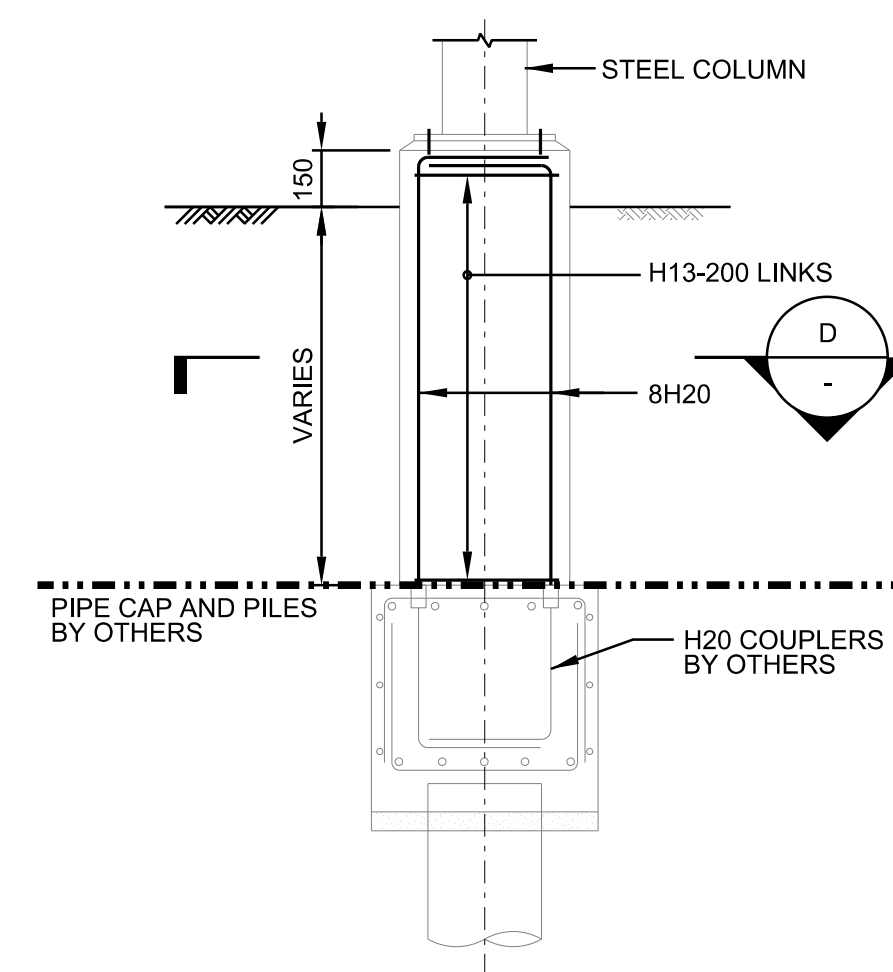



TYPICAL STUMP DETAILS
SCALE 1:20

STEEL MEMBER LIST	
MARK	DESCRIPTION
SC1	UC 305x305x97 kg/m
SC2	UC 254c254x73 kg/m
SC3	UC 152x152x23 kg/m
SC4	UC 203x203x46 kg/m
SB1	UC 203x203x60 kg/m
SB2	UC 203x203x46 kg/m
BR1	UC 152x152x23 kg/m

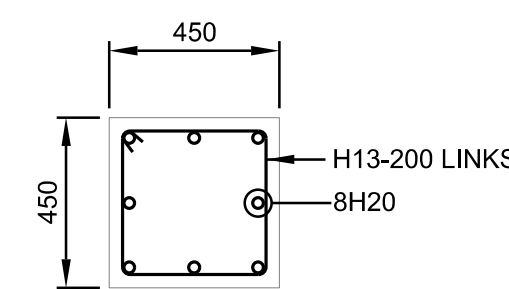

SECTION D - D
SCALE 1:20

- NOTES:
1. THE SETTING OUT, LAYOUT, DIMENSIONS, STEEL MEMBER DETAILS, REINFORCEMENT DETAILS AND INTERFACING CONNECTIONS SHOWN ARE INDICATIVE ONLY. THE CONTRACTOR SHALL COORDINATE WITH OTHER CONTRACTORS, AND DESIGN AND BUILD AND PIPE RACK TO COMPLY WITH THE SPECIFICATIONS.

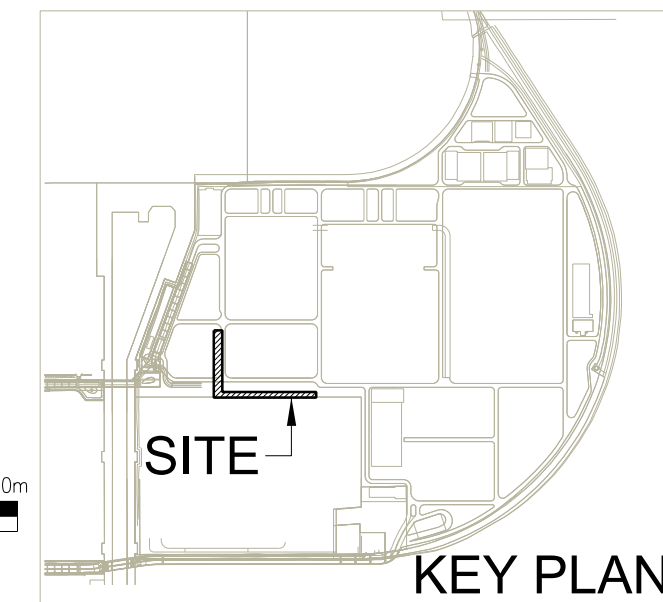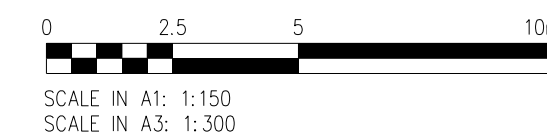

TENDER

T1	20/05/22	ISSUED FOR TENDER	SW	OMW
REV	DATE	DESCRIPTION	REVIEWED	AUTHORISED

CLIENT:

PUB SINGAPORE'S NATIONAL WATER AGENCY

PROGRAMME MANAGER:

bmies AECOM
A JOINT VENTURE DELIVERING THE DTSS2 PROJECT

CONSULTANT:

Jacobs
CH2M HILL Singapore Pte Ltd

PROJECT TITLE:

TUAS WATER RECLAMATION PLANT (TWRP)
DTSS PHASE 2

DRAWING TITLE

NOTIONAL
PIPE RACK SECTIONS,
ELEVATION AND STUMP DETAILS

DRAFTED: OML	DESIGNED: DC	SHEET SIZE: A1
DRAFTING CHECK: GB	DESIGN CHECK: SW	SCALE: AS SHOWN
DATE: 21/03/22	REVIEWED: OMW	PBS: 131101
CONTRACT: C4B	DRAWING NUMBER: PUB-DTSS2-TWRP SHEET NUMBER: WSW41-S-3001	REVISION: T1

THIS DRAWING IS COPYRIGHT