




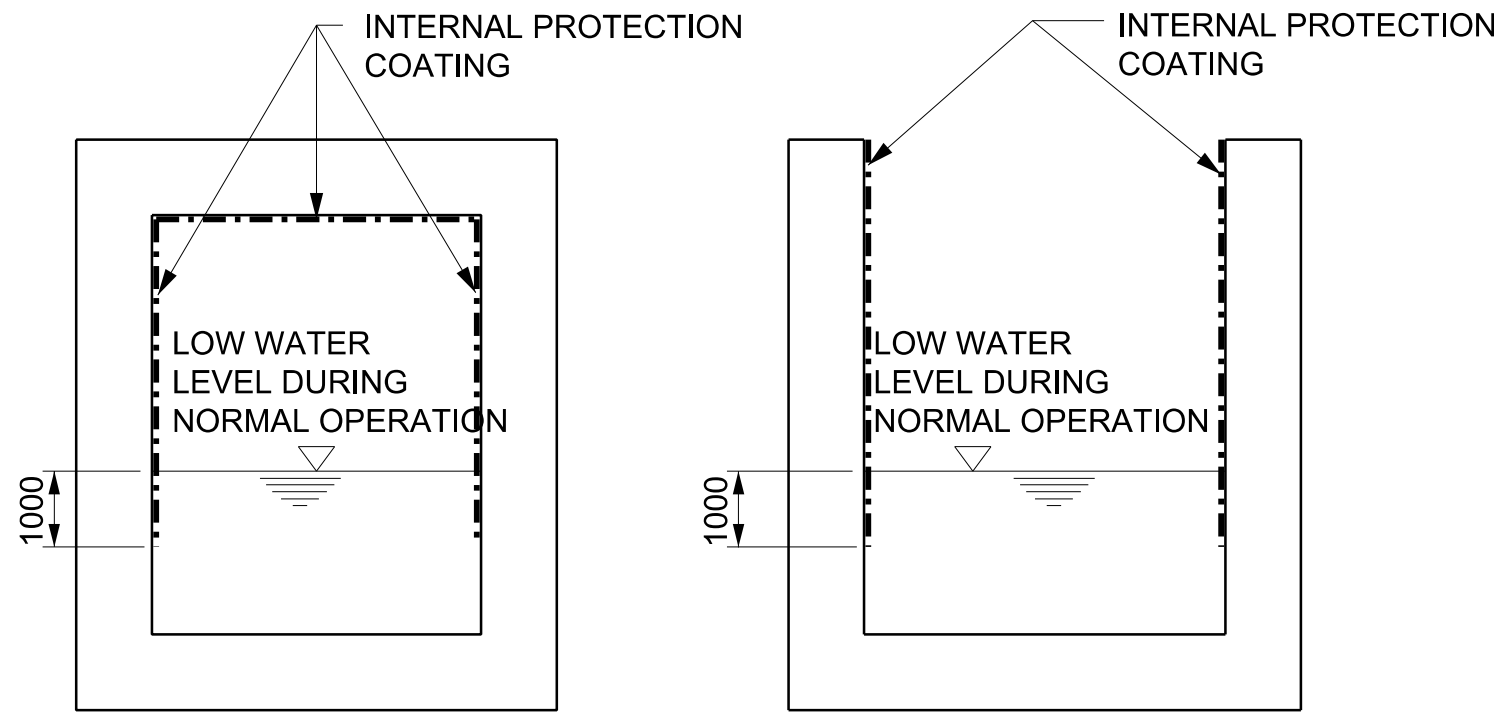

COVERAGE TYPE 1
N.T.S.

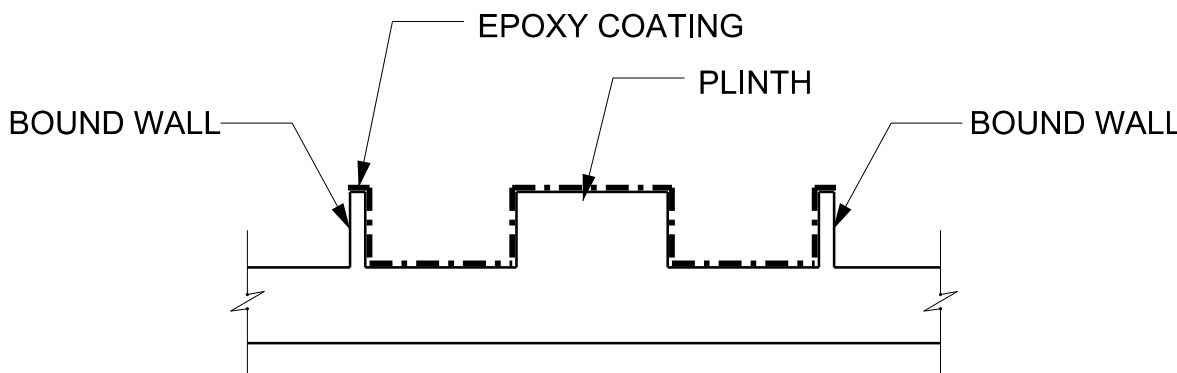

COVERAGE TYPE 3
N.T.S.

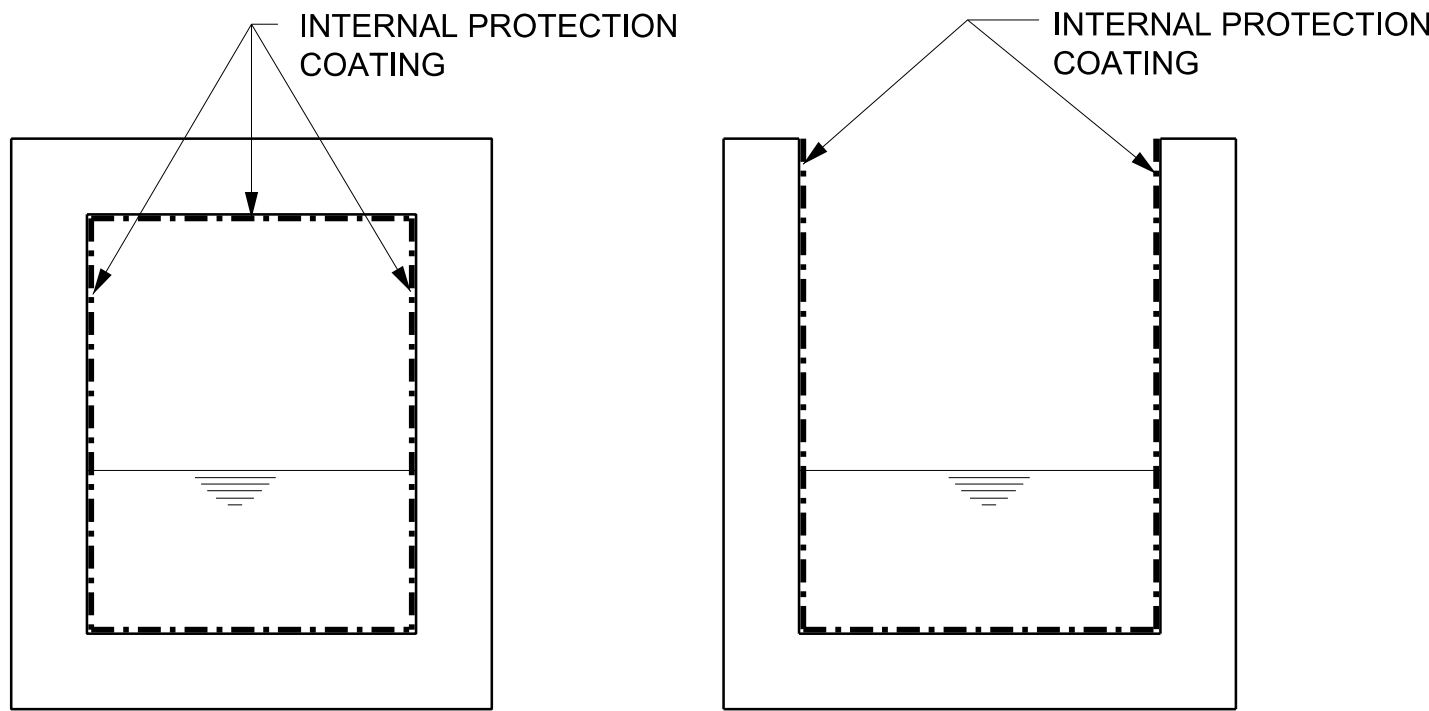

COVERAGE TYPE 2
N.T.S.

INTERNAL PROTECTION COATING
N.T.S.

- NOTES:
1. WATER LEVELS AT THE VARYING TANKS/ CHANNELS SHALL BE BASED ON THE HYDRAULIC PROFILE.
 2. DRAWING SHALL BE READ IN CONJUNCTION WITH PARTICULAR SPECIFICATION APPENDIX P3A.

TENDER

T1	20/05/22	ISSUED FOR TENDER	SW	OMW
REV	DATE	DESCRIPTION	REVIEWED	AUTHORISED

CLIENT:



PROGRAMME MANAGER:



CONSULTANT:



PROJECT TITLE:

TUAS WATER RECLAMATION PLANT (TWRP)
DTSS PHASE 2

DRAWING TITLE

STANDARD DETAILS
INTERNAL PROTECTION COATING

DRAFTED: OML	DESIGNED: DC	SHEET SIZE: A1
DRAFTING CHECK: GB	DESIGN CHECK: SW	SCALE: N.T.S.
DATE: 17/05/22	REVIEWED: OMW	PBS: 131101

CONTRACT:	DRAWING NUMBER:
C4B	PUB-DTSS2-TWRP
SHEET NUMBER:	REVISION:
WSW41-S-5001	T1

THIS DRAWING IS COPYRIGHT