


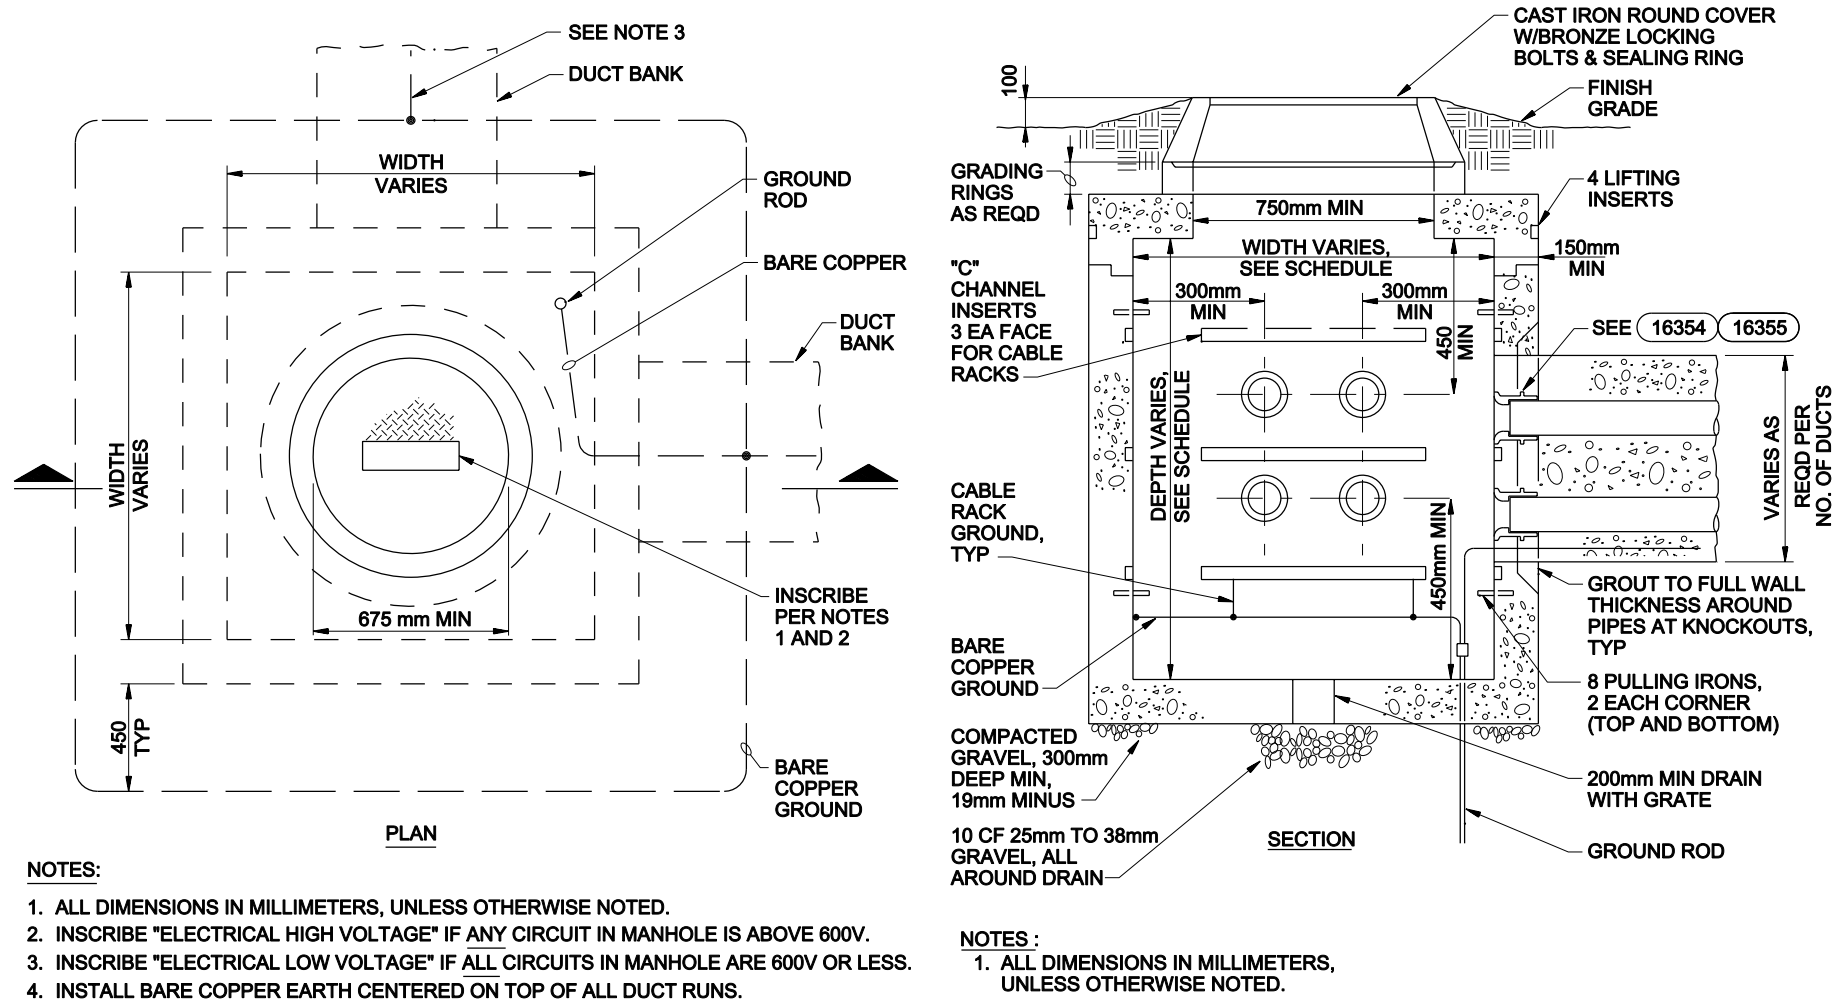

MANHOLE-WITH GROUNDING

NTS

STANDARD DETAIL

16351

JACOBS