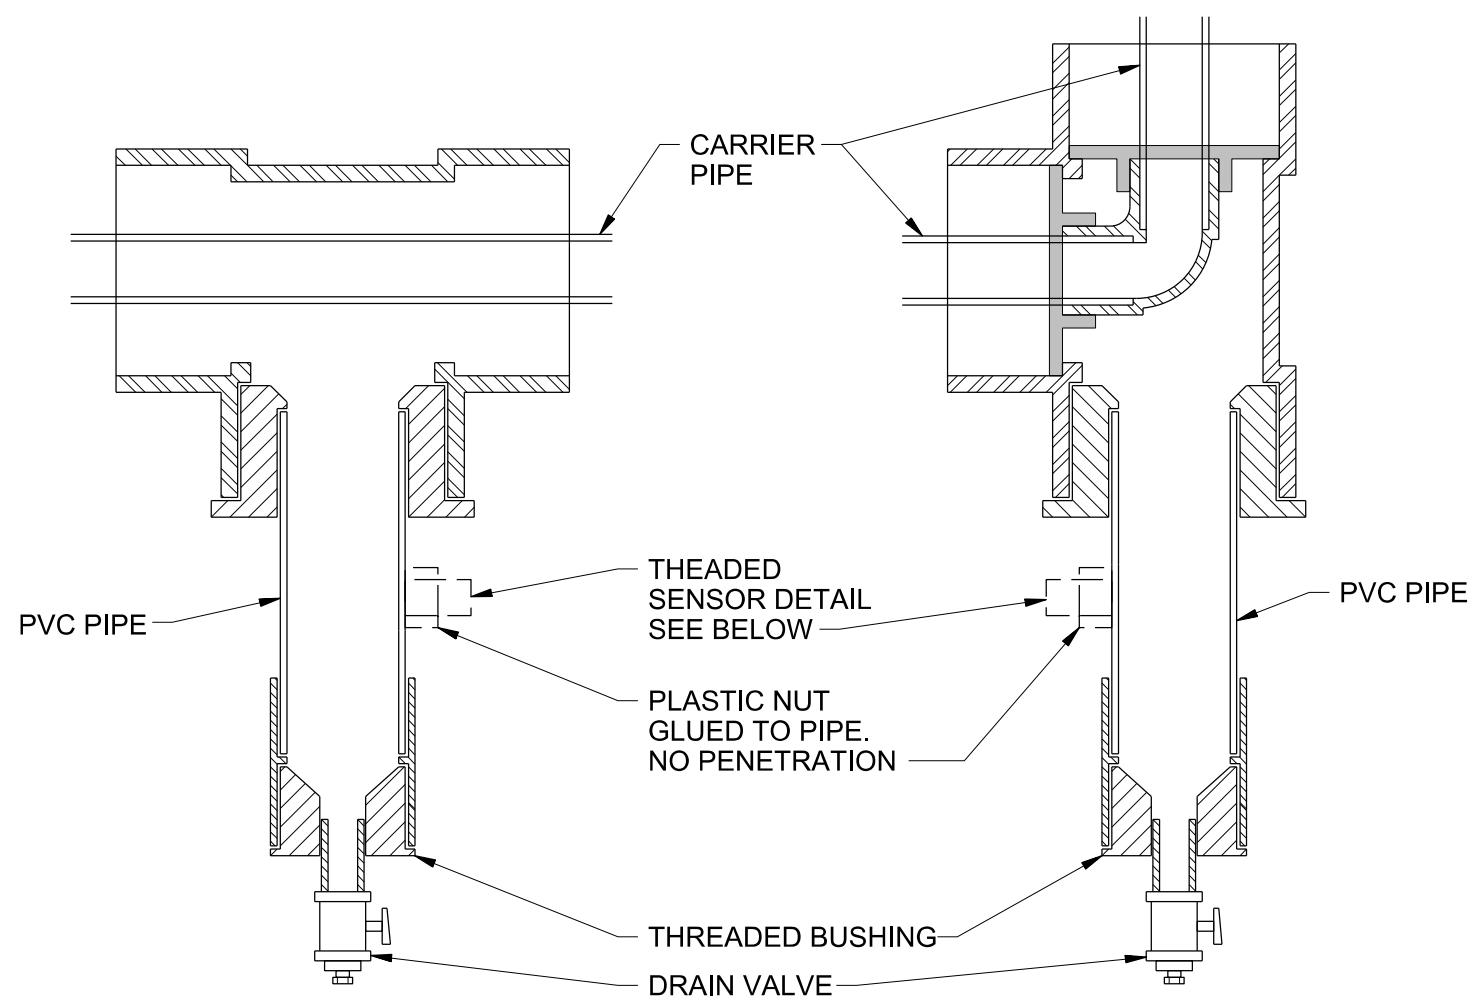
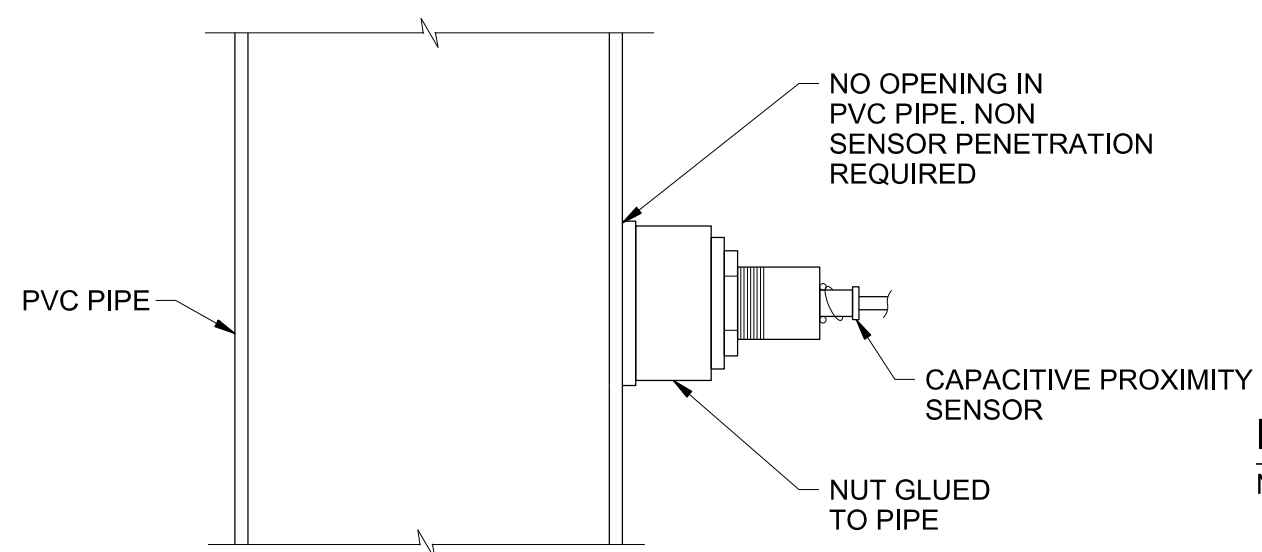


IN - LINEEND OF RUNSENSOR DETAIL

STANDARD DETAIL

GENERAL NOTES:

1. ALL FITTINGS ARE FACTORY TESTED
2. CONTAINMENT TEE SIZED PER SYSTEM REQUIREMENT.

LEAK DETECTION, DOUBLE-WALL CONTAINMENT PIPE

NTS

13280

JACOBS