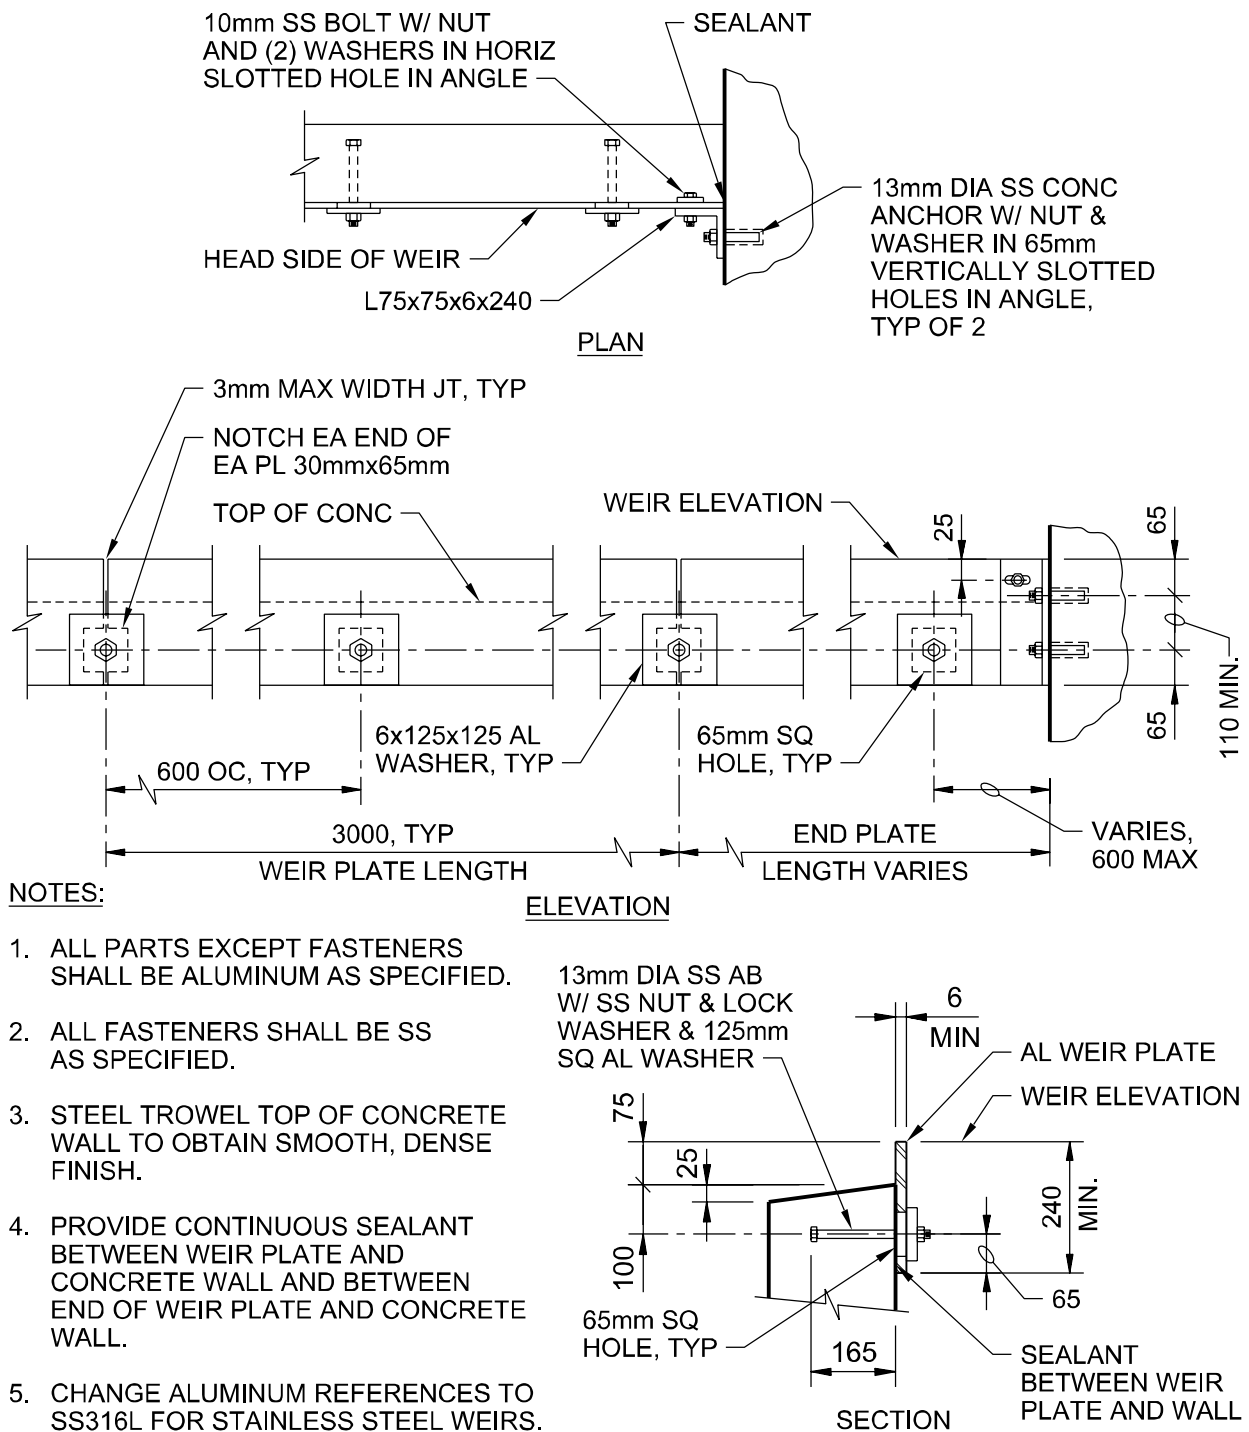


**STRAIGHT EDGE WEIR - TYPE A**

NTS

ALUMINUM

STANDARD DETAIL

DETAIL 1 OF 2

15990

JACOBS