


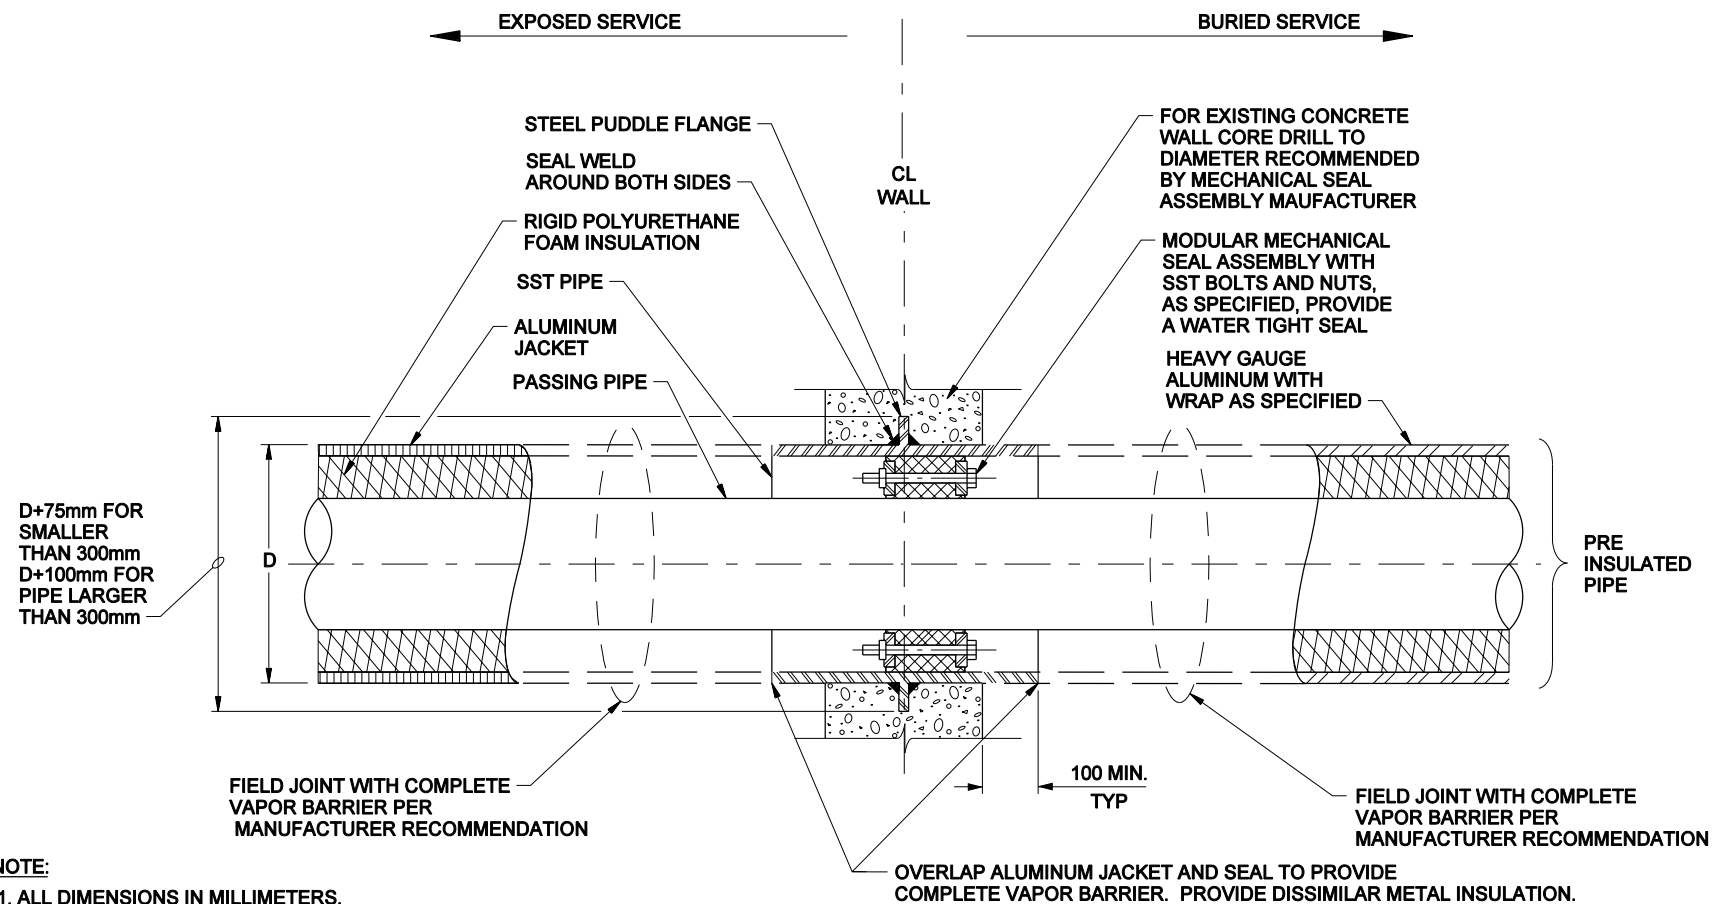

NOTE:

1. ALL DIMENSIONS IN MILLIMETERS, UNLESS OTHERWISE NOTED
2. WHERE EXISTING CONCRETE STRUCTURE IS TO BE CORE DRILLED, THE CONTRACTOR SHALL ULTRASONIC TEST OR X-RAY THE AREA FOR EMBEDDED ITEMS BEFORE CORE DRILLING CAN PROCEED. IF EMBEDDED ITEMS ARE FOUND, NOTIFY THE S.O. IMMEDIATELY.

WALL PENETRATION SEAL

NTS

STANDARD DETAIL

15409

JACOBS