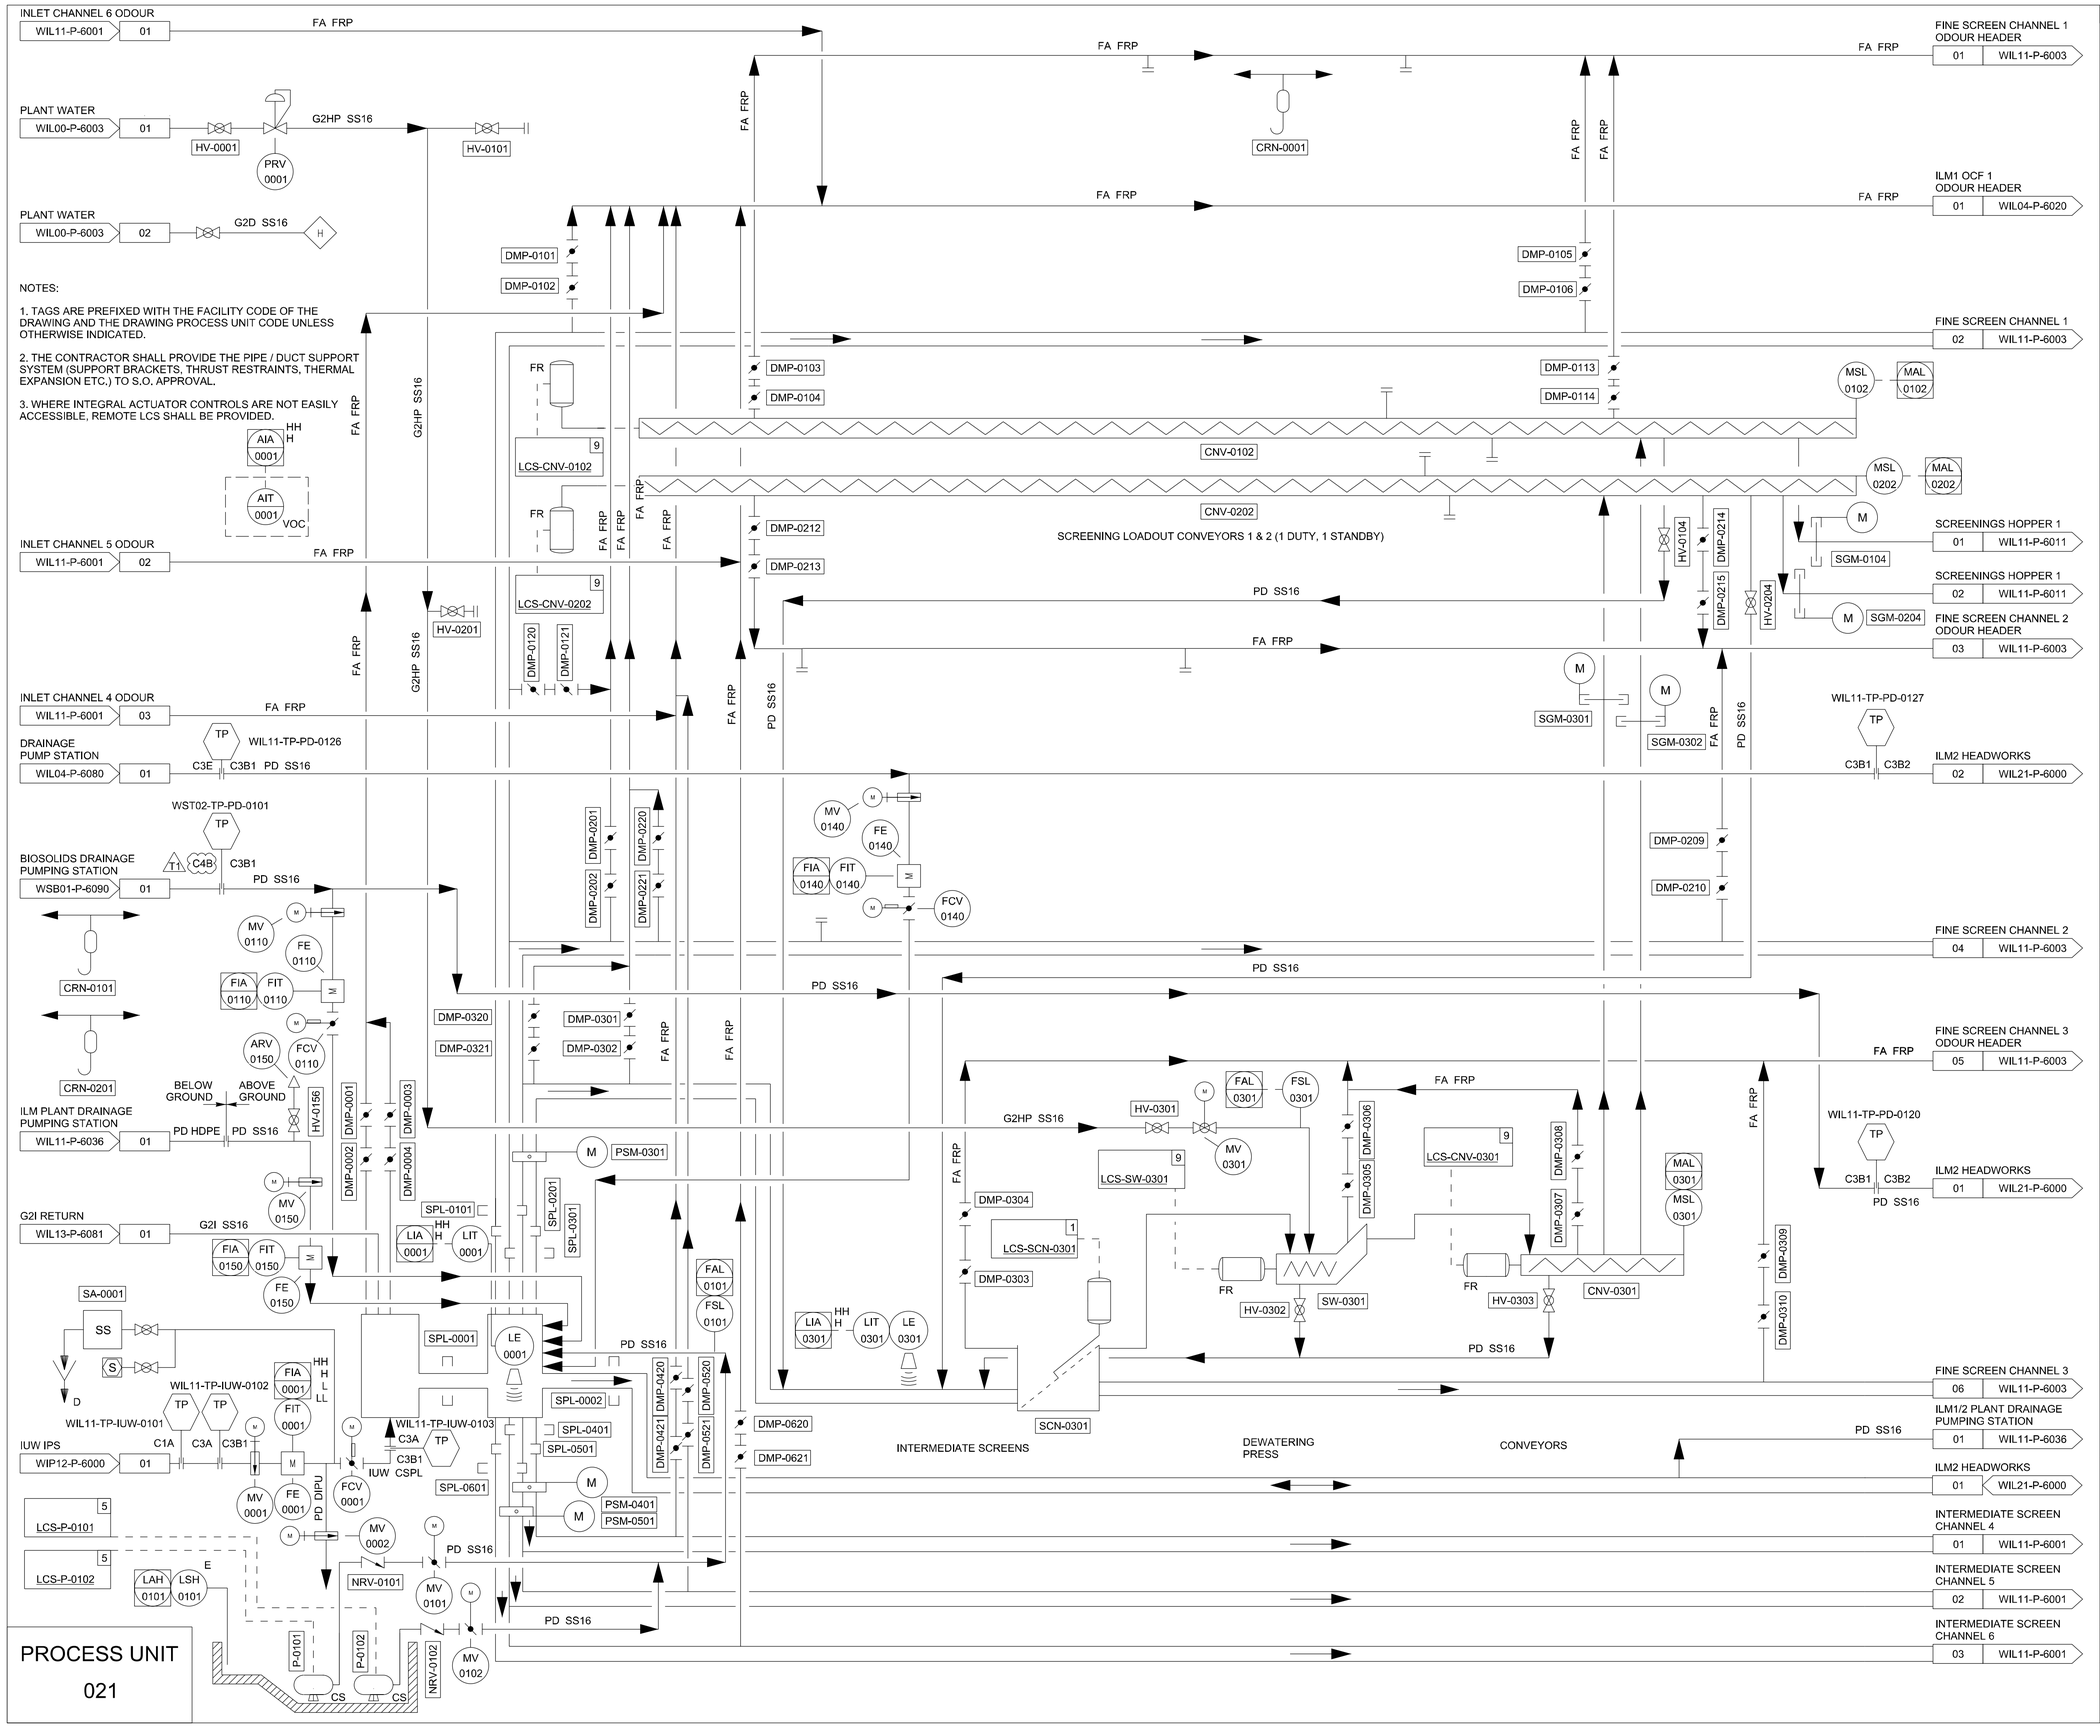


TENDER

REV	DATE	DESCRIPTION	REVIEWED	AUTHORISED
T1	20/05/22	ISSUED FOR TENDER C4B	CN	GOT
T1	03/12/21	ISSUED FOR TENDER C3E	CN	GOT
T2	28/04/21	ISSUED FOR ADDENDUM 2	CN	GOT
T1	17/07/20	ISSUED FOR TENDER C3B1	CN	GOT
T1	24/04/20	ISSUED FOR TENDER C3A	CN	GOT

CLIENT:
PUB SINGAPORE'S NATIONAL WATER AGENCY

PROGRAMME MANAGER:
binnies AECOM
A JOINT VENTURE DELIVERING THE DTSS2 PROJECT

CONSULTANT:
Jacobs
CH2M HILL SIngapore Pte Ltd

PROJECT TITLE:
TUAS WATER RECLAMATION PLANT (TWRP)
DTSS PHASE 2

DRAWING TITLE
P&ID
INTERMEDIATE
SCREENS 1, 2 & 3

DRAFTED: EM	DESIGNED: SYC	SHEET SIZE: A1
DRAFTING CHECK: DW	DESIGN CHECK: DT	SCALE: NTS
DATE: 12/05/17	REVIEWED: CN	PBS: 131101

CONTRACT: -
DRAWING NUMBER: PUB-DTSS2-TWRP
SHEET NUMBER: WIL11-P-6000
REVISION: T1

THIS DRAWING IS COPYRIGHT