



PIPE RACK PLAN

SCALE 1:300

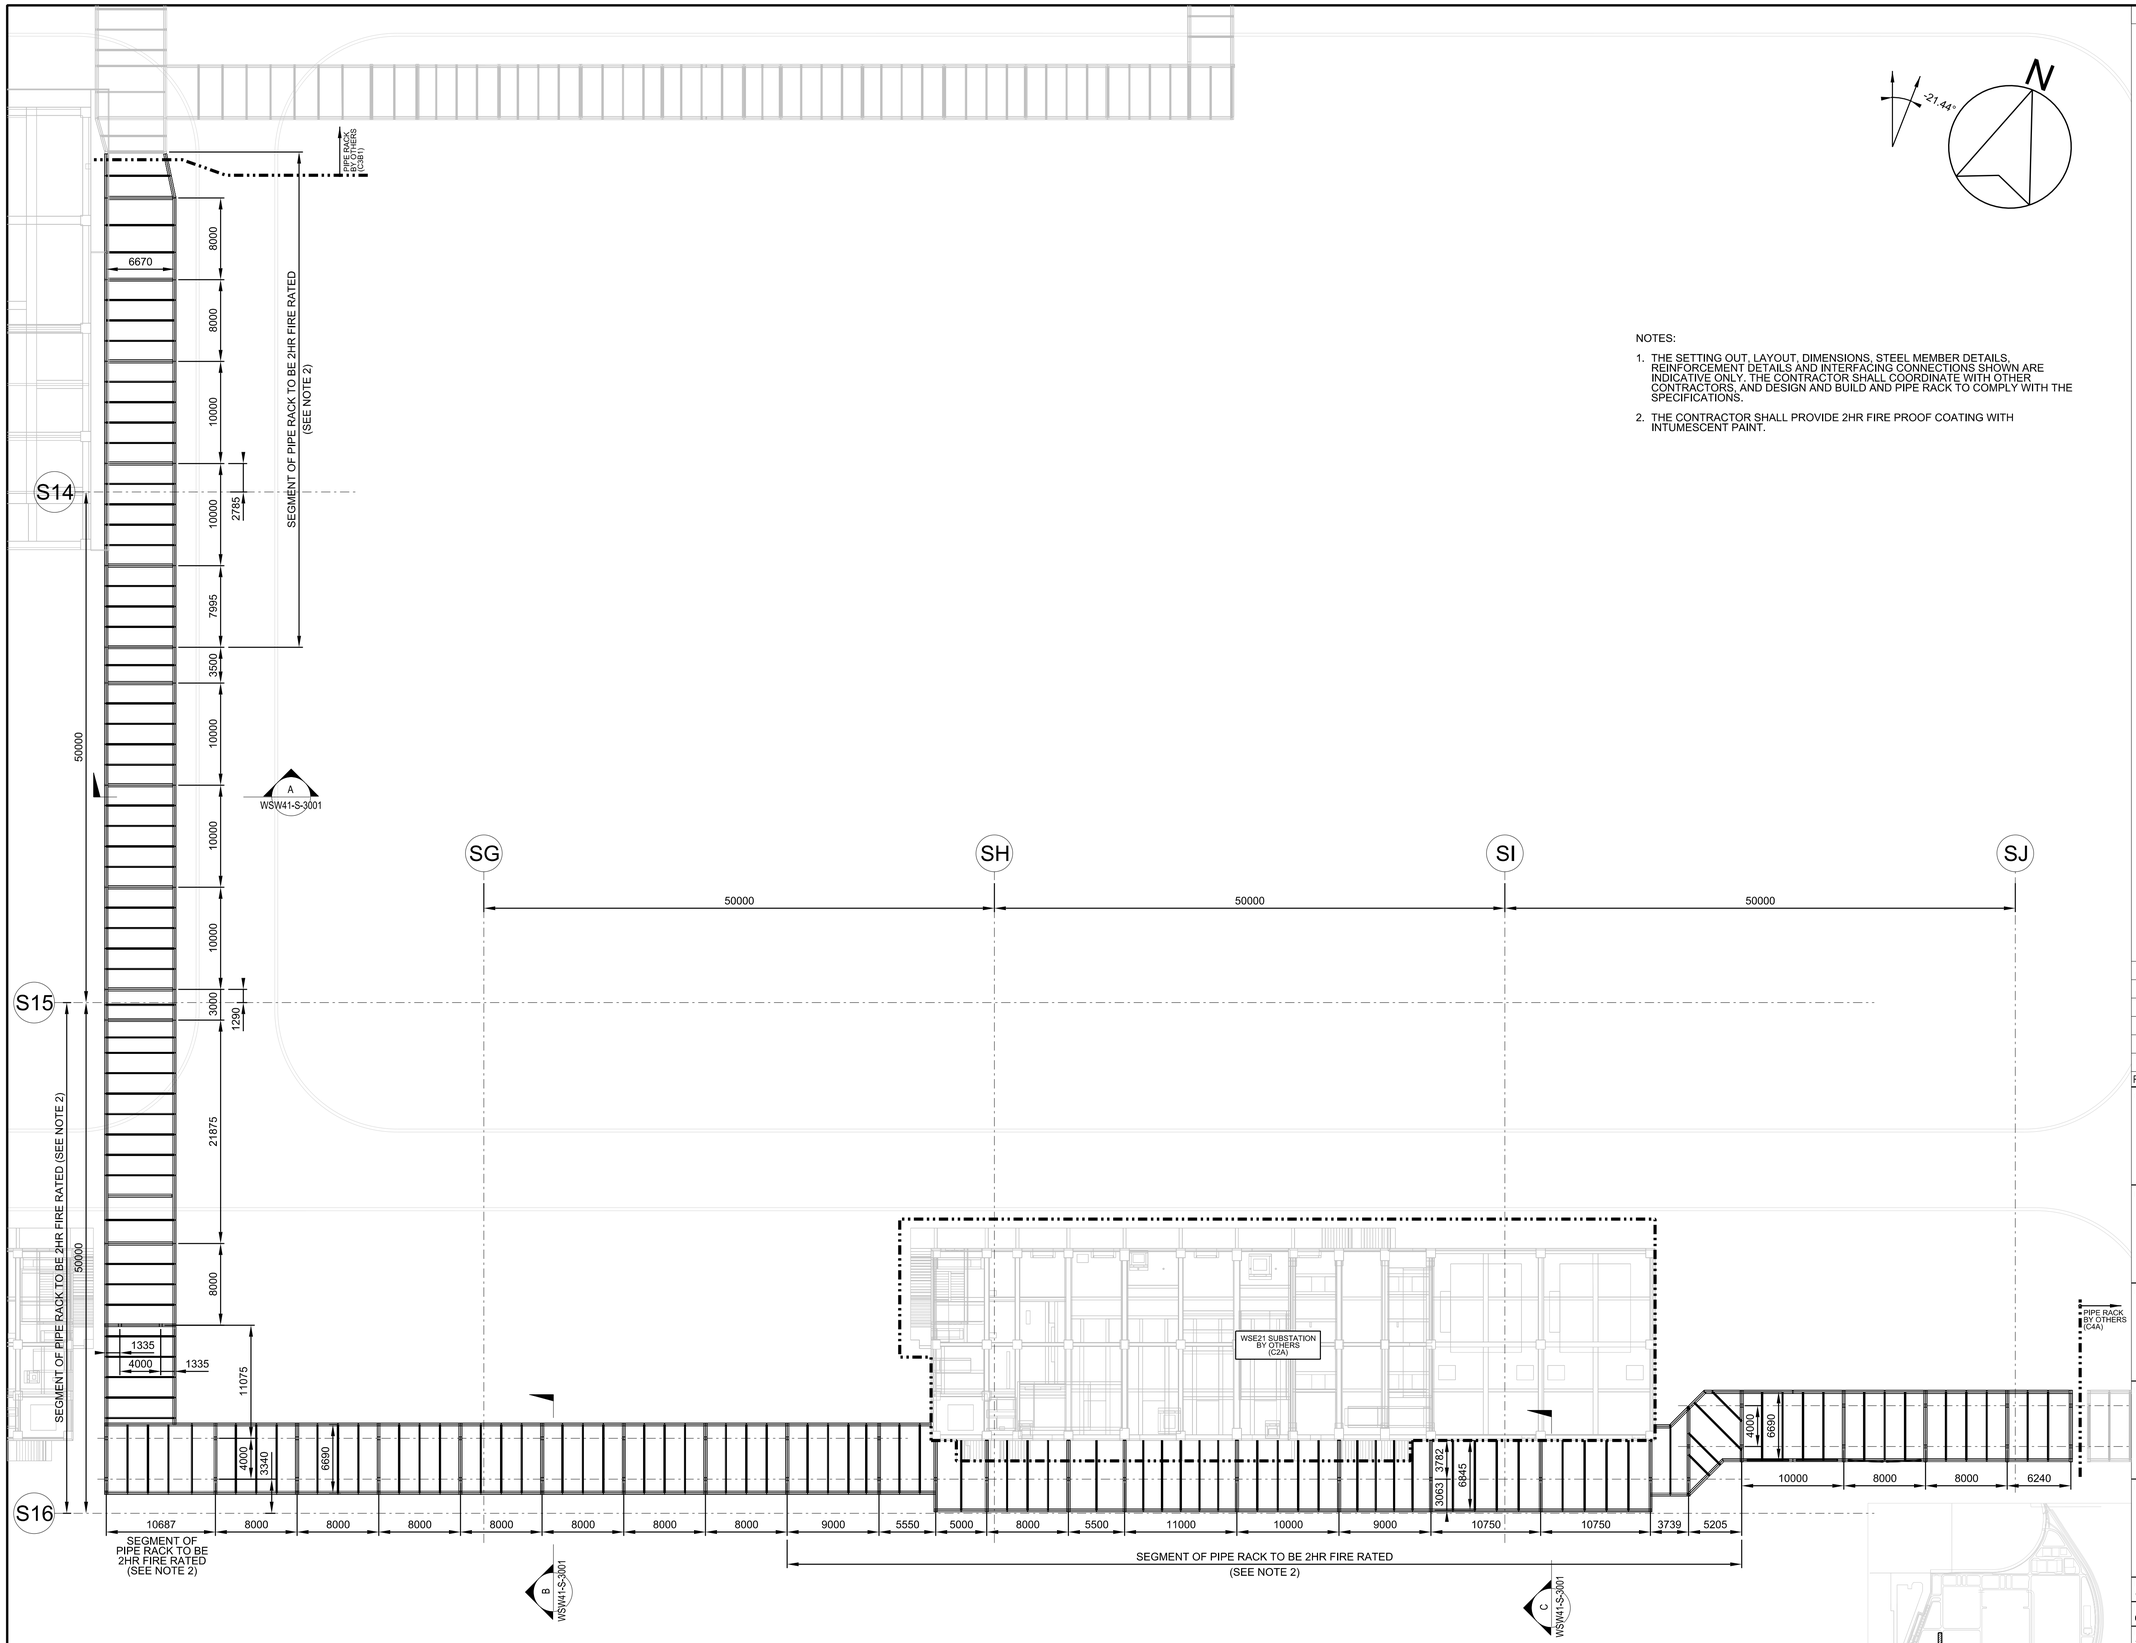


NOTES:

1. THE SETTING OUT, LAYOUT, DIMENSIONS, STEEL MEMBER DETAILS, REINFORCEMENT DETAILS AND INTERFACING CONNECTIONS SHOWN ARE INDICATIVE ONLY. THE CONTRACTOR SHALL COORDINATE WITH OTHER CONTRACTORS, AND DESIGN AND BUILD AND PIPE RACK TO COMPLY WITH THE SPECIFICATIONS.
2. THE CONTRACTOR SHALL PROVIDE 2HR FIRE PROOF COATING WITH INTUMESCENT PAINT.




KEY PLAN

0 2.5 5 10m

SCALE IN A1: 1:150
SCALE IN A3: 1:300

TENDER

| REV | DATE | DESCRIPTION | REVIEWED | AUTHORISED |
|---|---|---|---|---|
| T1 | 20/05/22 | ISSUED FOR TENDER | SW | OMW |

CLIENT:

PUB SINGAPORE'S NATIONAL WATER AGENCY

PROGRAMME MANAGER:

binnies AECOM

A JOINT VENTURE DELIVERING THE DTSS2 PROJECT

CONSULTANT:

Jacobs

CH2M HILL Singapore Pte Ltd

PROJECT TITLE:

TUAS WATER RECLAMATION PLANT (TWRP)
DTSS PHASE 2

DRAWING TITLE

NOTIONAL
PIPE RACK PLAN

| | | |
|---|---|---|
| DRAFTED: OML | DESIGNED: DC | SHEET SIZE: A1 |
| DRAFTING CHECK: GB | DESIGN CHECK: SW | SCALE: AS SHOWN |
| DATE: 21/03/22 | REVIEWED: OMW | PBS: 131101 |

CONTRACT: C4B

DRAWING NUMBER: PUB-DTSS2-TWRP

SHEET NUMBER: WSW41-S-1001

REVISION: T1

THIS DRAWING IS COPYRIGHT